

精神专科医院建筑设计方案参考图集

《精神专科医院建筑设计方案参考图集》编制组

2009. 12

目 录

编制说明	2
《精神专科医院建筑设计方案参考图集》设计要点	3
150 床规模设计方案一	6
150 床规模设计方案二	11
300 床规模设计方案一	15
300 床规模设计方案二	19
500 床规模设计方案一	24
500 床规模设计方案二	29
大样示意图	33

编制说明

为了做好全国精神专科医院建设技术指导工作，卫生部组织中国中元国际工程公司、华东建筑设计研究院有限公司、中国建筑西南建筑设计研究院和部分精神卫生专业机构专家组成编制组，编制了《精神专科医院建筑设计方案参考图集》。

在卫生部规划财务司及疾病预防控制中心的统一协调和组织下，编制组广泛听取了国内精神科临床及管理等方面专家的建议，并征求了各省、自治区及直辖市卫生厅（局）意见。在此对为本图集编制付出辛勤劳动的各省、自治区及直辖市卫生厅（局）及北京大学第六医院、北京安定医院、北京回龙观医院、上海市精神卫生中心、天津精神卫生中心、四川大学华西医院、广东省精神卫生研究所、浙江省精神卫生办公室的领导和专家，向为编制组提供资料的北京、天津、上海市和四川、河南、浙江、广东省的有关精神专科医院和精神卫生中心表示由衷的感谢！

限于编制组自身的知识结构和学术水平，图集中谬误之处恐难避免，希望医疗及建筑领域专家批评指正。如本图集能为精神专科医院建设提供些许帮助，当是编制组各位同仁最为欣喜之事。

编制组向以下个人致谢（以姓氏笔划为序）：

孔灵芝 万 钧 王润田 王 翼 石其昌 冯 葵 任西岳 许海涛
李滋新 刘 魁 邱茂新 严 俊 辛春华 陈海勇 吴翔天 林永强
赵全德 徐卫红 秦 如 高璐璐 黄 平 黄锡璆 蒋 清

《精神专科医院建筑设计方案参考图集》编制组

2009. 12

《精神专科医院建筑设计方案参考图集》设计要点

1、 总则

- 1.1、为提高精神专科医院的设计水平，根据国家有关设计标准及规范，编制本套《精神专科医院建筑设计方案参考图集》。
- 1.2、本图集包括 150 床、300 床及 500 床规模精神专科医院设计方案各二个，为各级精神专科医院提供设计参考。
- 1.3、本图集仅为参考，不作为规范性要求。

2、 主要功能单元构成

150 床、300 床及 500 床规模精神卫生专科医院应根据医疗工作特点及自身工作需要合理配置功能单元，本图集按下表配置主要功能单元。

主要功能单元构成

床位规模	150 床	300 床	500 床
急诊部	-----	1、 急 诊	1、 急 诊
门 诊 部	1、 精 神 科 门 诊 2、 社 区 防 治 3、 精 神 医 学 鉴 定 科	1、 精 神 科 门 诊 2、 临 床 心 理 科 3、 老 年 精 神 科 4、 儿 少 精 神 科 5、 神 经 症 科 6、 康 复 科	1、 精 神 科 门 诊 2、 临 床 心 理 科 3、 老 年 精 神 科 4、 儿 少 精 神 科 5、 神 经 症 科 6、 康 复 科

		7、 社 区 防 治 8、 精 神 医 学 鉴 定 科	7、 社 区 防 治 8、 精 神 医 学 鉴 定 科
医 技 科 室	1、 药 剂 科 2、 检 验 科 3、 放 射 科 4、 B 超 室 5、 脑 电 图 室 与 睡 眠 功 能 检 查 室 6、 中 心 供 应 室 7、 病 案 室 8、 心 电 图 室 9、 工 娱 疗 室 10、 营 养 室	1、 药 剂 科 2、 检 验 科 3、 放 射 科 4、 B 超 室 5、 脑 电 图 与 睡 眠 功 能 检 查 室 6、 中 心 供 应 室 7、 病 案 室 8、 心 电 图 室 9、 无 抽 搐 电 休 克 治 疗 室 10 心 理 测 查 室 11、脑 功 能 治 疗 室 12、 工 娱 疗 室 13、 营 养 室	1、 药 剂 科 2、 检 验 科 3、 放 射 科 4、 B 超 室 5、 脑 电 图 与 睡 眠 功 能 检 查 室 6、 中 心 供 应 室 7、 病 案 室 8、 心 电 图 室 9、 无 抽 搐 电 休 克 治 疗 室 10、 心 理 测 查 室 11、 心 理 治 疗 室 12、 脑 功 能 治 疗 室 13、 工 娱 疗 室 14、 营 养 室
住院部	1、 护 理 单 元	1、 护 理 单 元	1、 护 理 单 元

保障系统	1、设备机房 2、传达室 3、总务库房 4、总务修理 5、污水处理 6、垃圾处置 7、锅炉房 8、洗衣房 9、太平间	1、设备机房 2、传达室 3、总务库房 4、总务修理 5、污水处理 6、垃圾处置 7、锅炉房 8、洗衣房 9、太平间	1、设备机房 2、传达室 3、总务库房 4、总务修理 5、污水处理 6、垃圾处置 7、锅炉房 8、洗衣房 9、太平间
行政管理	1、办公用房 2、计算机房 3、图书馆	1、办公用房 2、计算机房 3、图书馆	1、办公用房 2、计算机房 3、图书馆
院内生活	1、职工食堂 2、浴室 3、单身宿舍	1、职工食堂 2、浴室 3、单身宿舍	1、职工食堂 2、浴室 3、单身宿舍
教学科研	-----	-----	1、教室 2、实验室

3、 总平面设计要点

- 3.1、综合考虑城市交通、朝向、风向等因素，合理布局。
- 3.2、功能合理分区，一般分为医疗区、后勤保障区。

- 3.3、规划留有发展或改、扩建余地。
- 3.4、根据用地情况合理安排用地出入口位置和数量，一般设置主入口及后勤辅助出入口。
- 3.5、本图集不考虑传染病病人的收治。具体建设时可根据承担任务，在院区内设置相对独立的传染病诊疗功能单元。
- 3.6、充分利用地形、防护间距和其它空地布置绿化及病人活动场地。
- 3.7、室外活动场地邻近病房设置，本图集按 5m²/床设置。供急性病人使用的室外活动场地应采取必要的封闭措施。

4、 门诊部、急诊部设计要点

- 4.1、门诊部设在靠近医院主要交通入口处，与急诊部和医技部邻近，并设直通医院内部的联系通路。根据规模、用地情况，门诊部与急诊、医技部可组合为一体。
- 4.2、儿少精神科、精神医学鉴定科、临床心理科考虑设置单独出入口。
- 4.3、门诊部分采用分科候诊，门诊量小的可合科候诊。可采用厅式候诊或廊式候诊形式。
- 4.4、诊室考虑以单人诊室为主，参考方案中单人诊室面积控制在 8-12m² 之间。根据教学等工作需要可设置少量多人诊室。
- 4.5、为方便医护人员交流及相互支援，诊室间应设置医护人员应急出口。
- 4.6、急诊部自成一区，单独设置出入口，便于急救车停靠。并与门诊部、医技部有方便联系。可考虑与门诊部组成一体。

5、 医技部、工娱疗室设计要点

5.1、医技部与门诊、急诊及住院部之间应设有便捷的交通联系，方便各部分病人使用。可与门诊、急诊组成一体。

5.2、医技部内应考虑将医护人员工作区域与病人活动区域相对独立设置，避免相互之间的干扰。

5.3、工娱疗室设置位置应最大限度的方便住院病人到达。并应与门诊部、急诊部及医技部的其他功能适当分隔。可考虑与住院部组合为一体。参考方案按 $1-1.5\text{m}^2/\text{床}$ 设置工娱疗室的净使用面积。

6、 住院部设计要点

6.1、护理单元按设置 40 床考虑。

6.2、护理单元内应设置独立的医护人员内部工作区，该区域应与病人活动区域设置必要、可靠的隔离措施。

6.3、护理单元内的病房以 4-6 床间为主，附以少量单床间。参考方案中将单人间病

床数控制在护理单元总床位数的 10%以内。

6.4、各护理单元内宜设置兴奋室一间，供急性发病病人住院使用，其墙面、地面等部位均采用必要的安全保护措施。

6.5、护理单元内应设置一定规模的病人餐厅及活动室。参考方案按 $2-2.5\text{m}^2/\text{床}$ 设置餐厅及活动室的净使用面积。

6.6、住院部出入院处可独立设置，规模较小的医院也可与门诊挂号、收费合并设置。

7、 其它部分设计要点

7.1、保障系统与院内生活部分可合并设置，并应考虑在院区内独立成区，靠近后勤辅助出入口。

7.2、行政办公部分可独立设置，也可与保障系统与院内生活部分合并设置，也可与门诊楼组合设置。

7.3、教学科研部分可与保障系统与院内生活部分合并设置，也可与门诊楼组合设置。




设计要点说明


- 1 采用多层建筑院落的单元化布局，将后勤用房独立，布局紧凑；各功能单元均有天井，形成内部院落空间。
- 2 门诊、医技、行政部分集中设置，由楼层分隔，与住院楼相对独立，避免相互干扰。
- 3 工疗用房与护理单元一体化设计，且位于病房与门诊之间便于住院病人与门诊病人两方的使用。
- 4 病房楼一层为两个护理单元，医护区位各单元端头靠后位置，每个单元有一套医护人员小组，便于病房分科划分。
- 5 这种简洁的体块便于多种方式的平面组合。

主要技术经济指标


用地面积	16800m ²
总建筑面积	8856.14m ²
床位数	152 张
床均面积：	58.26m ² /床

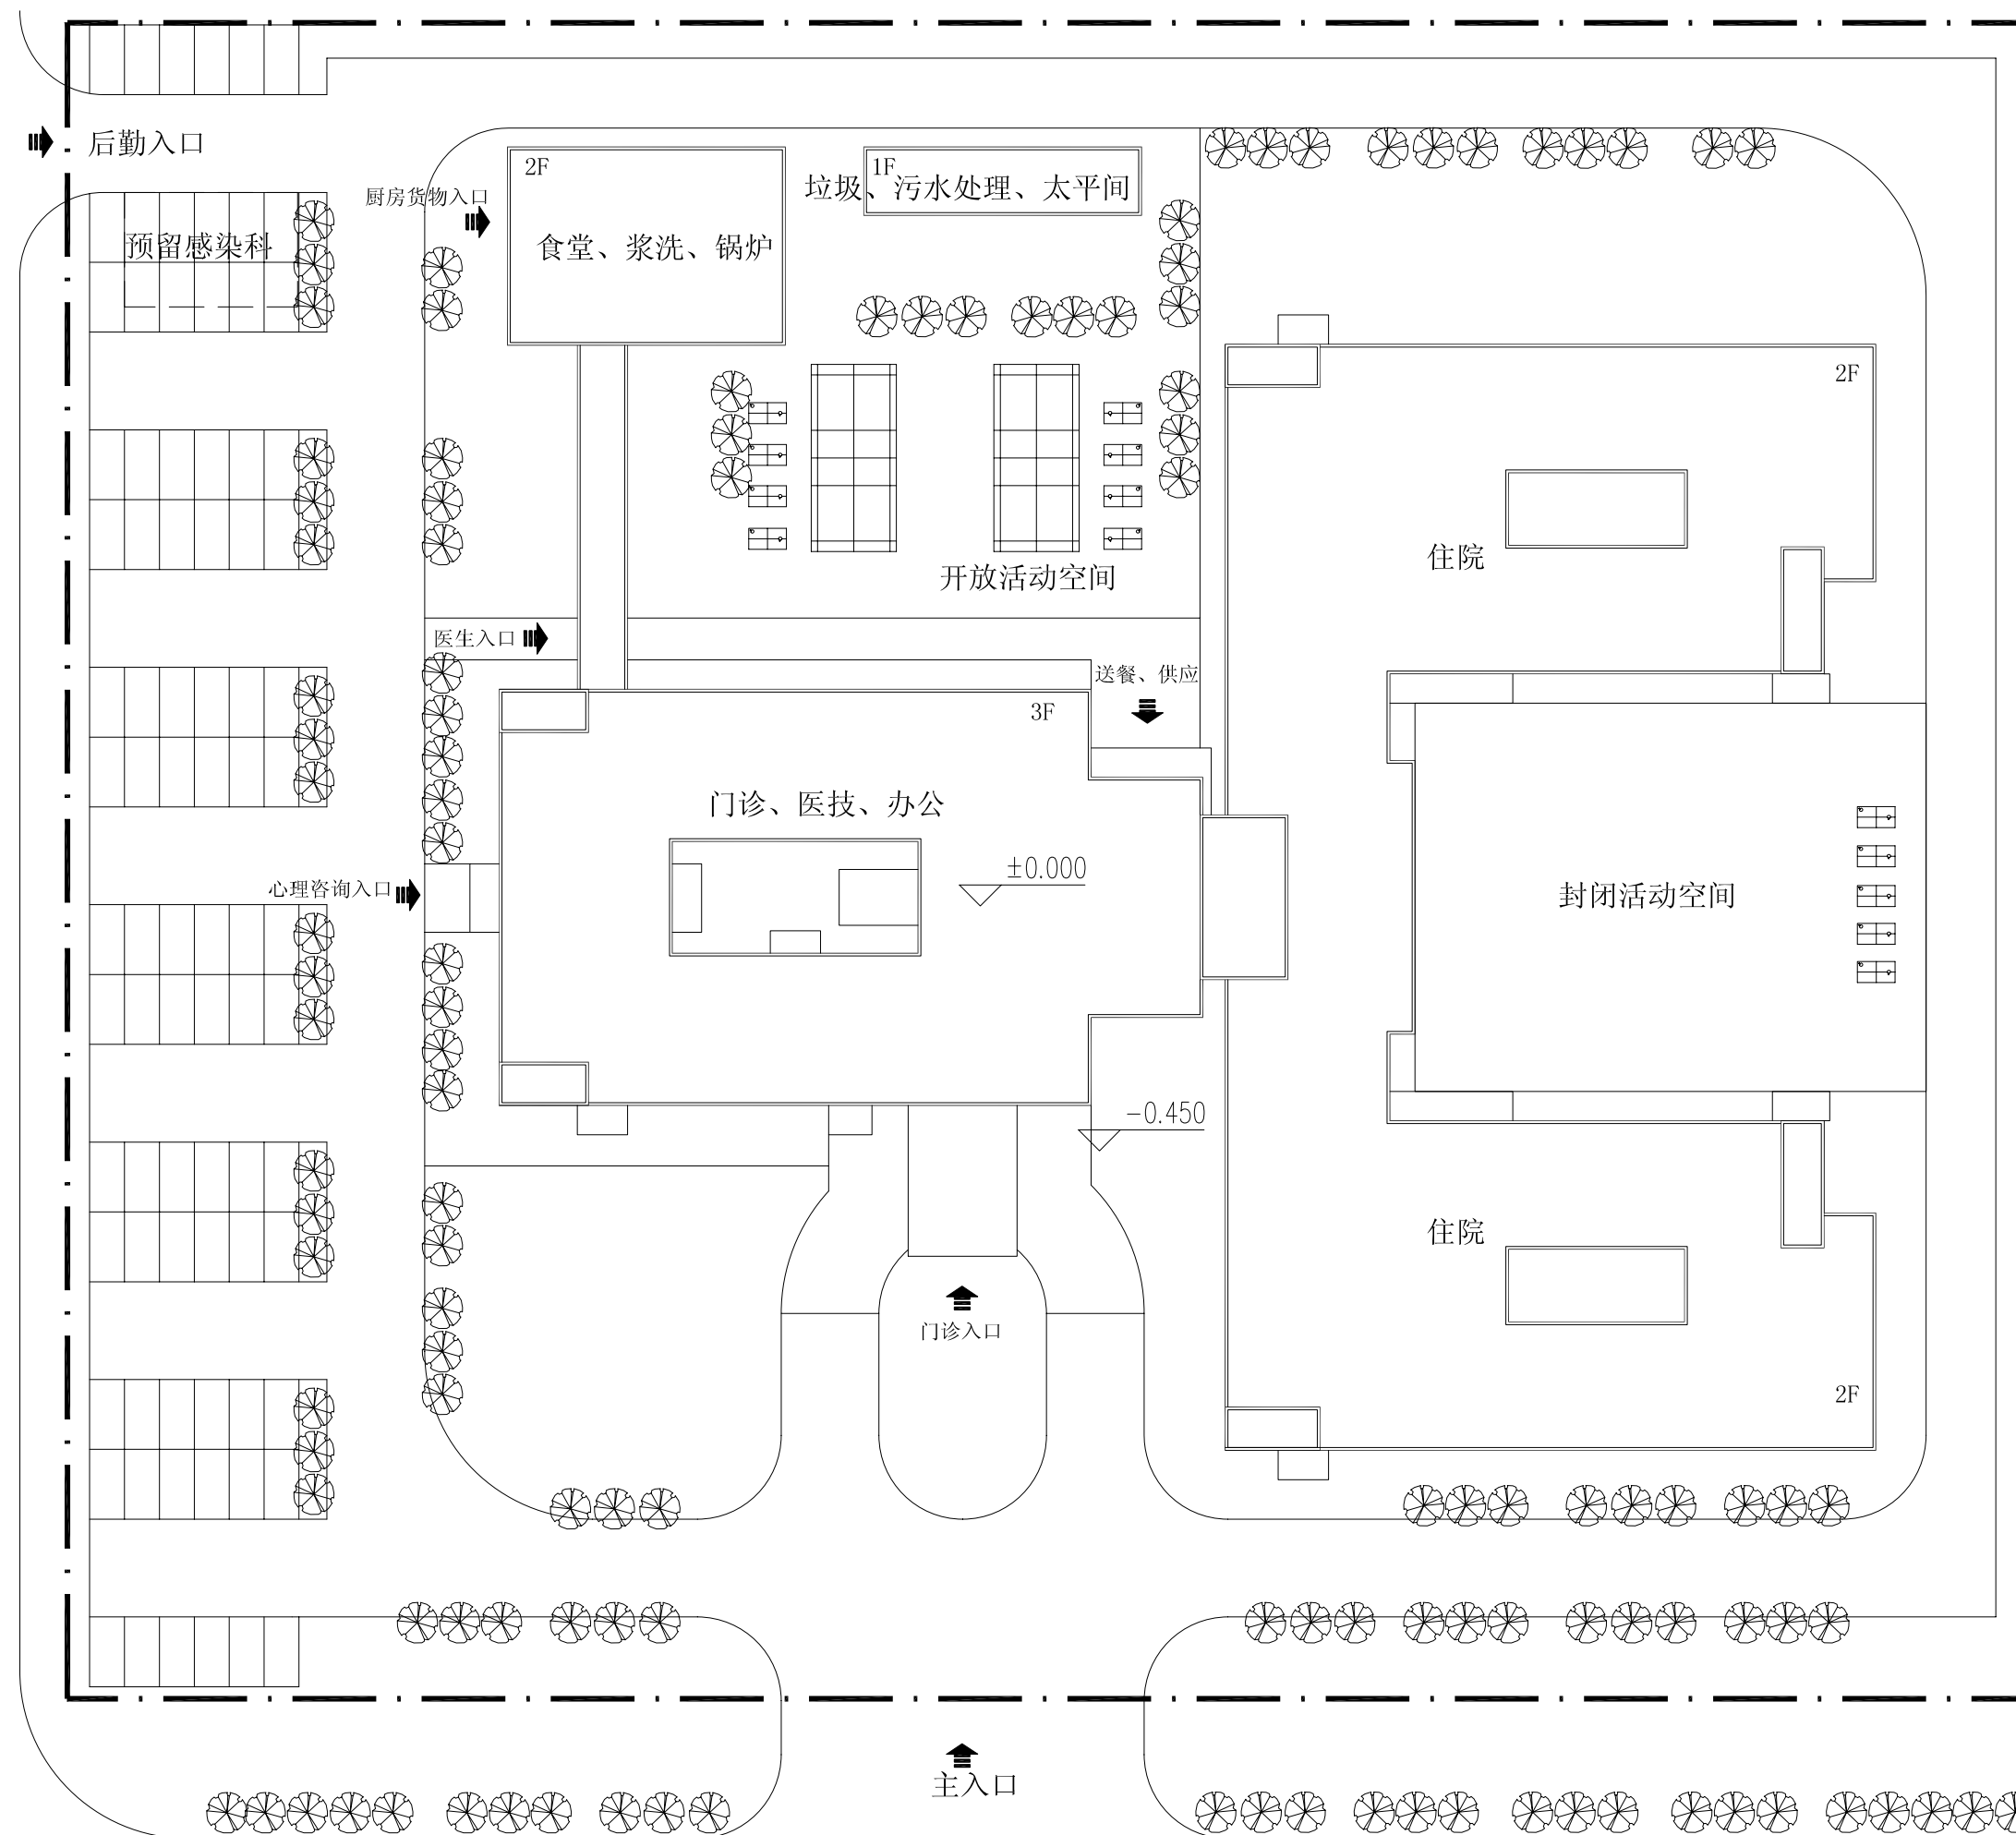


总平面图 1:500

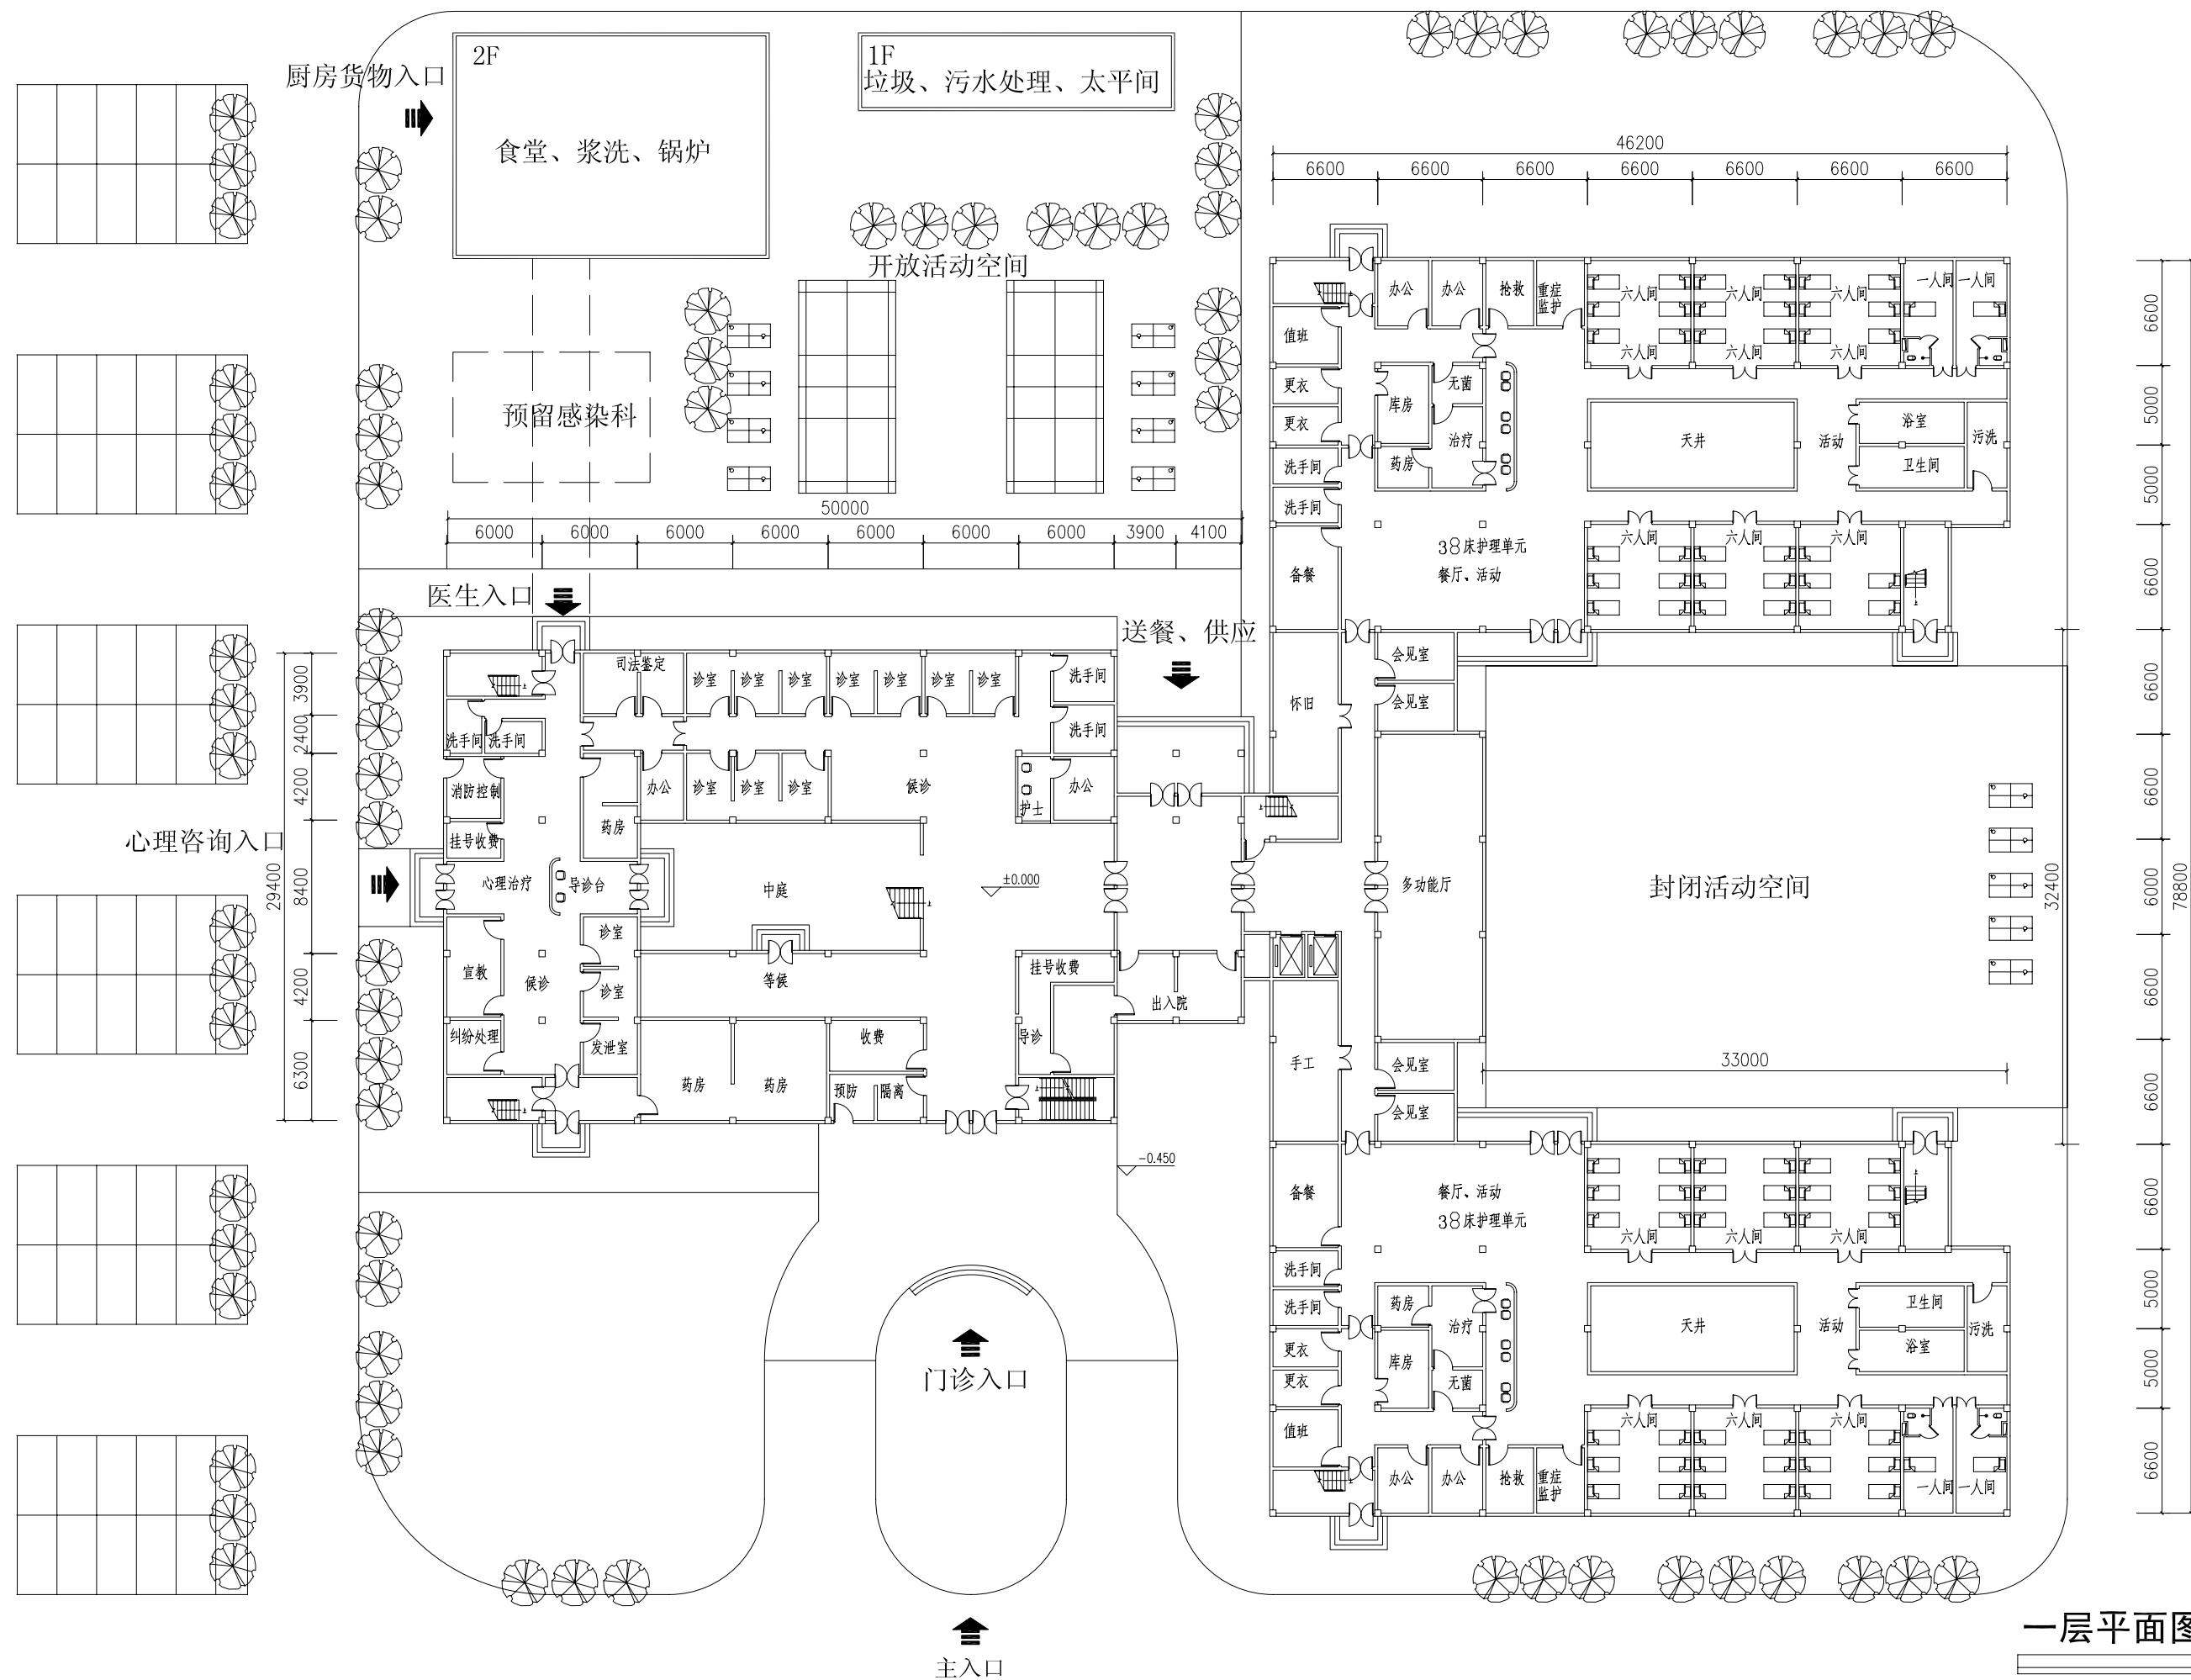


一层平面图 1:400

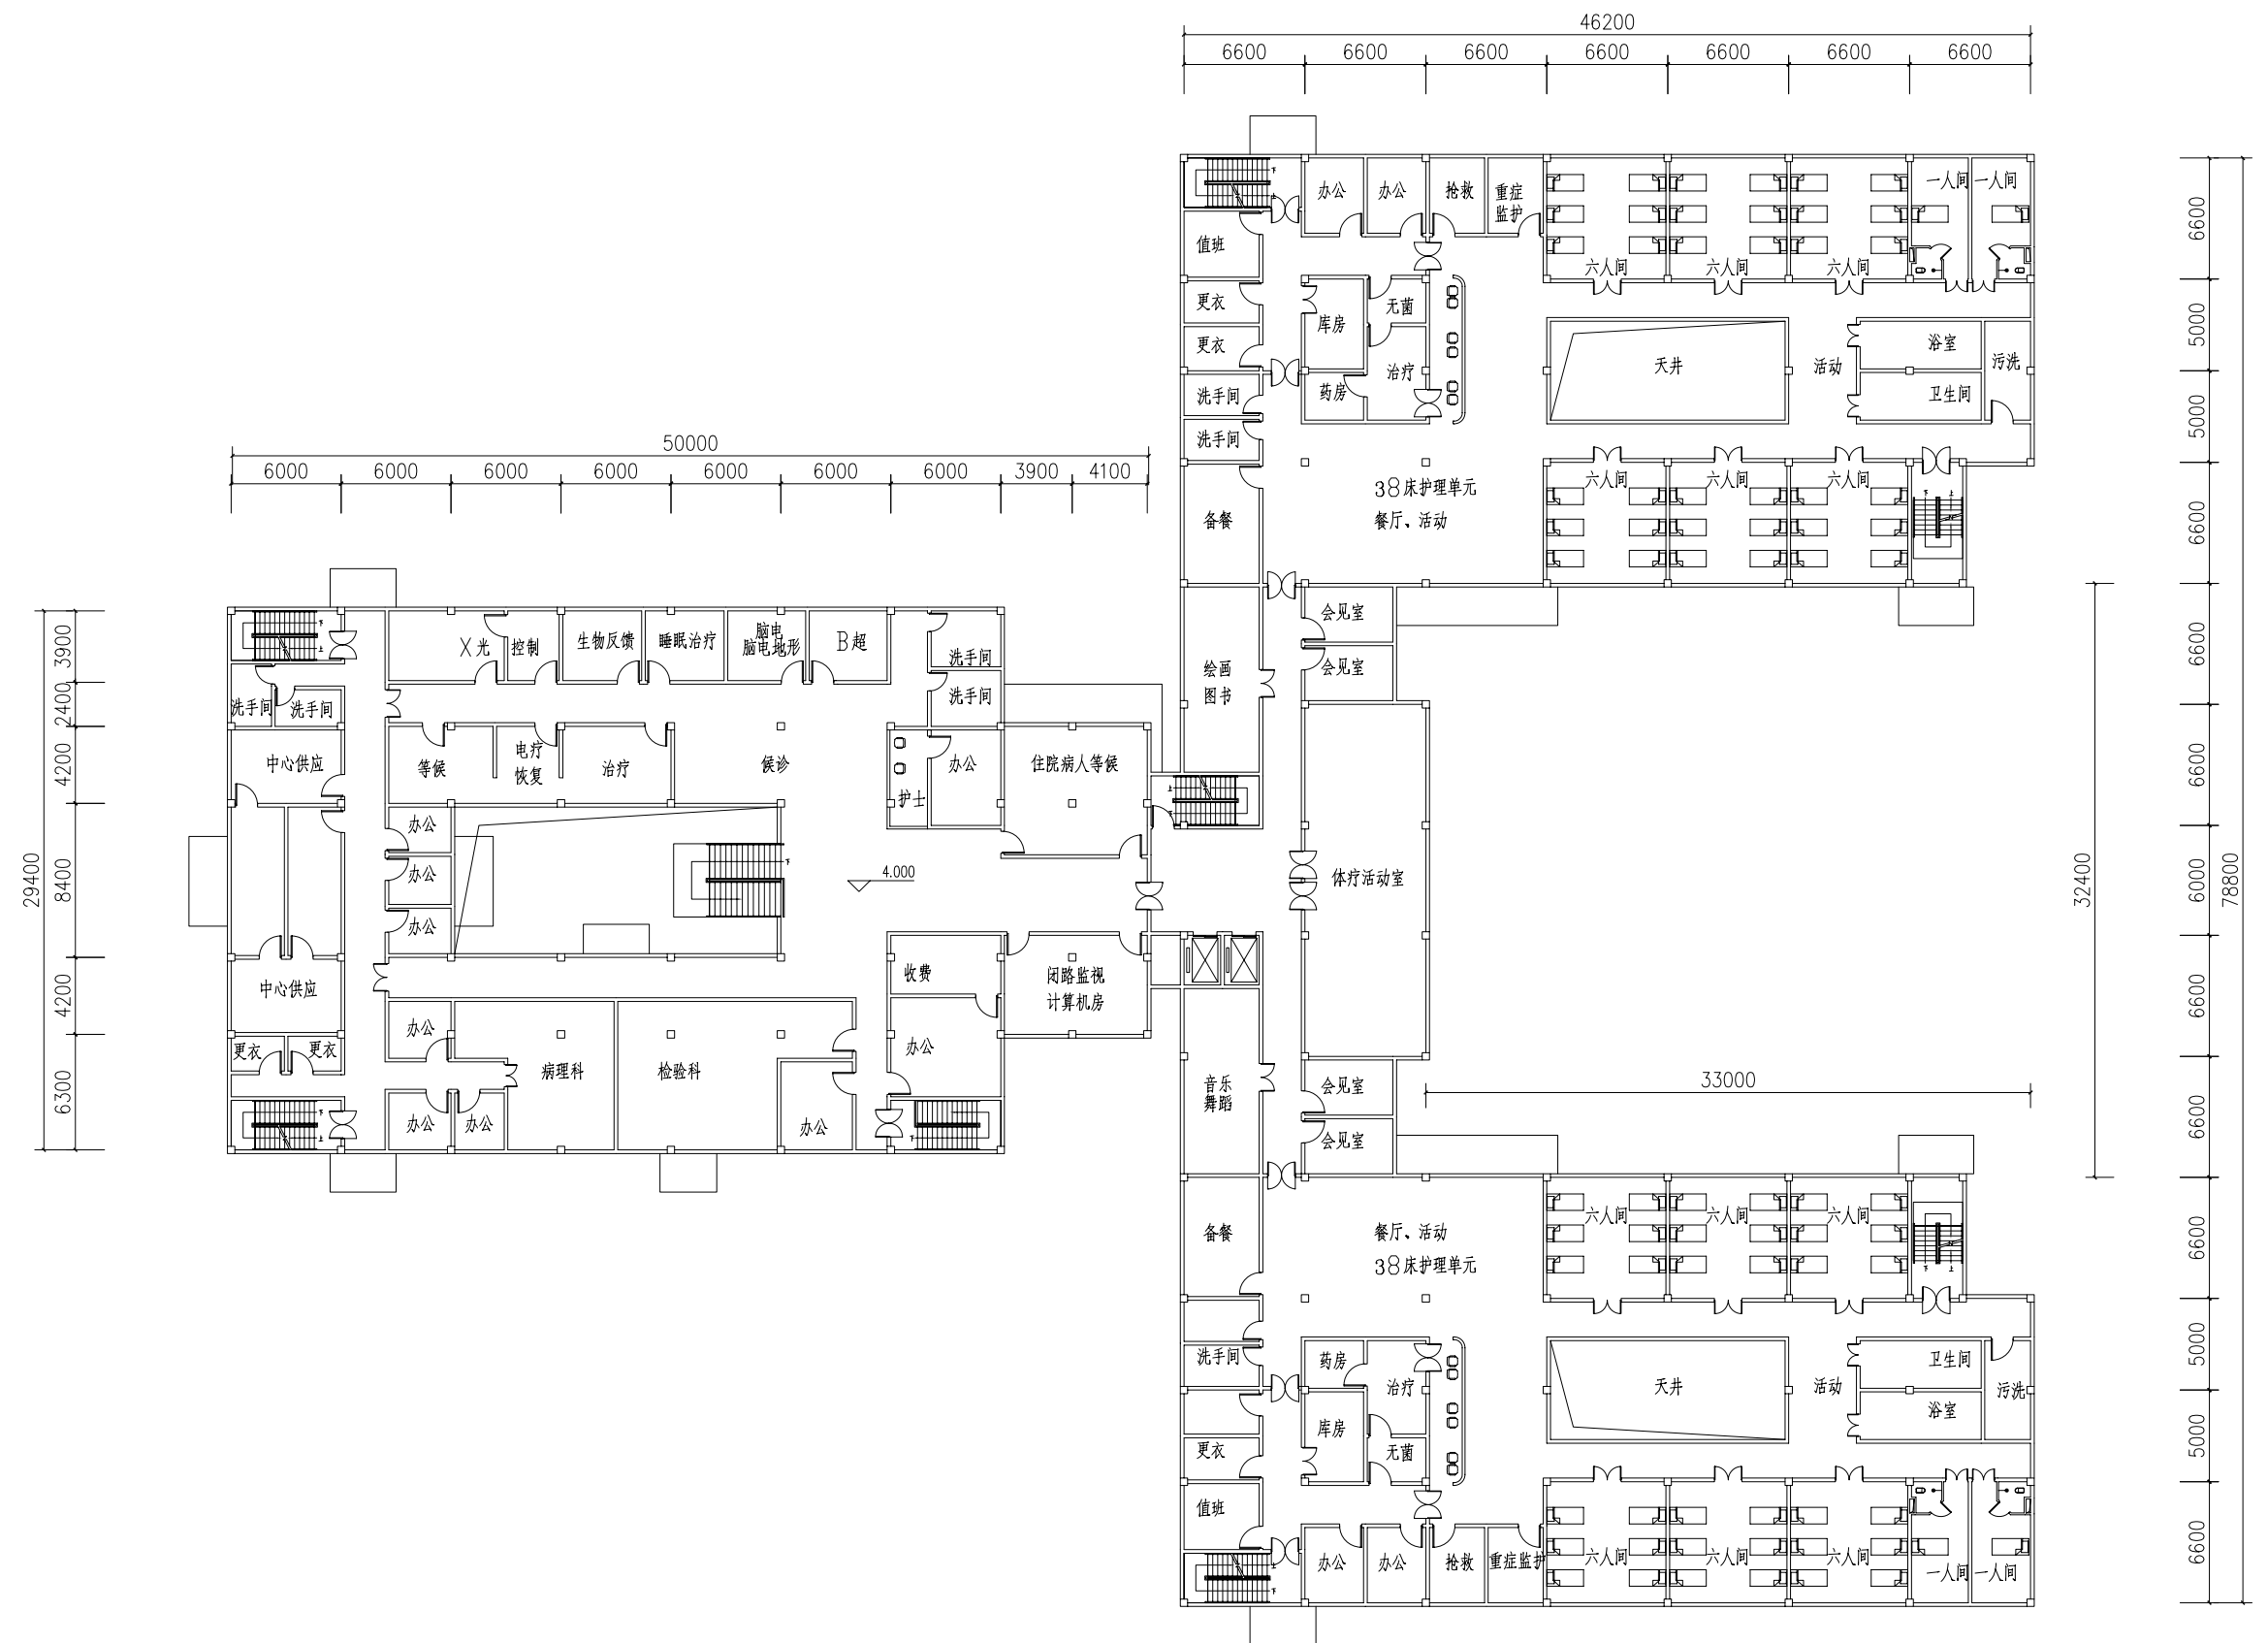


二层平面图 1:400

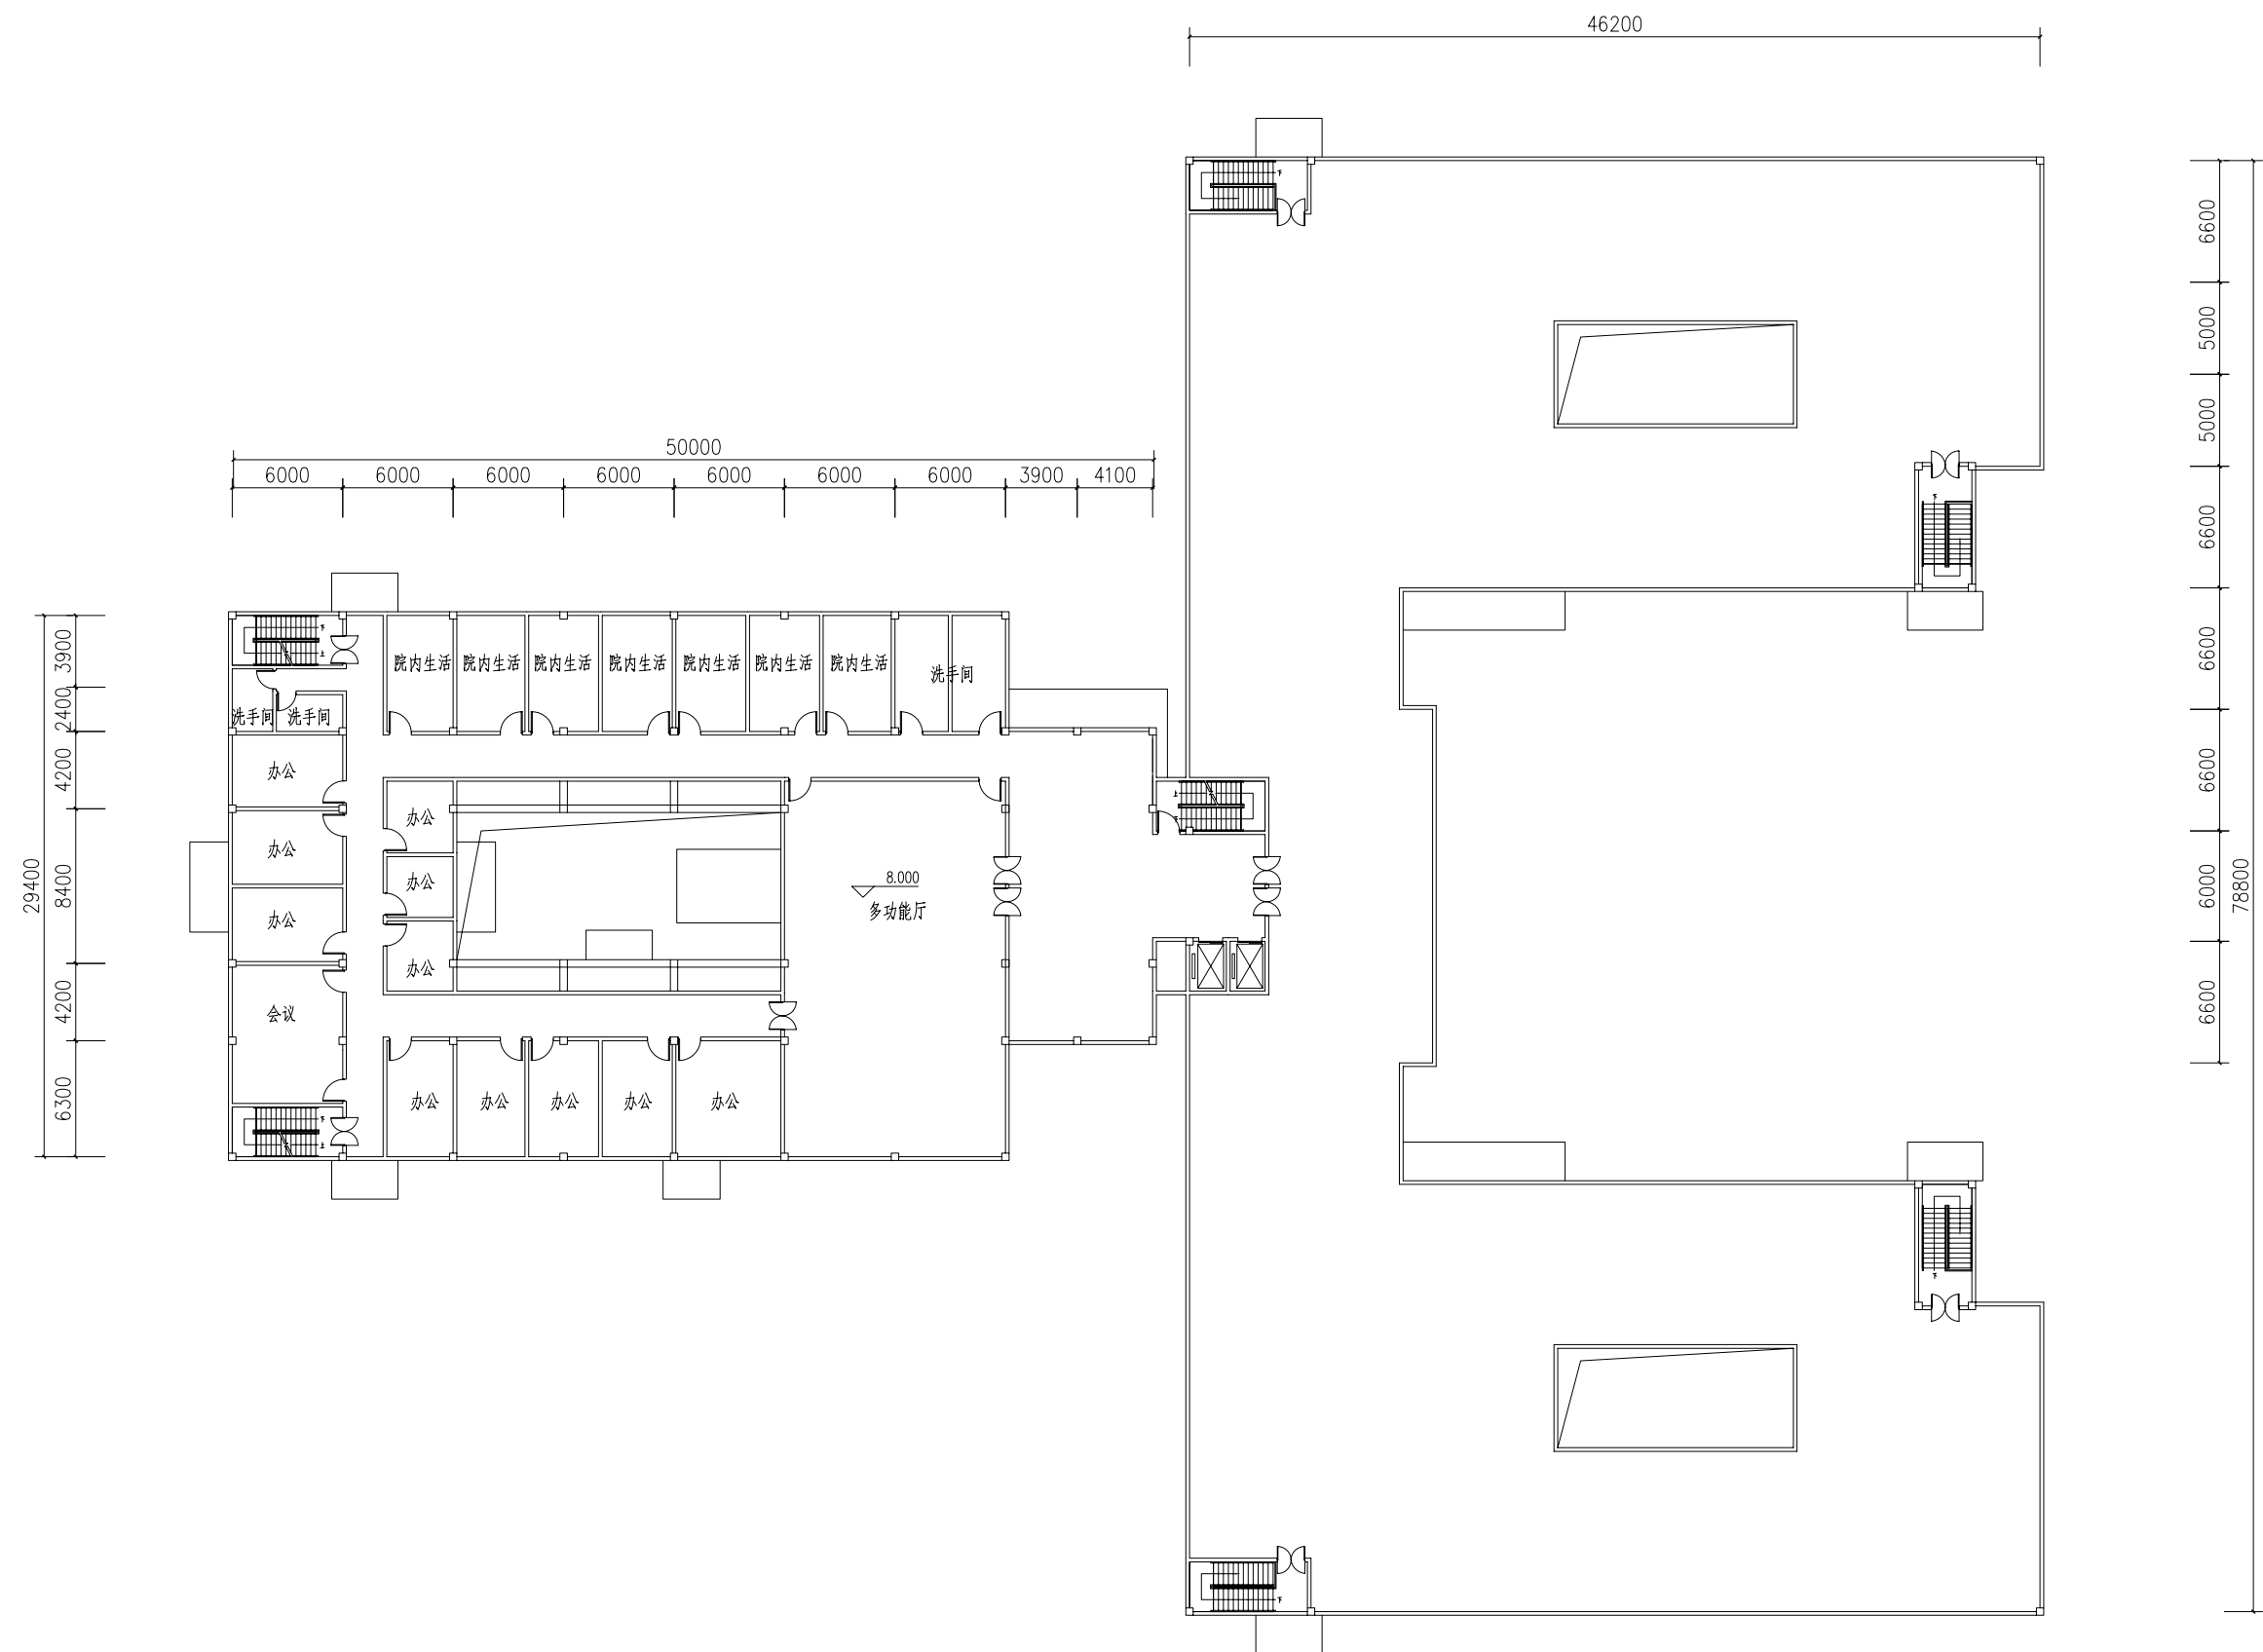


三层平面图 1:400

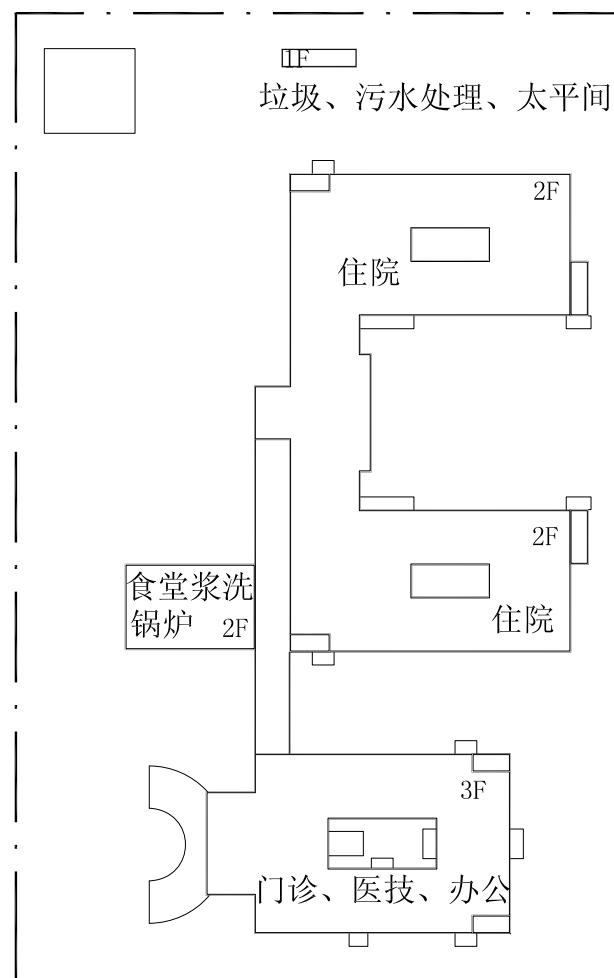


功能组合示意图一

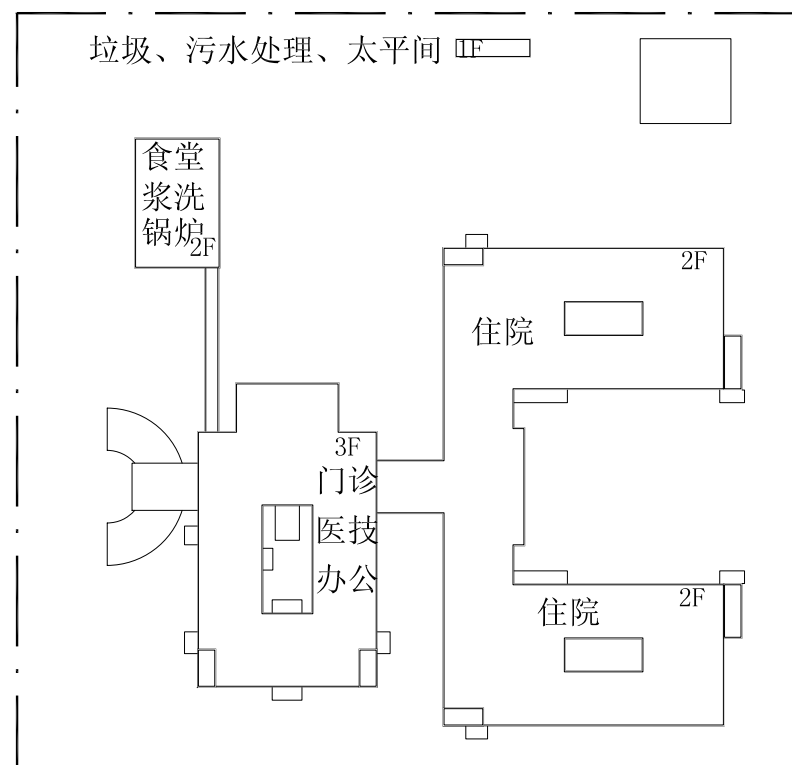


功能组合示意图二

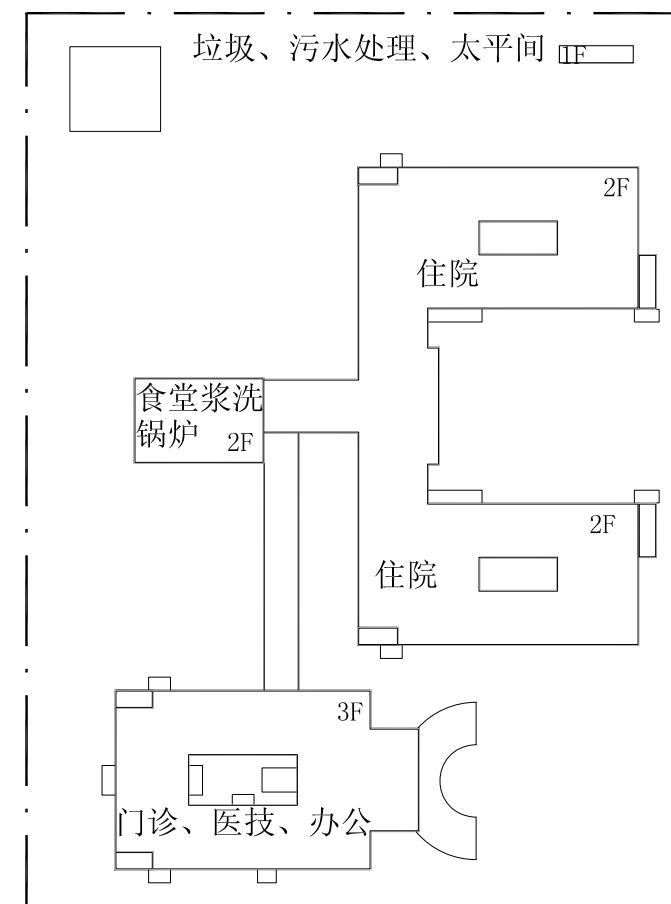

功能组合示意图三

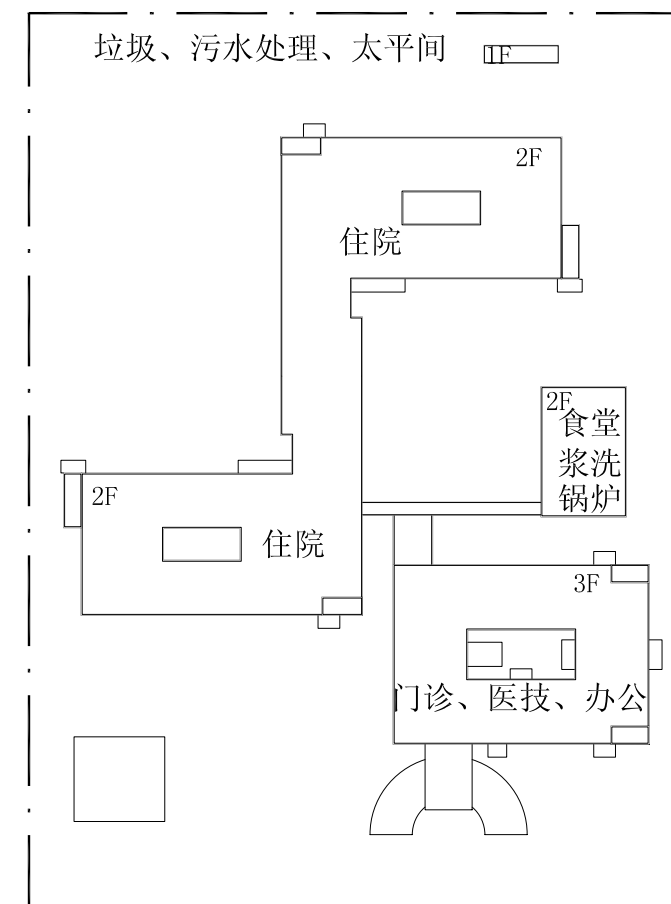


功能组合示意图四

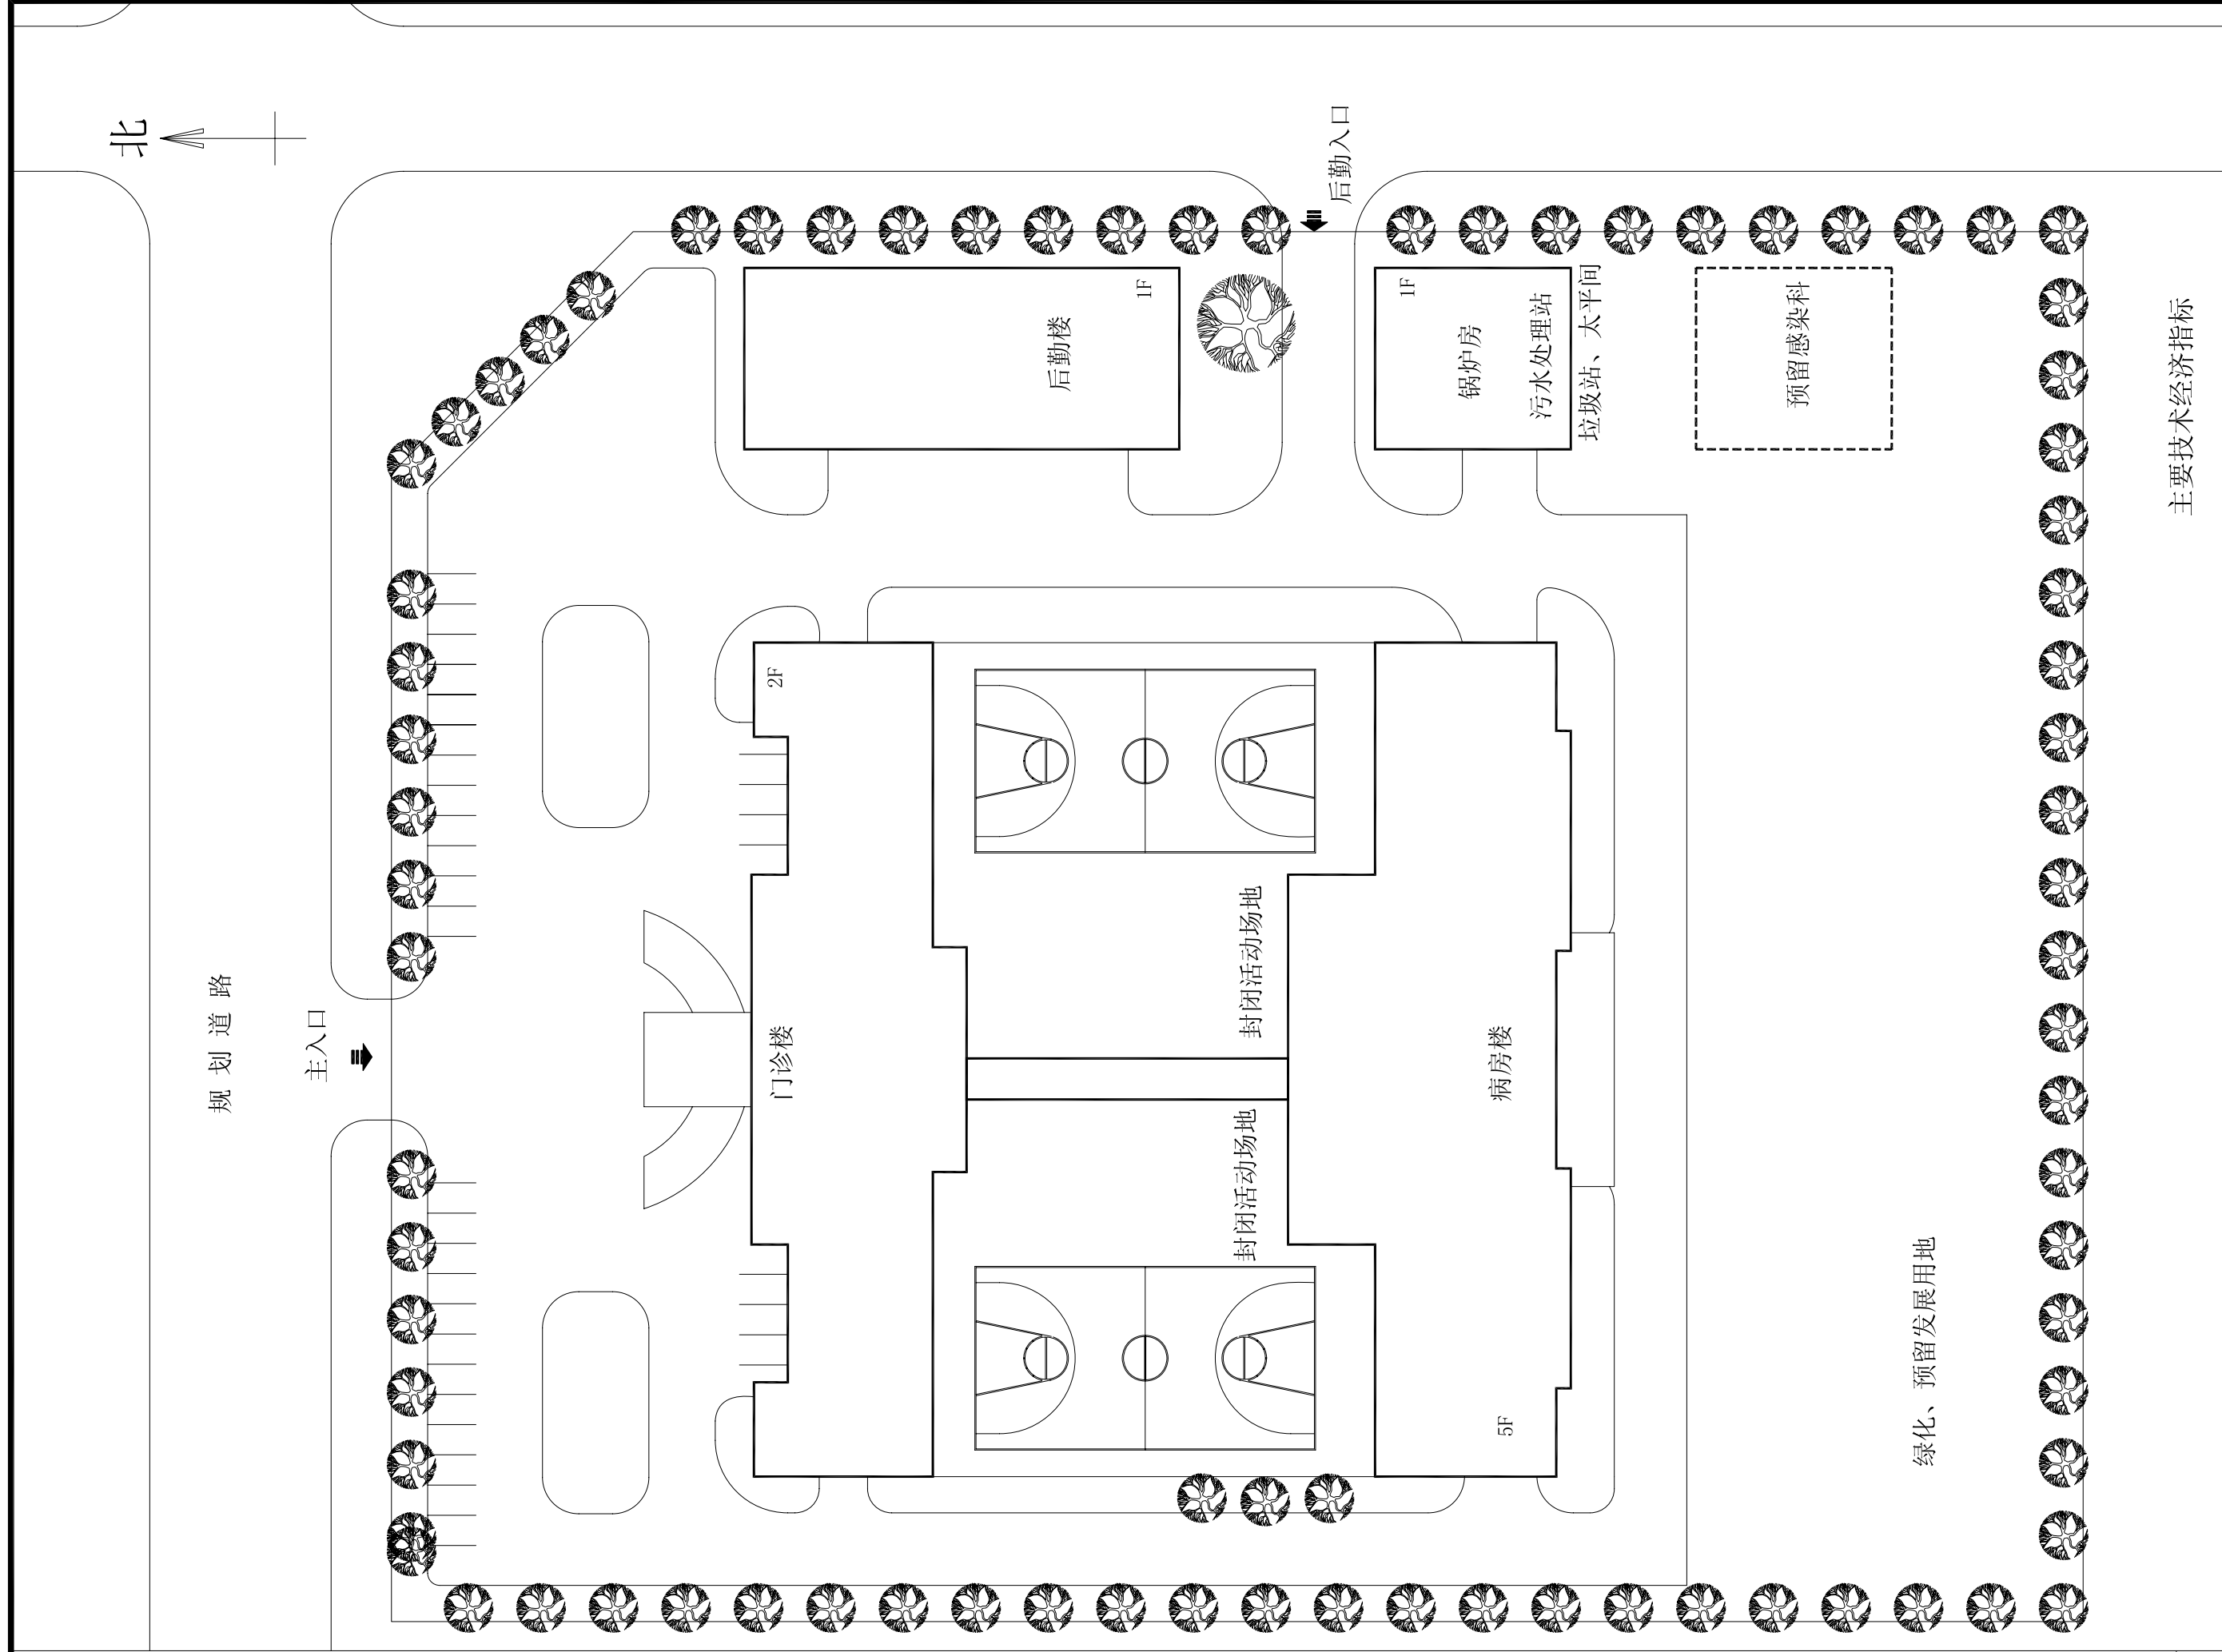


主要技术经济指标

用地面积	15900m ²
总建筑面积	8970m ²
床位数	160 张
床均面积:	56.06m ² /床


总平面图 1:500

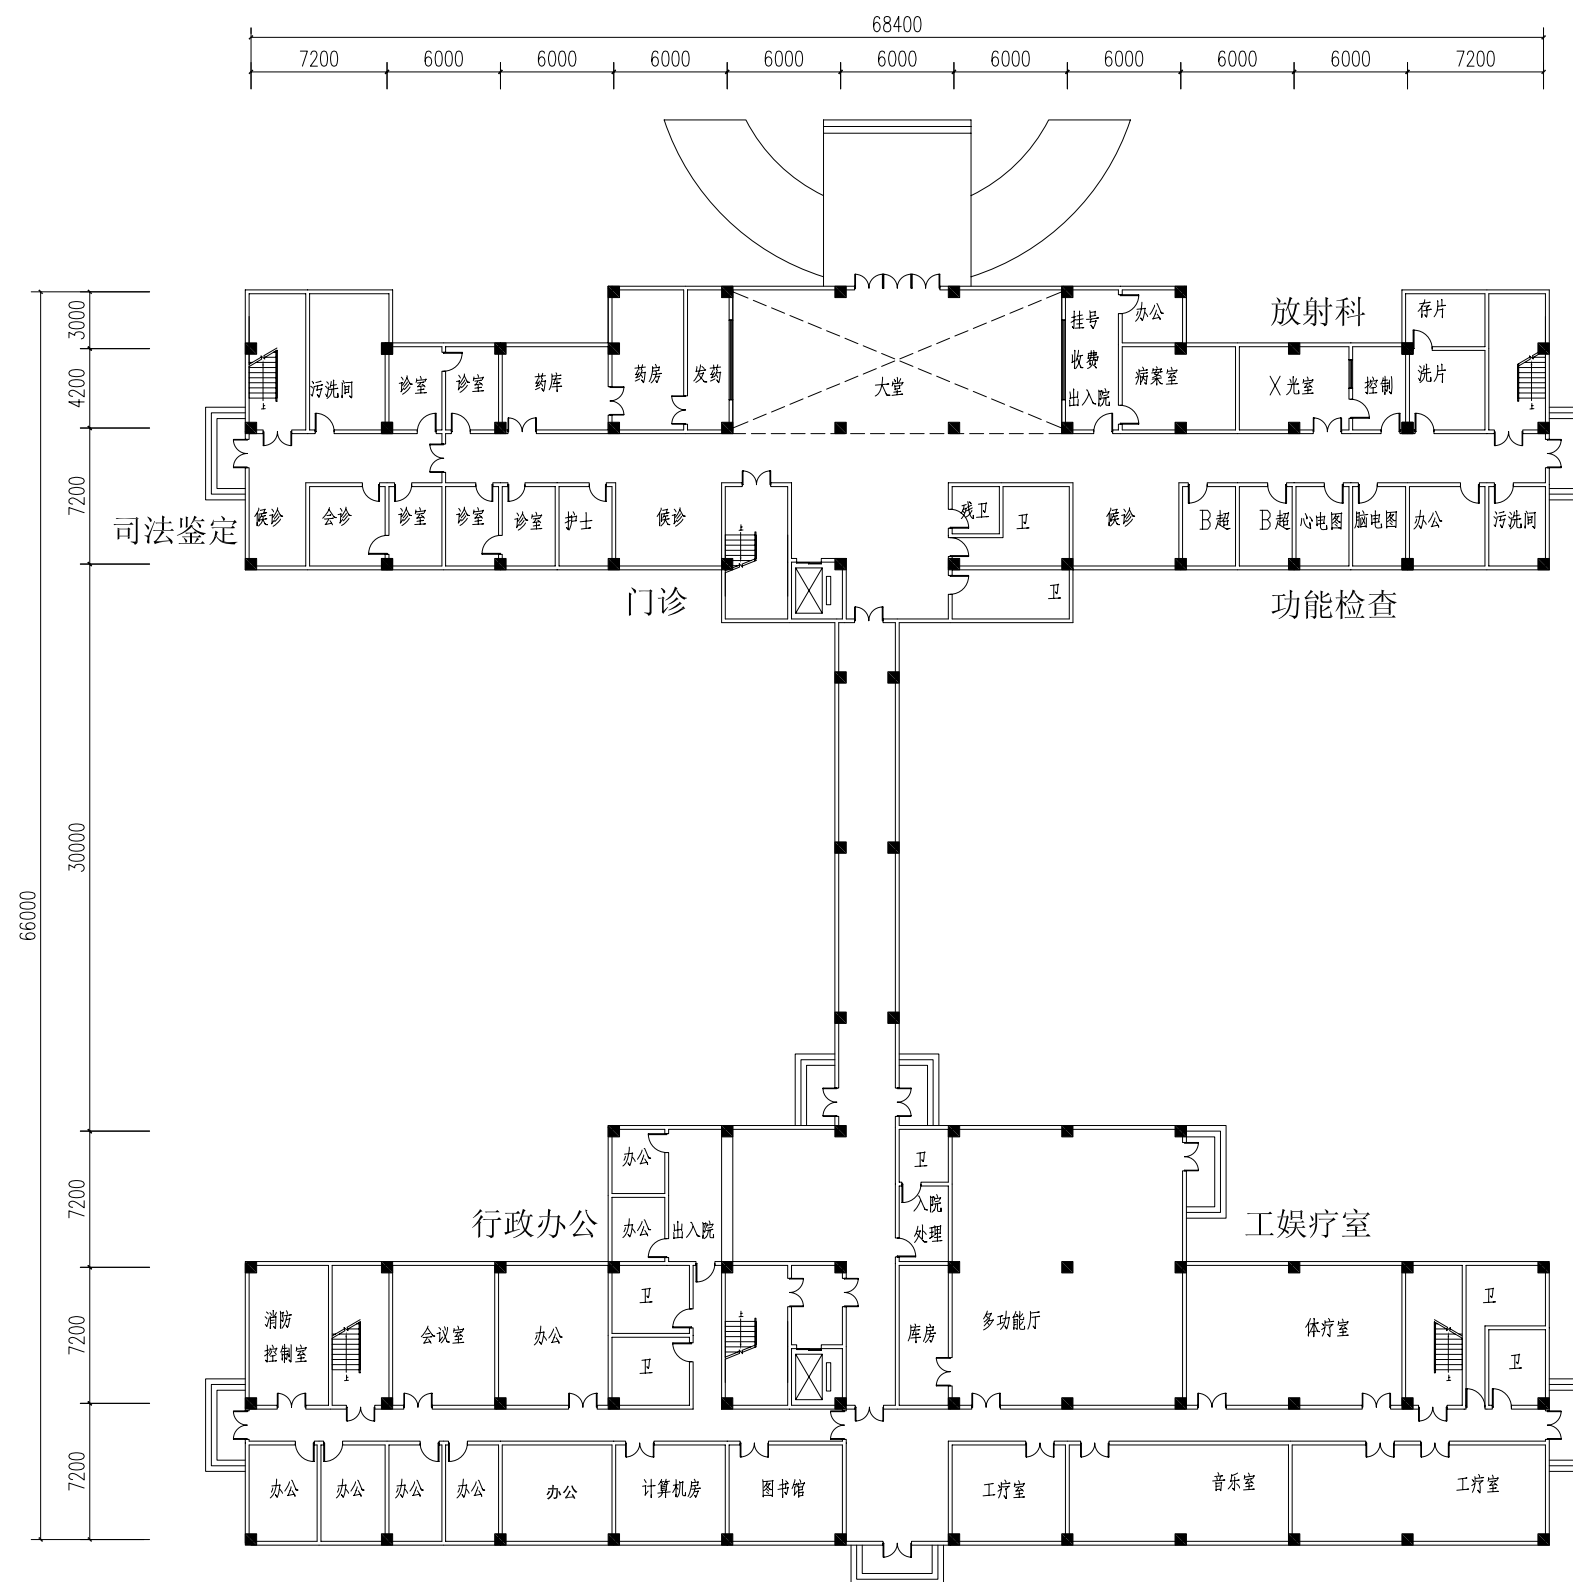

一层平面图 1:400

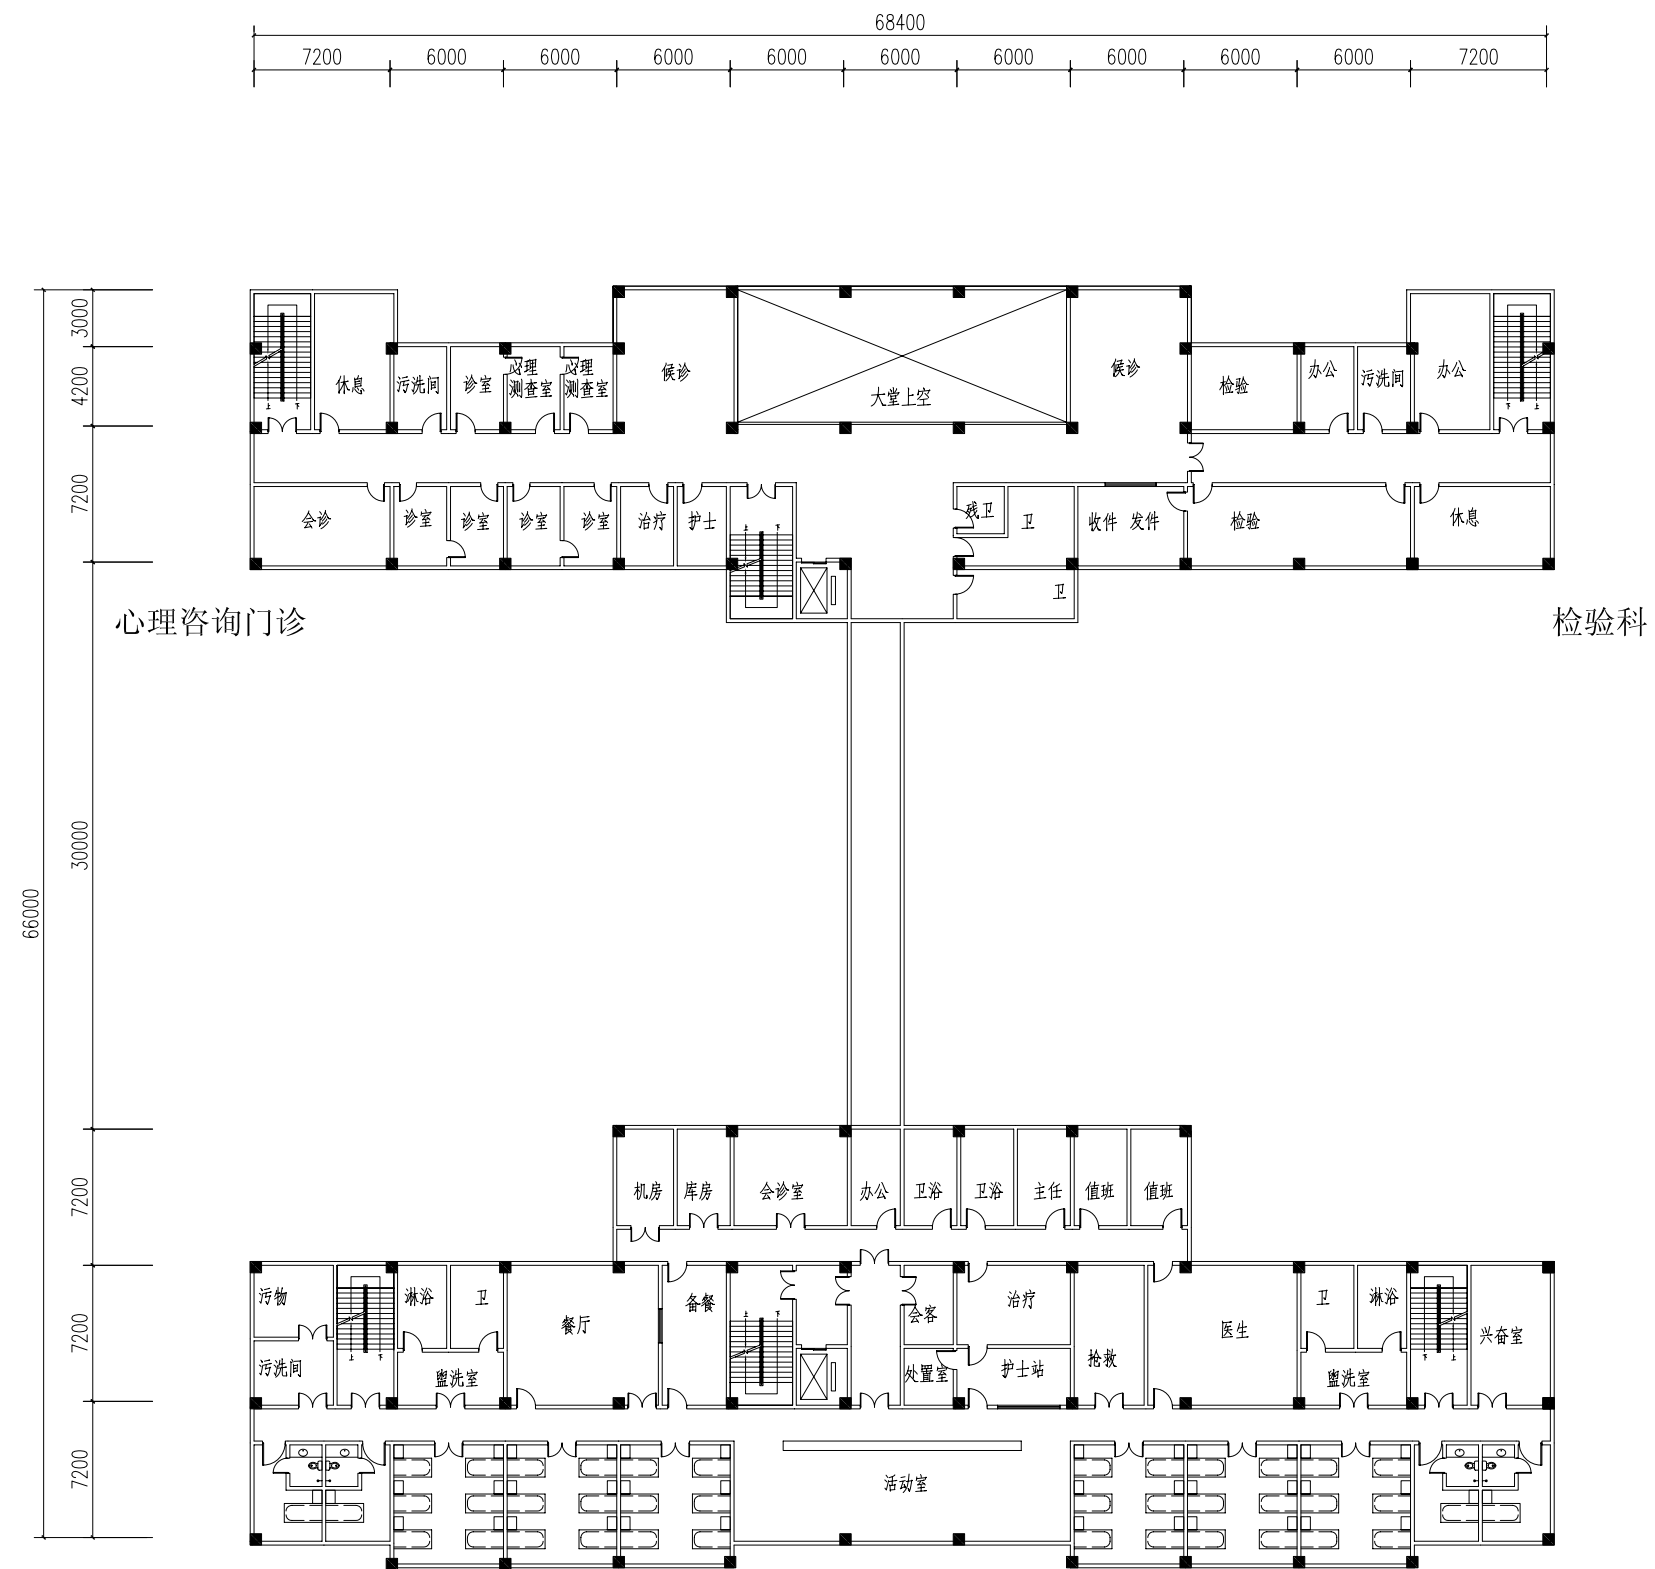

二层平面图 1:400

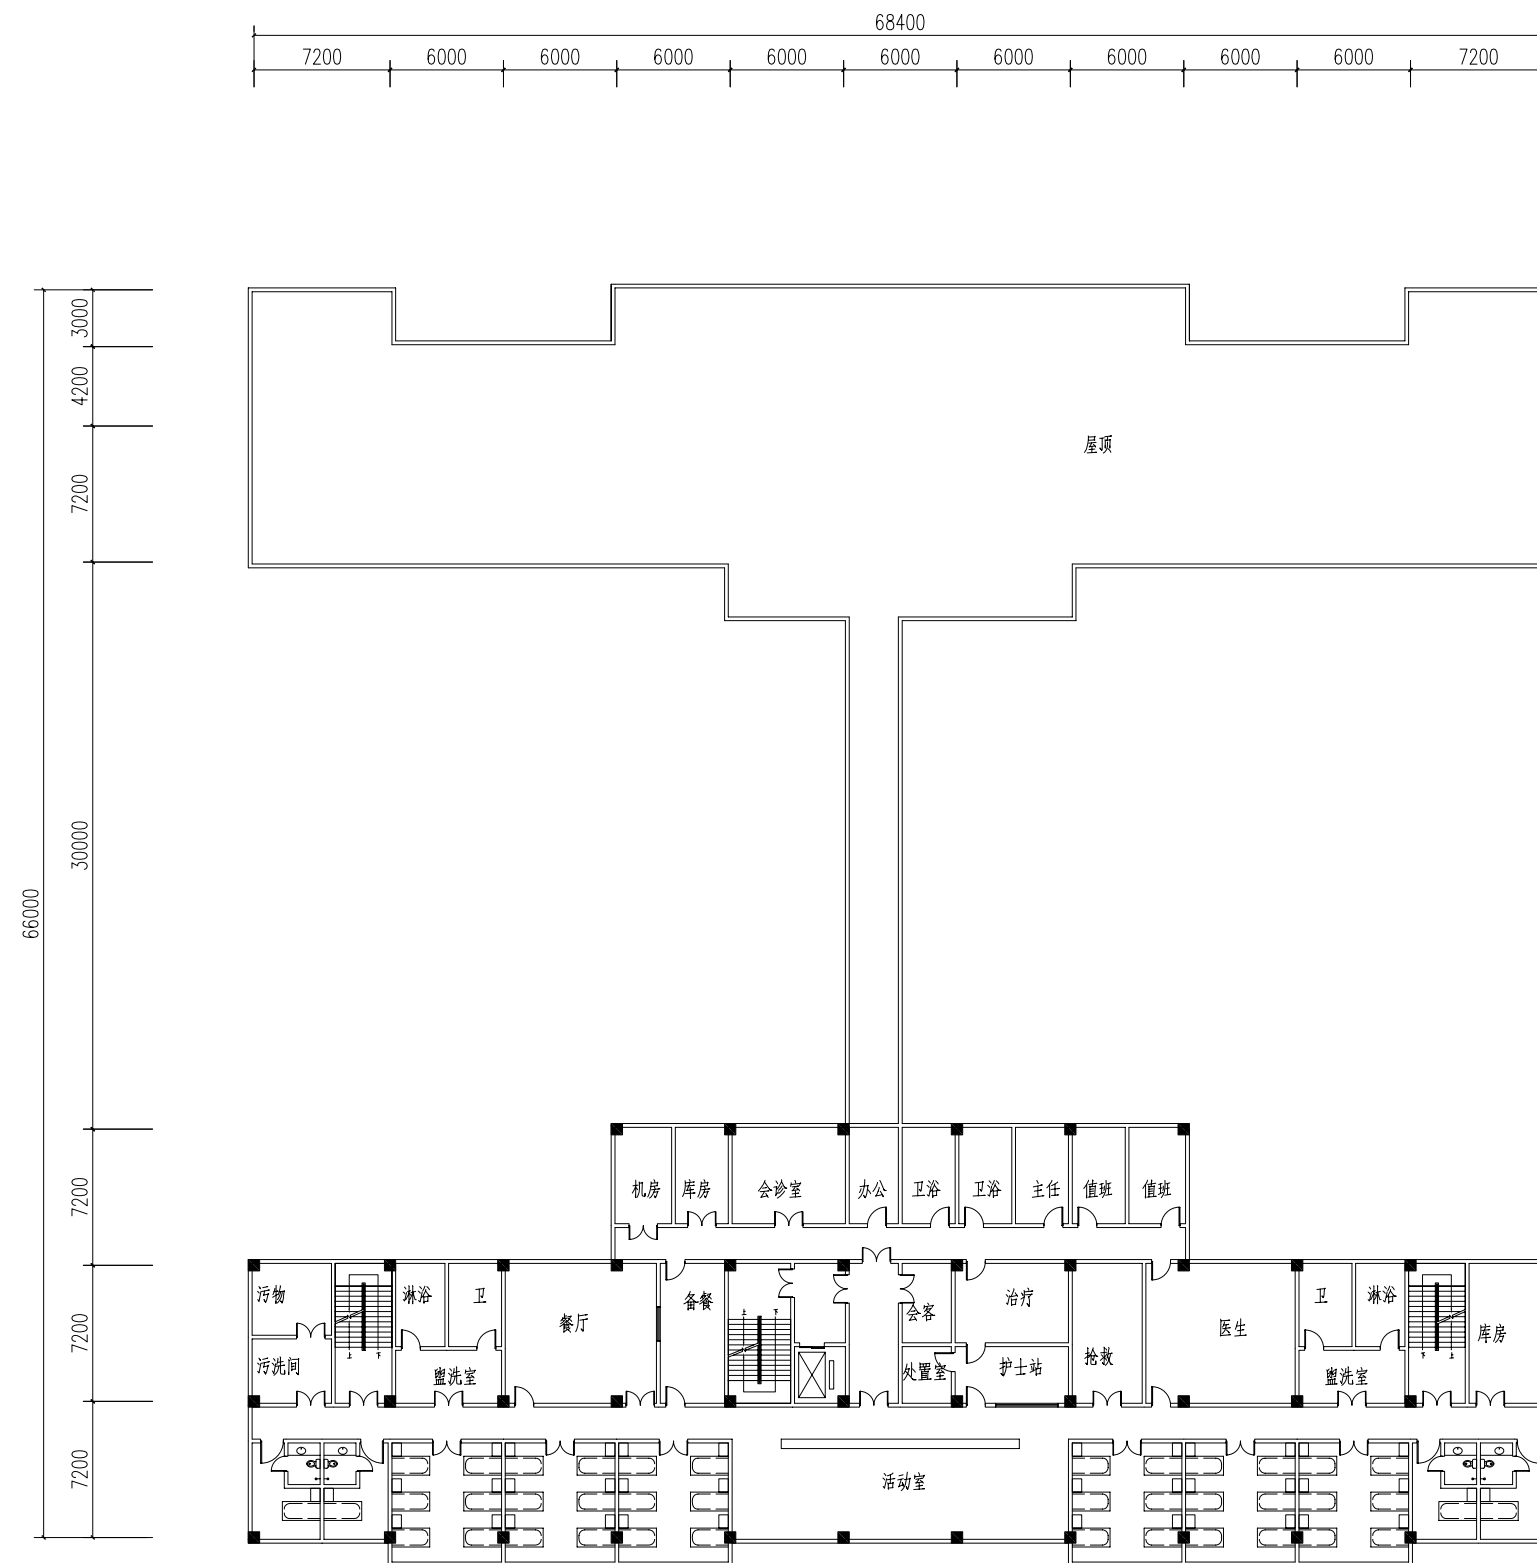


三-五层平面图 1:400




用地面积	32206m ²
总建筑面积	17121m ²
床位数	317 张
床均面积：	54 m ² /床




--

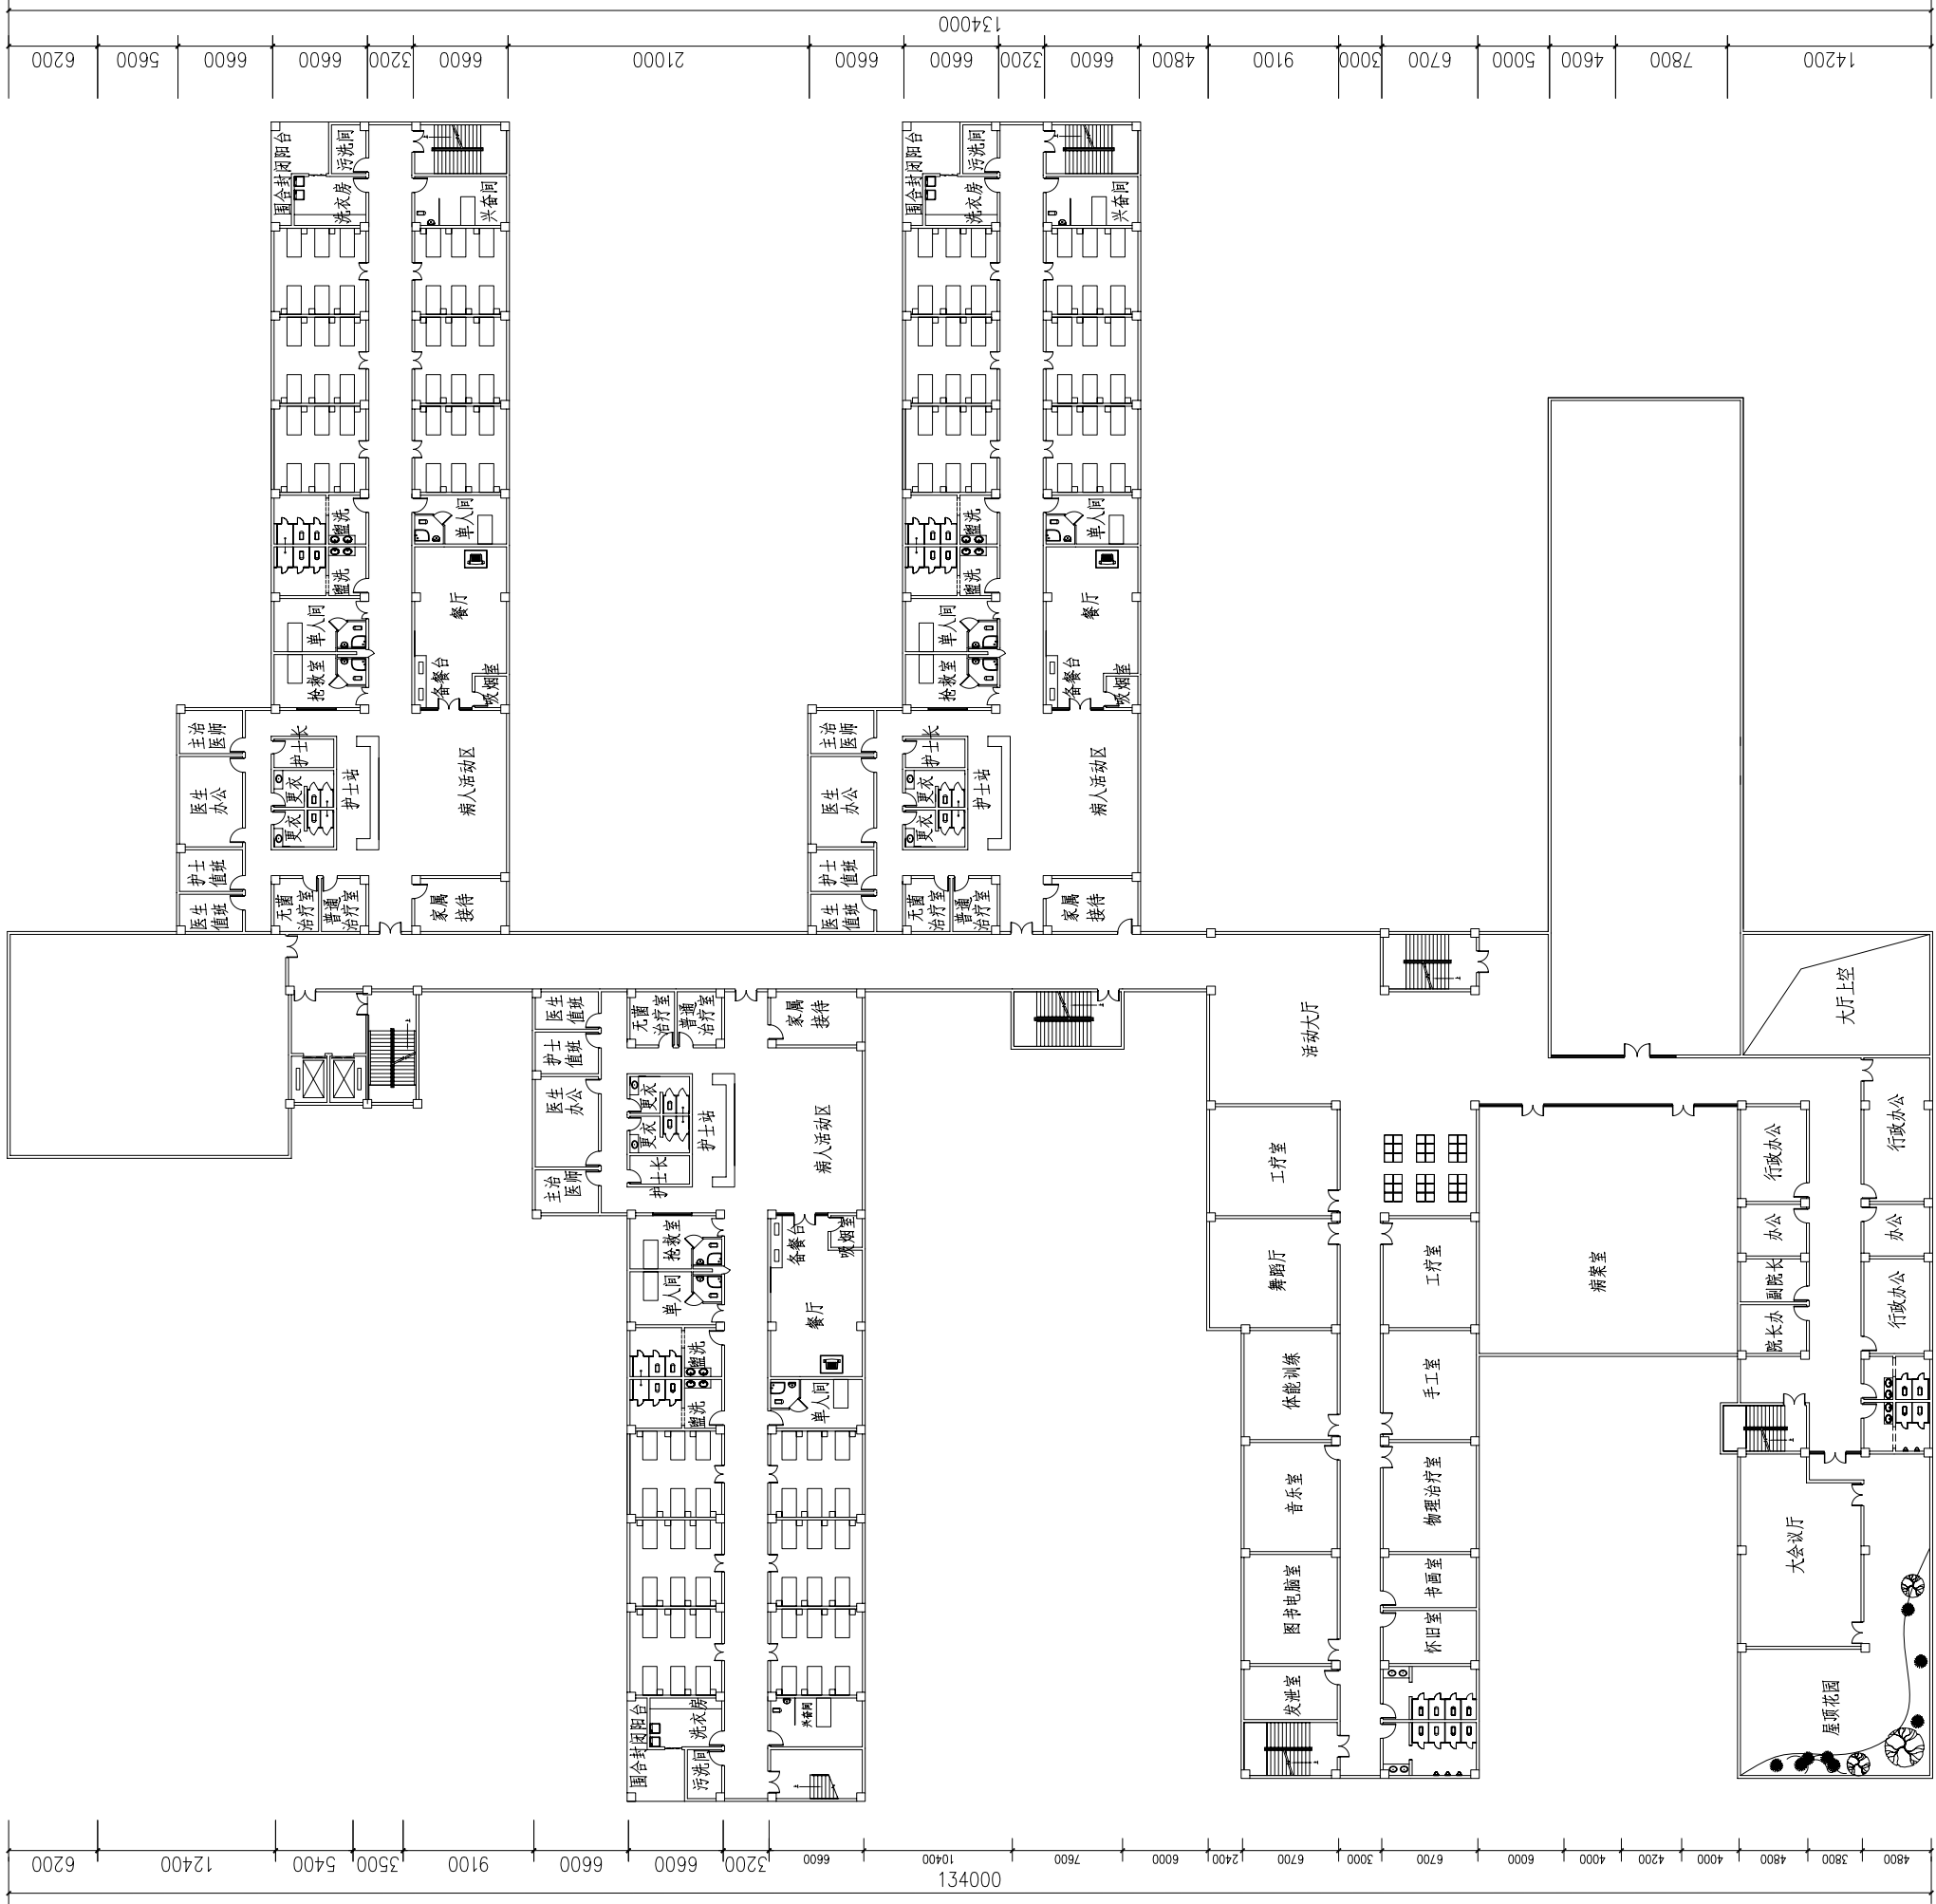

二层平面图 1:500

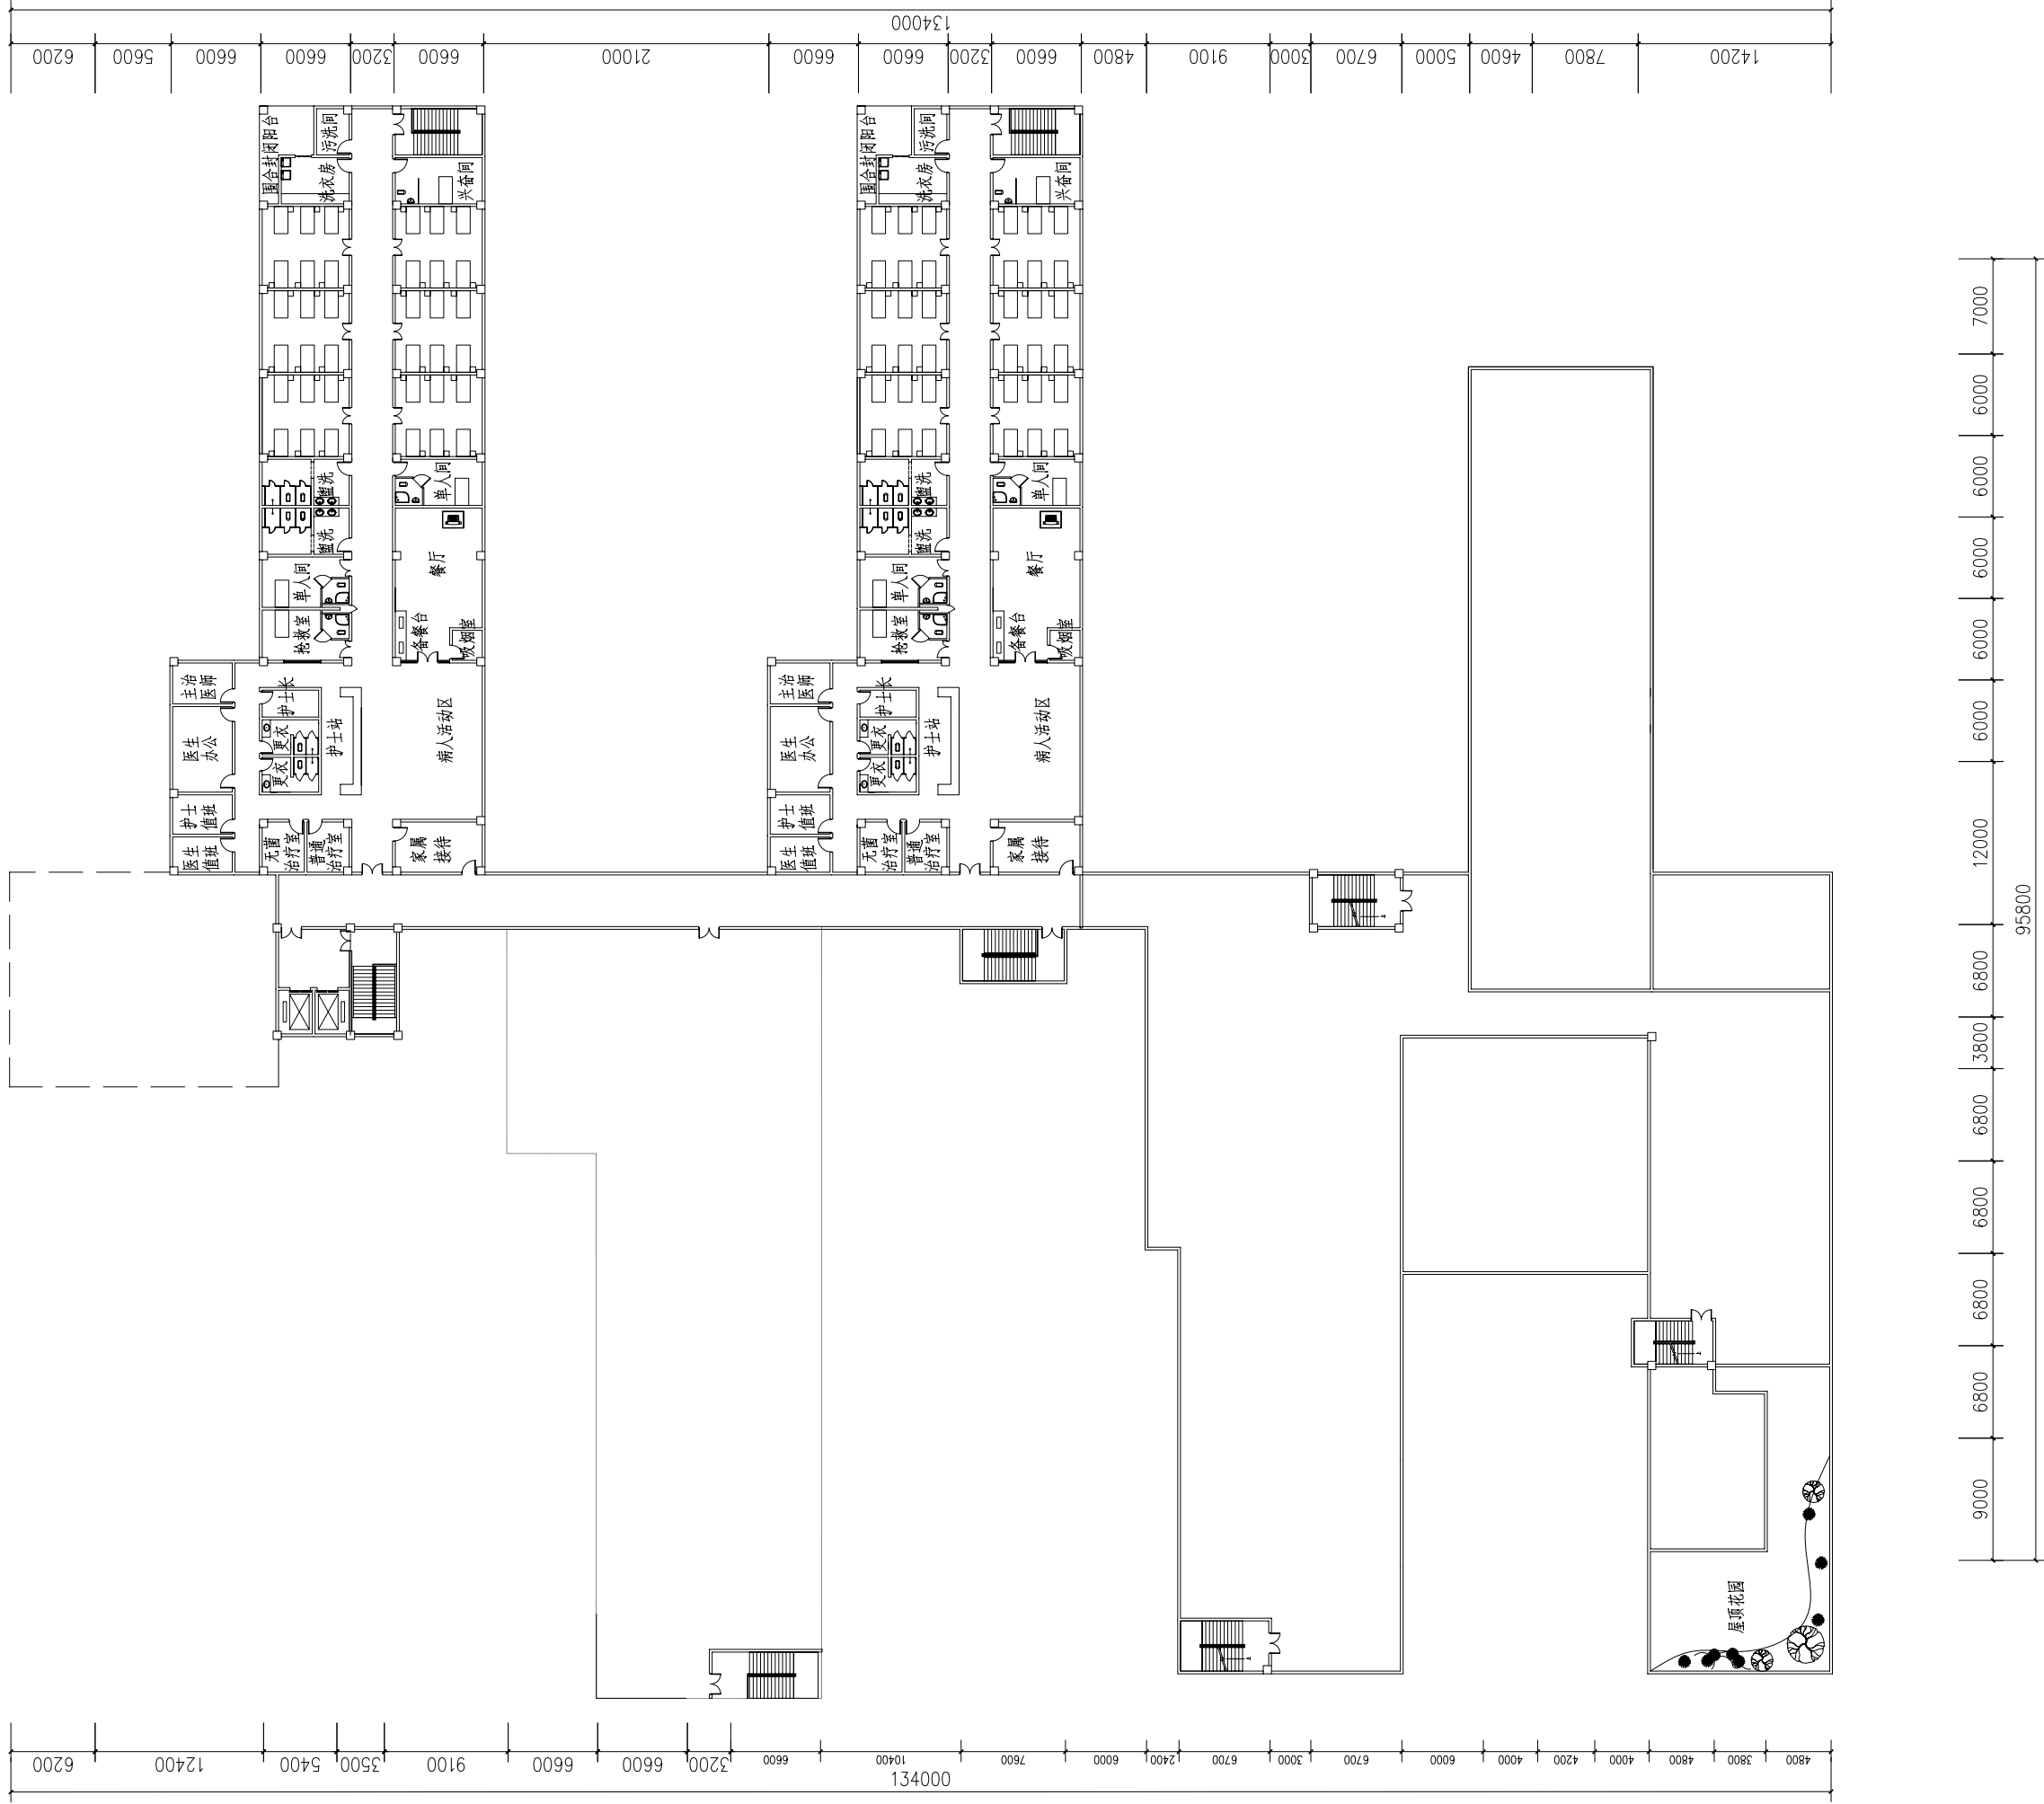


三层平面图 1:500

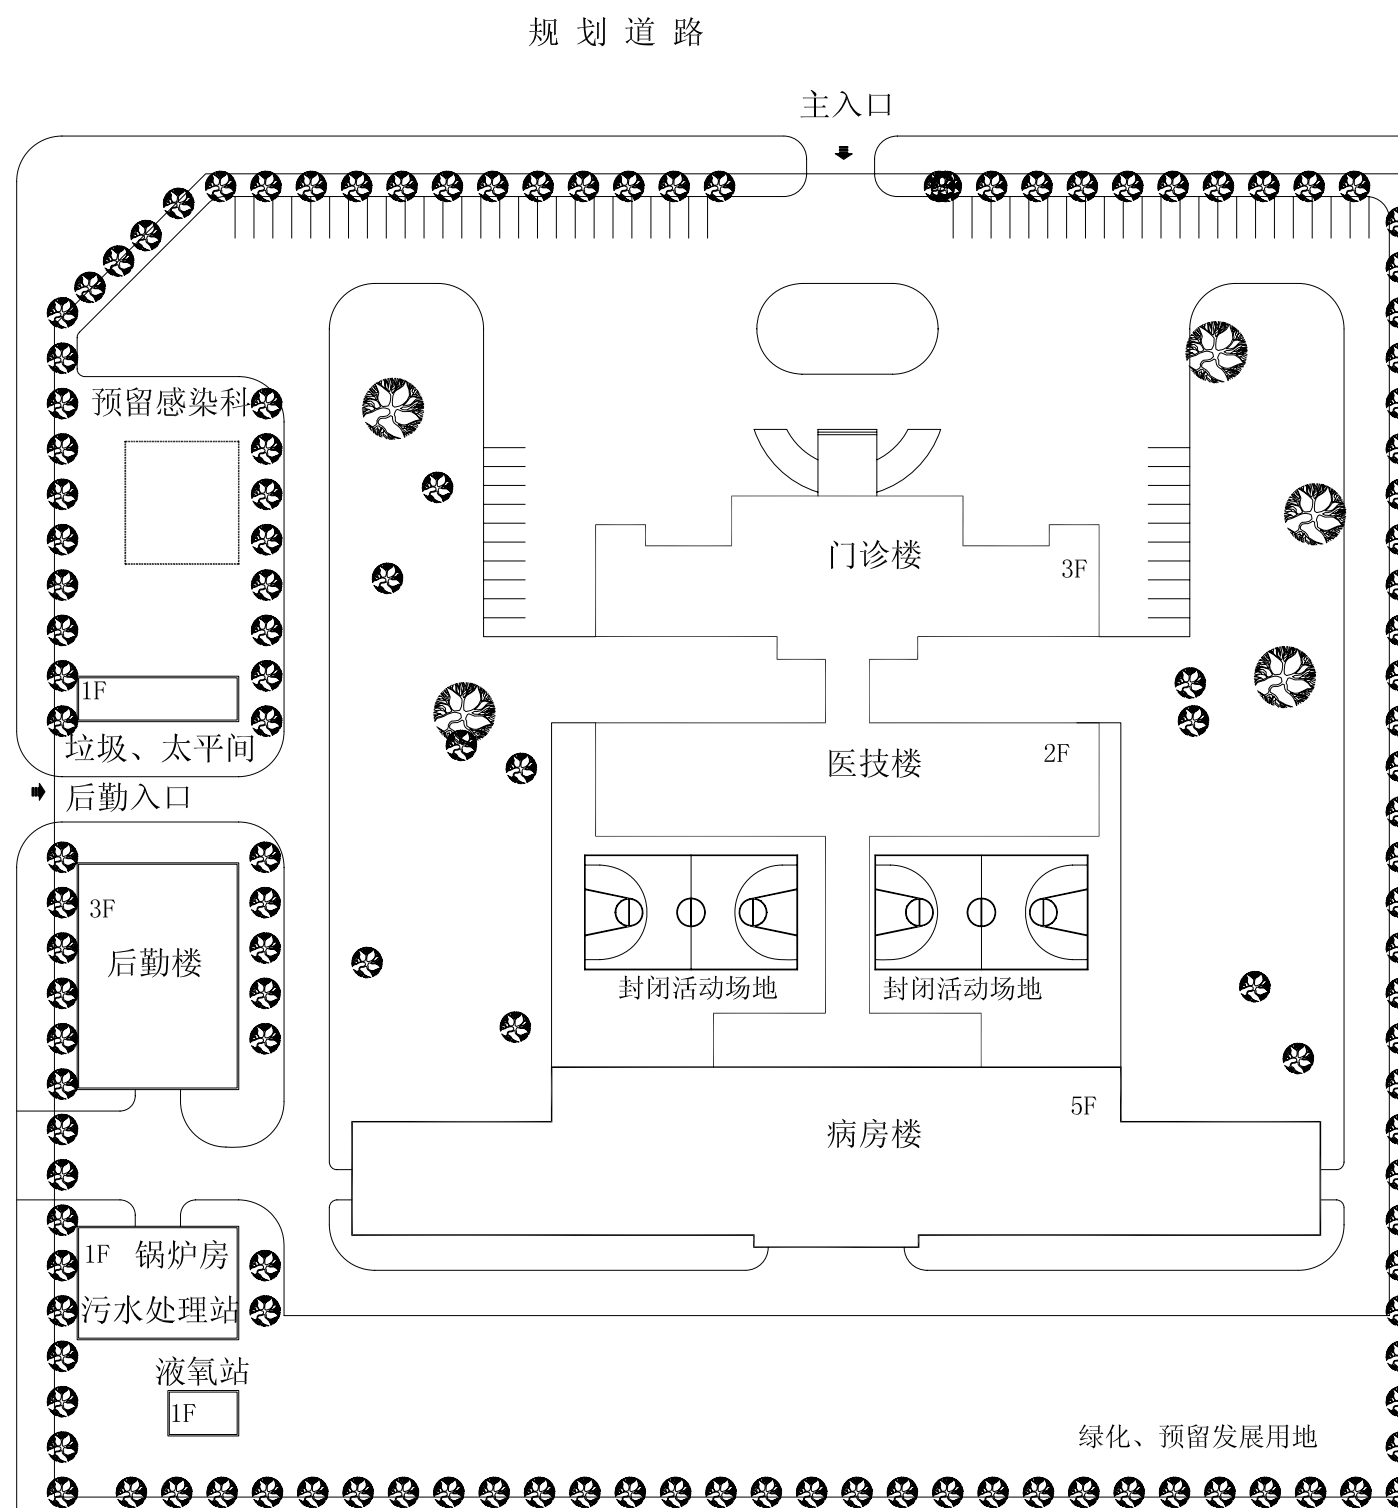


主要技术经济指标

用地面积	31400m ²
总建筑面积	18386m ²
床位数	320 张
床均面积:	57.36 m ² /床


总平面图 1:1000

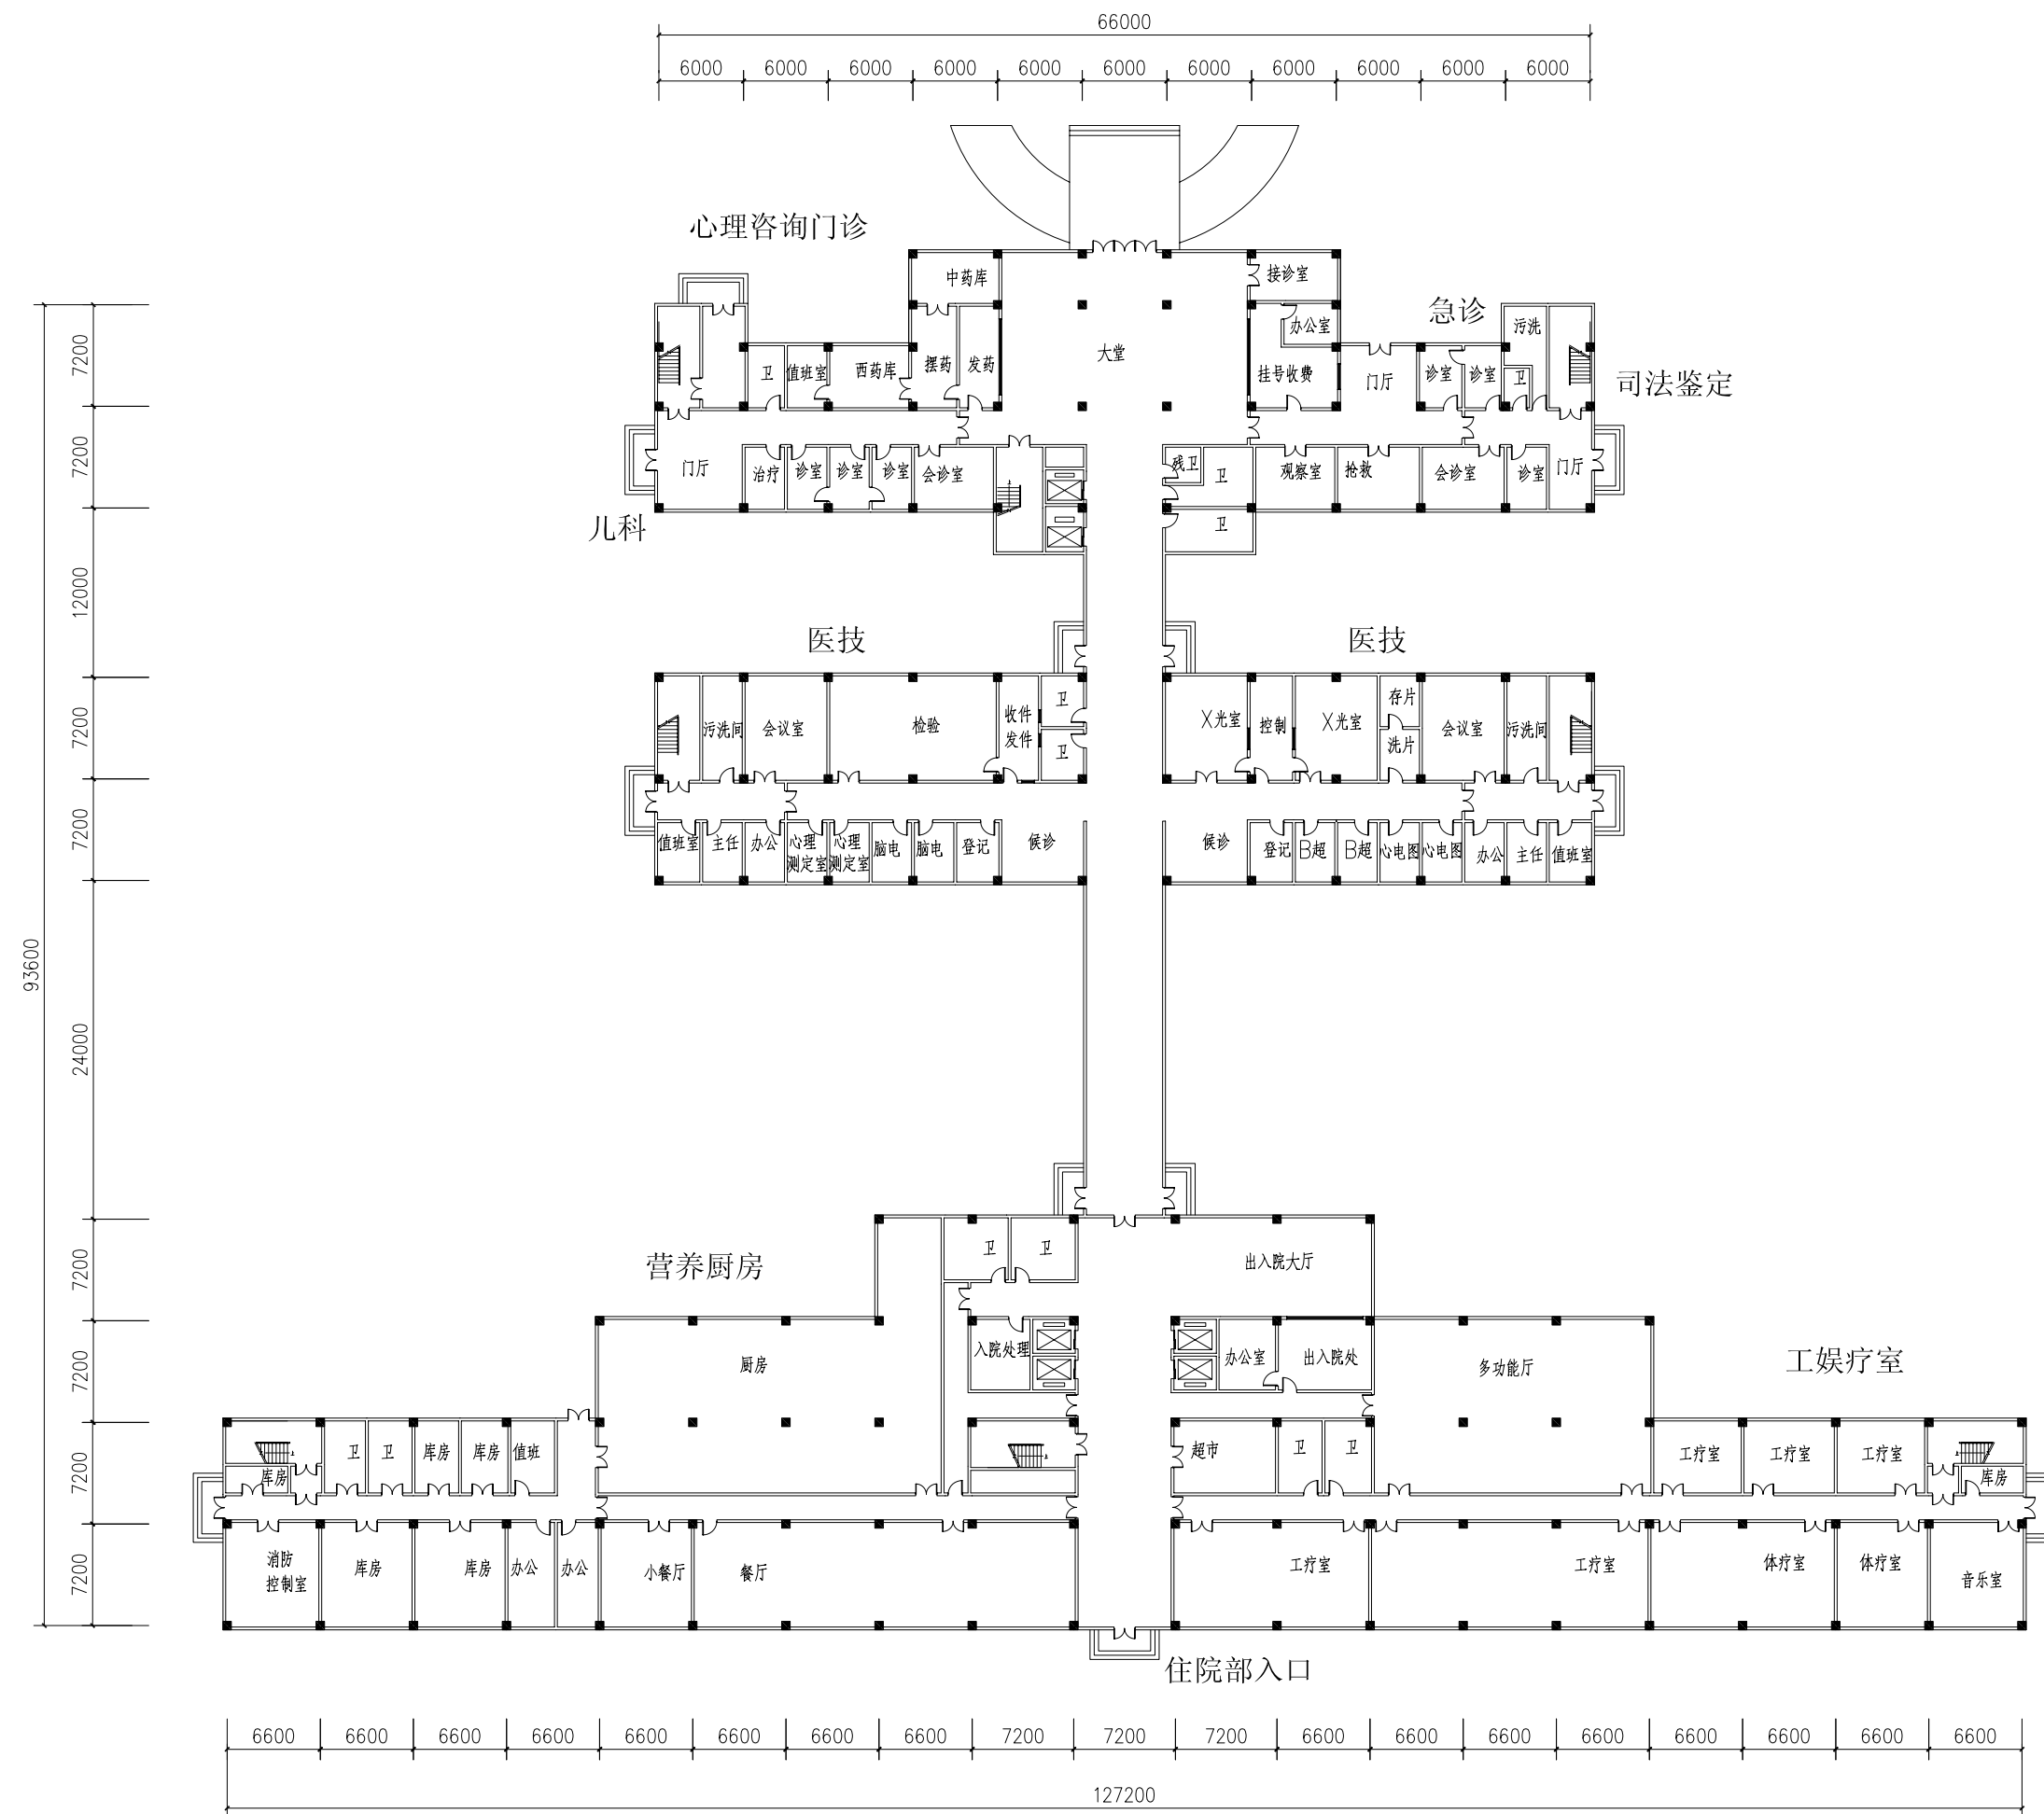


一层平面图 1:500

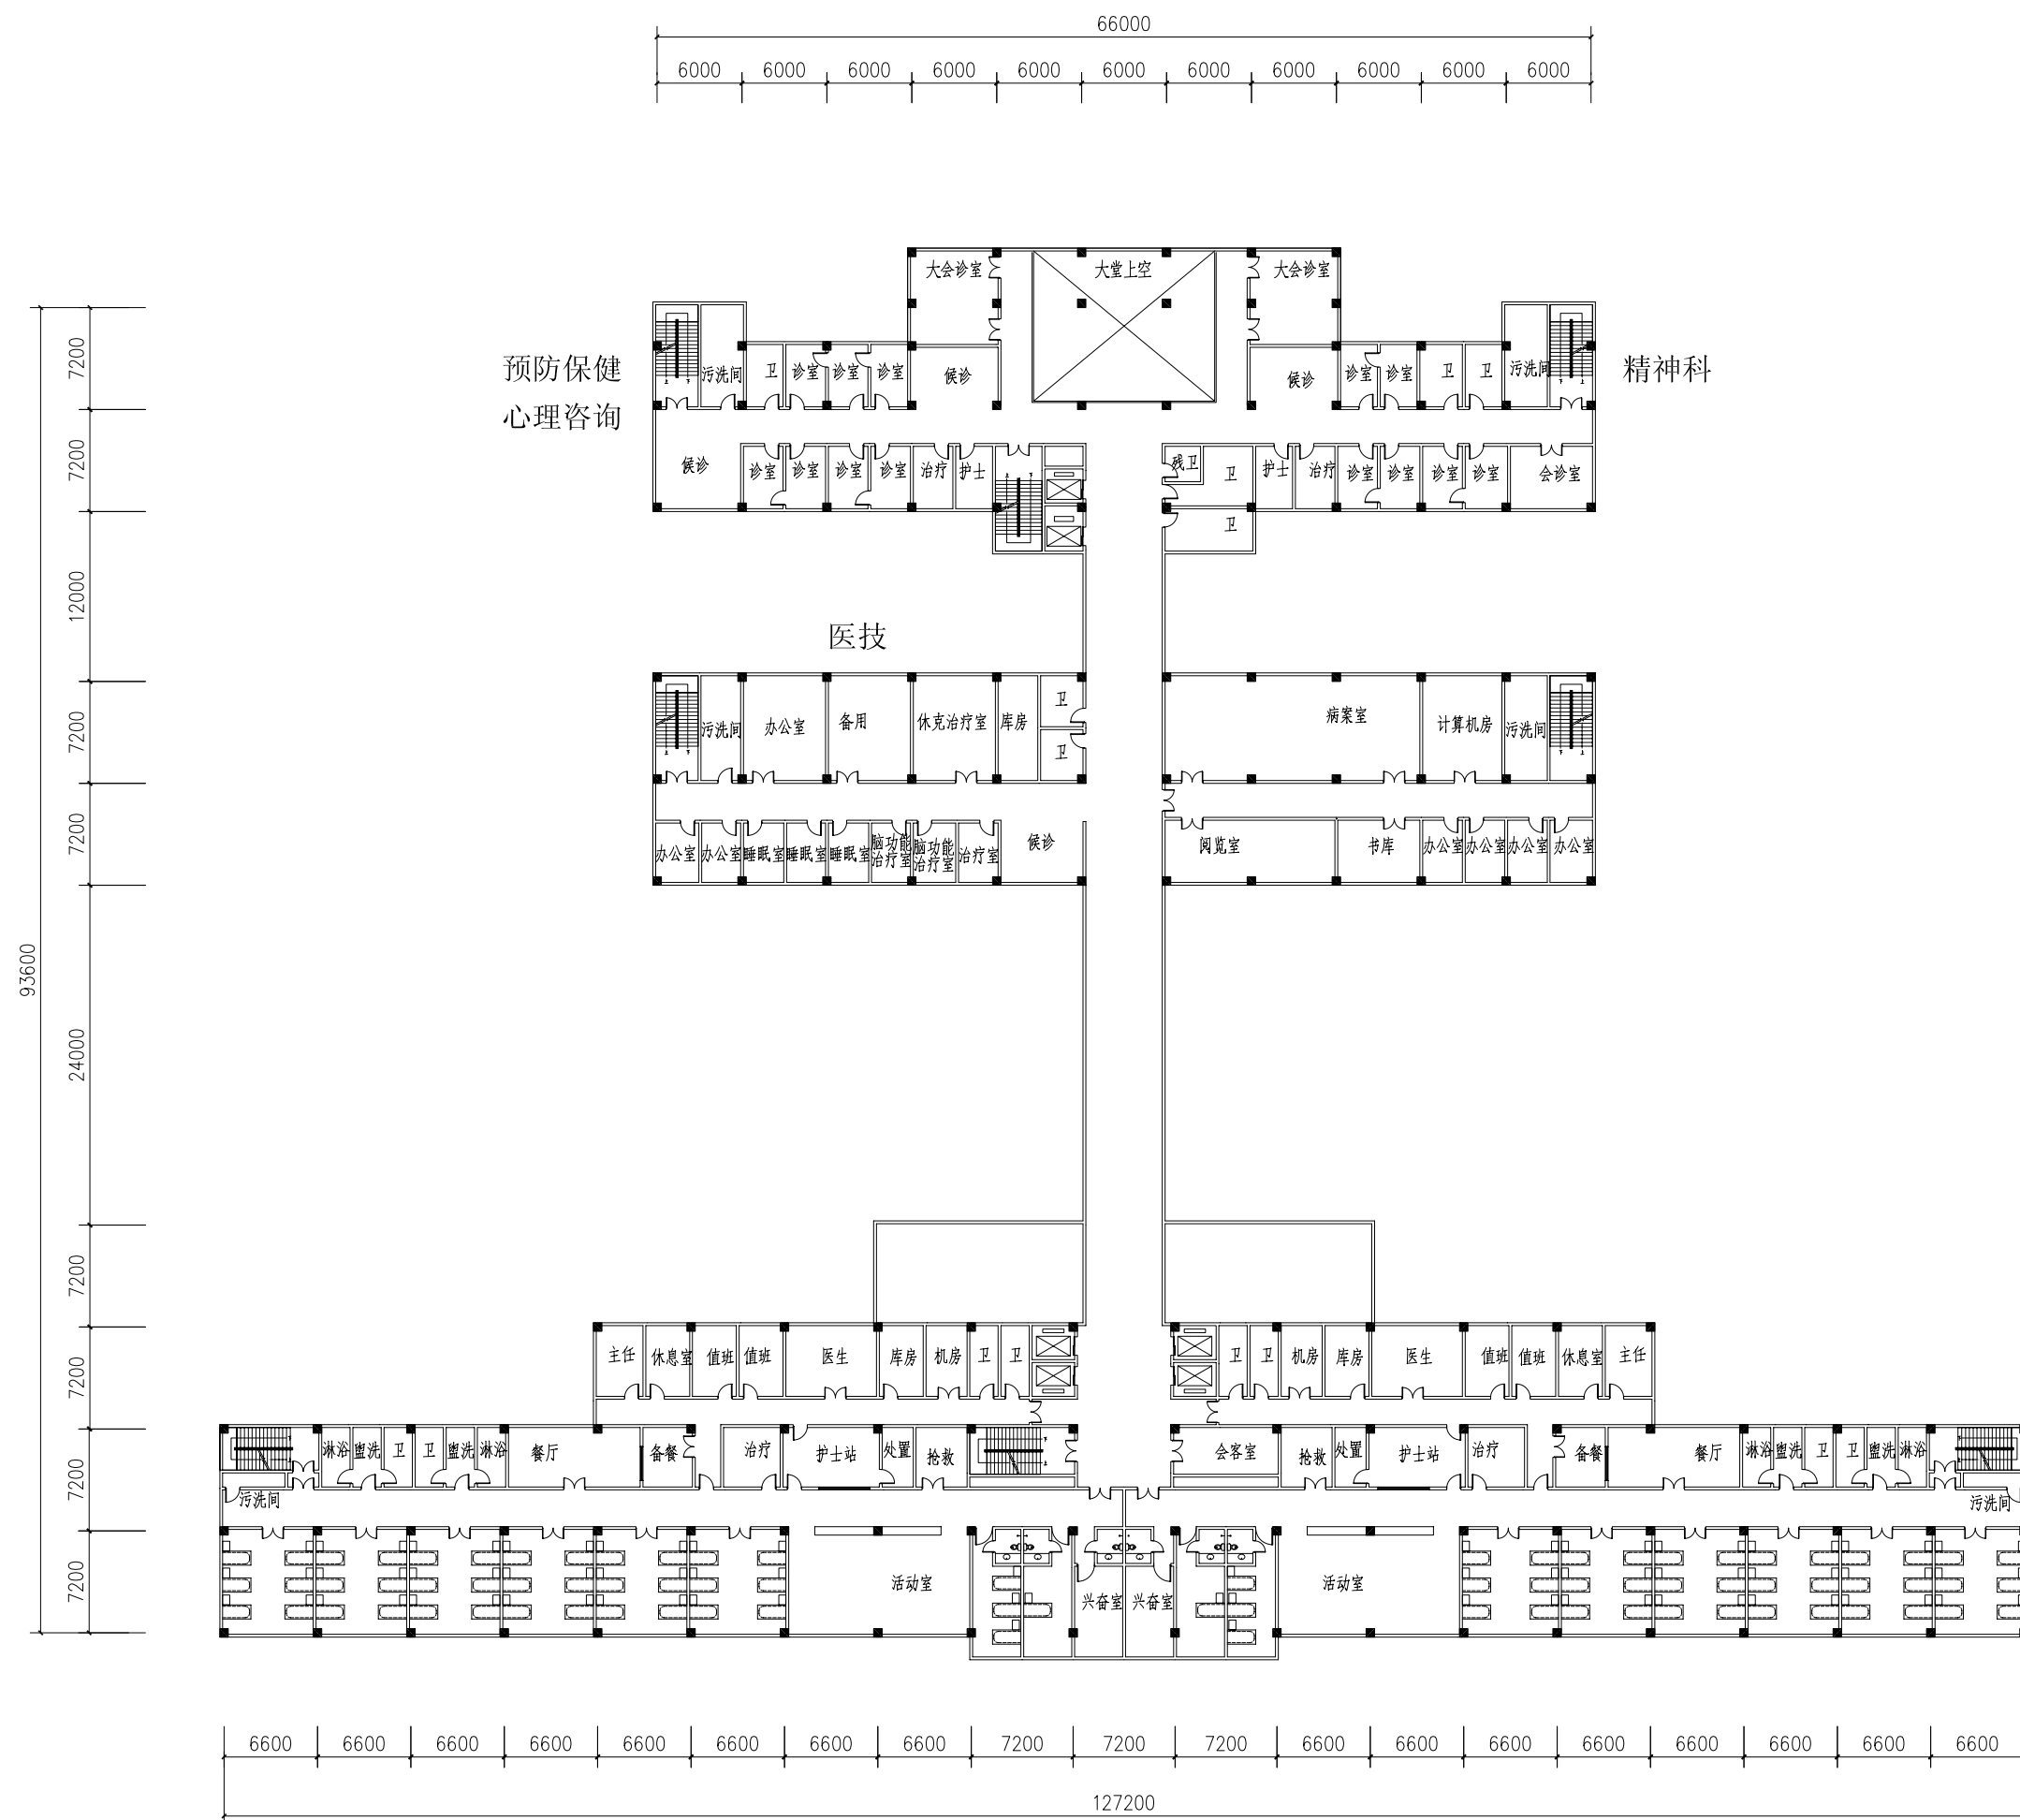



二层平面图 1:500

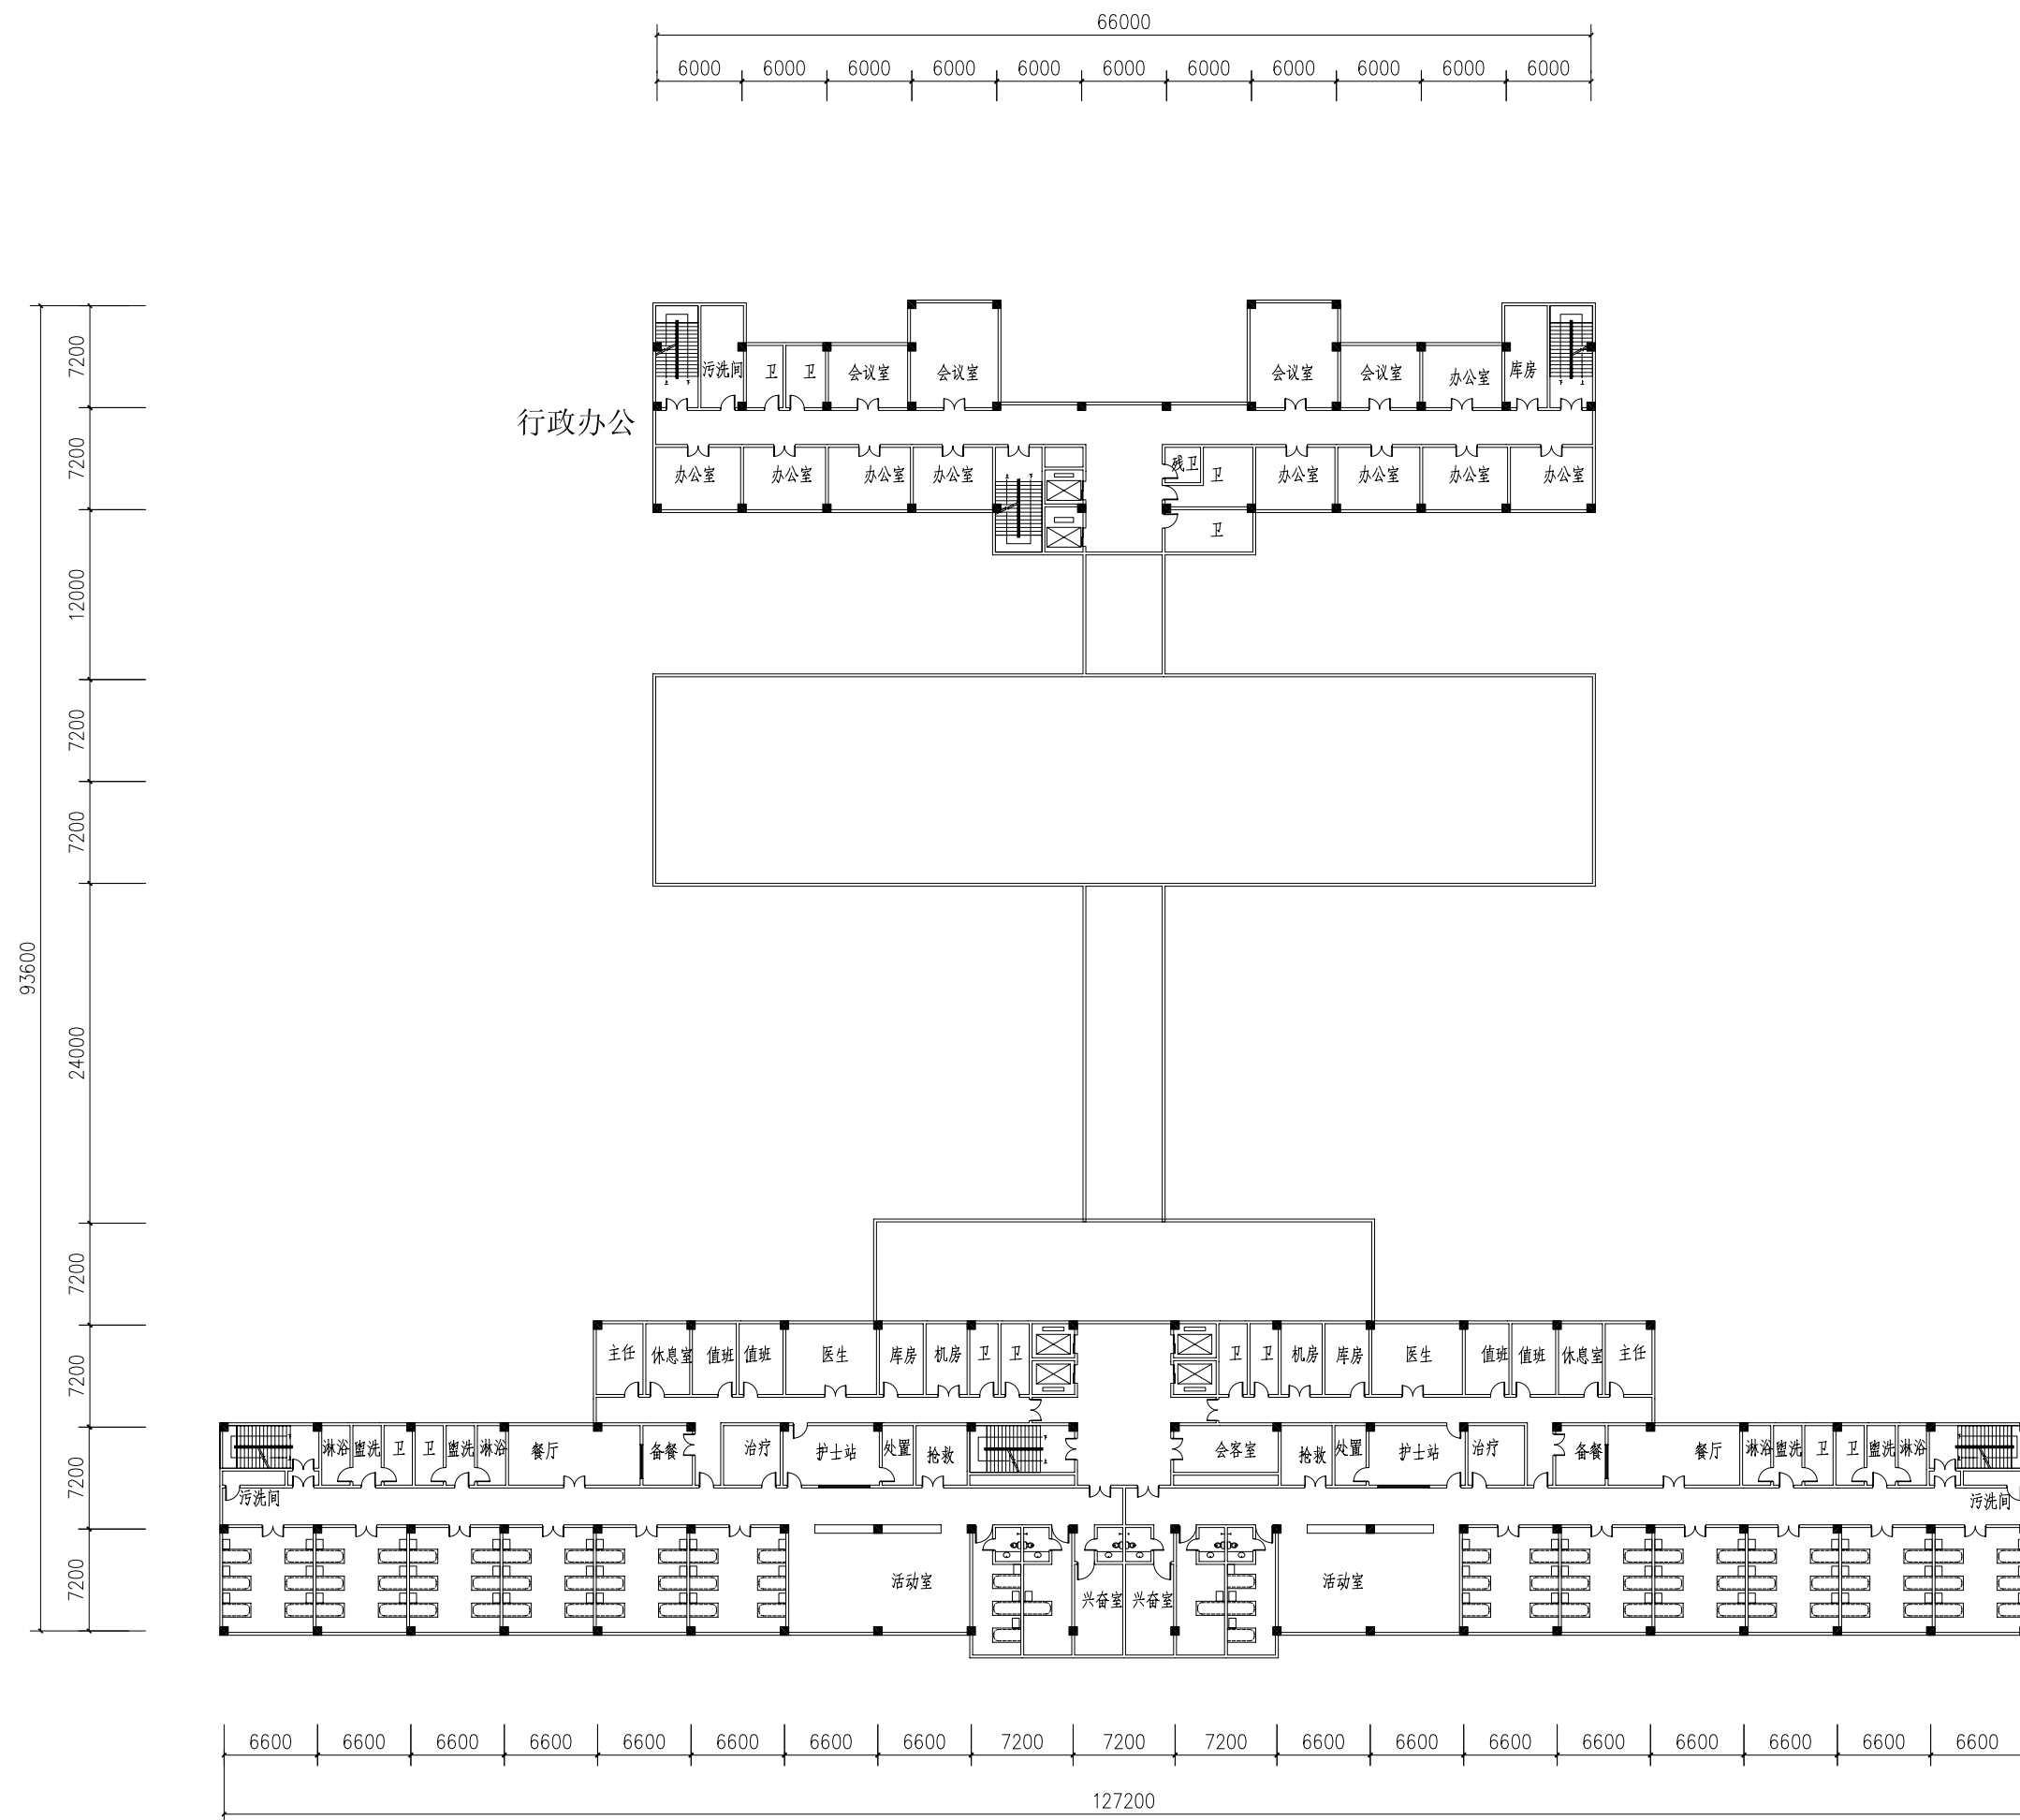

三层平面图 1:500

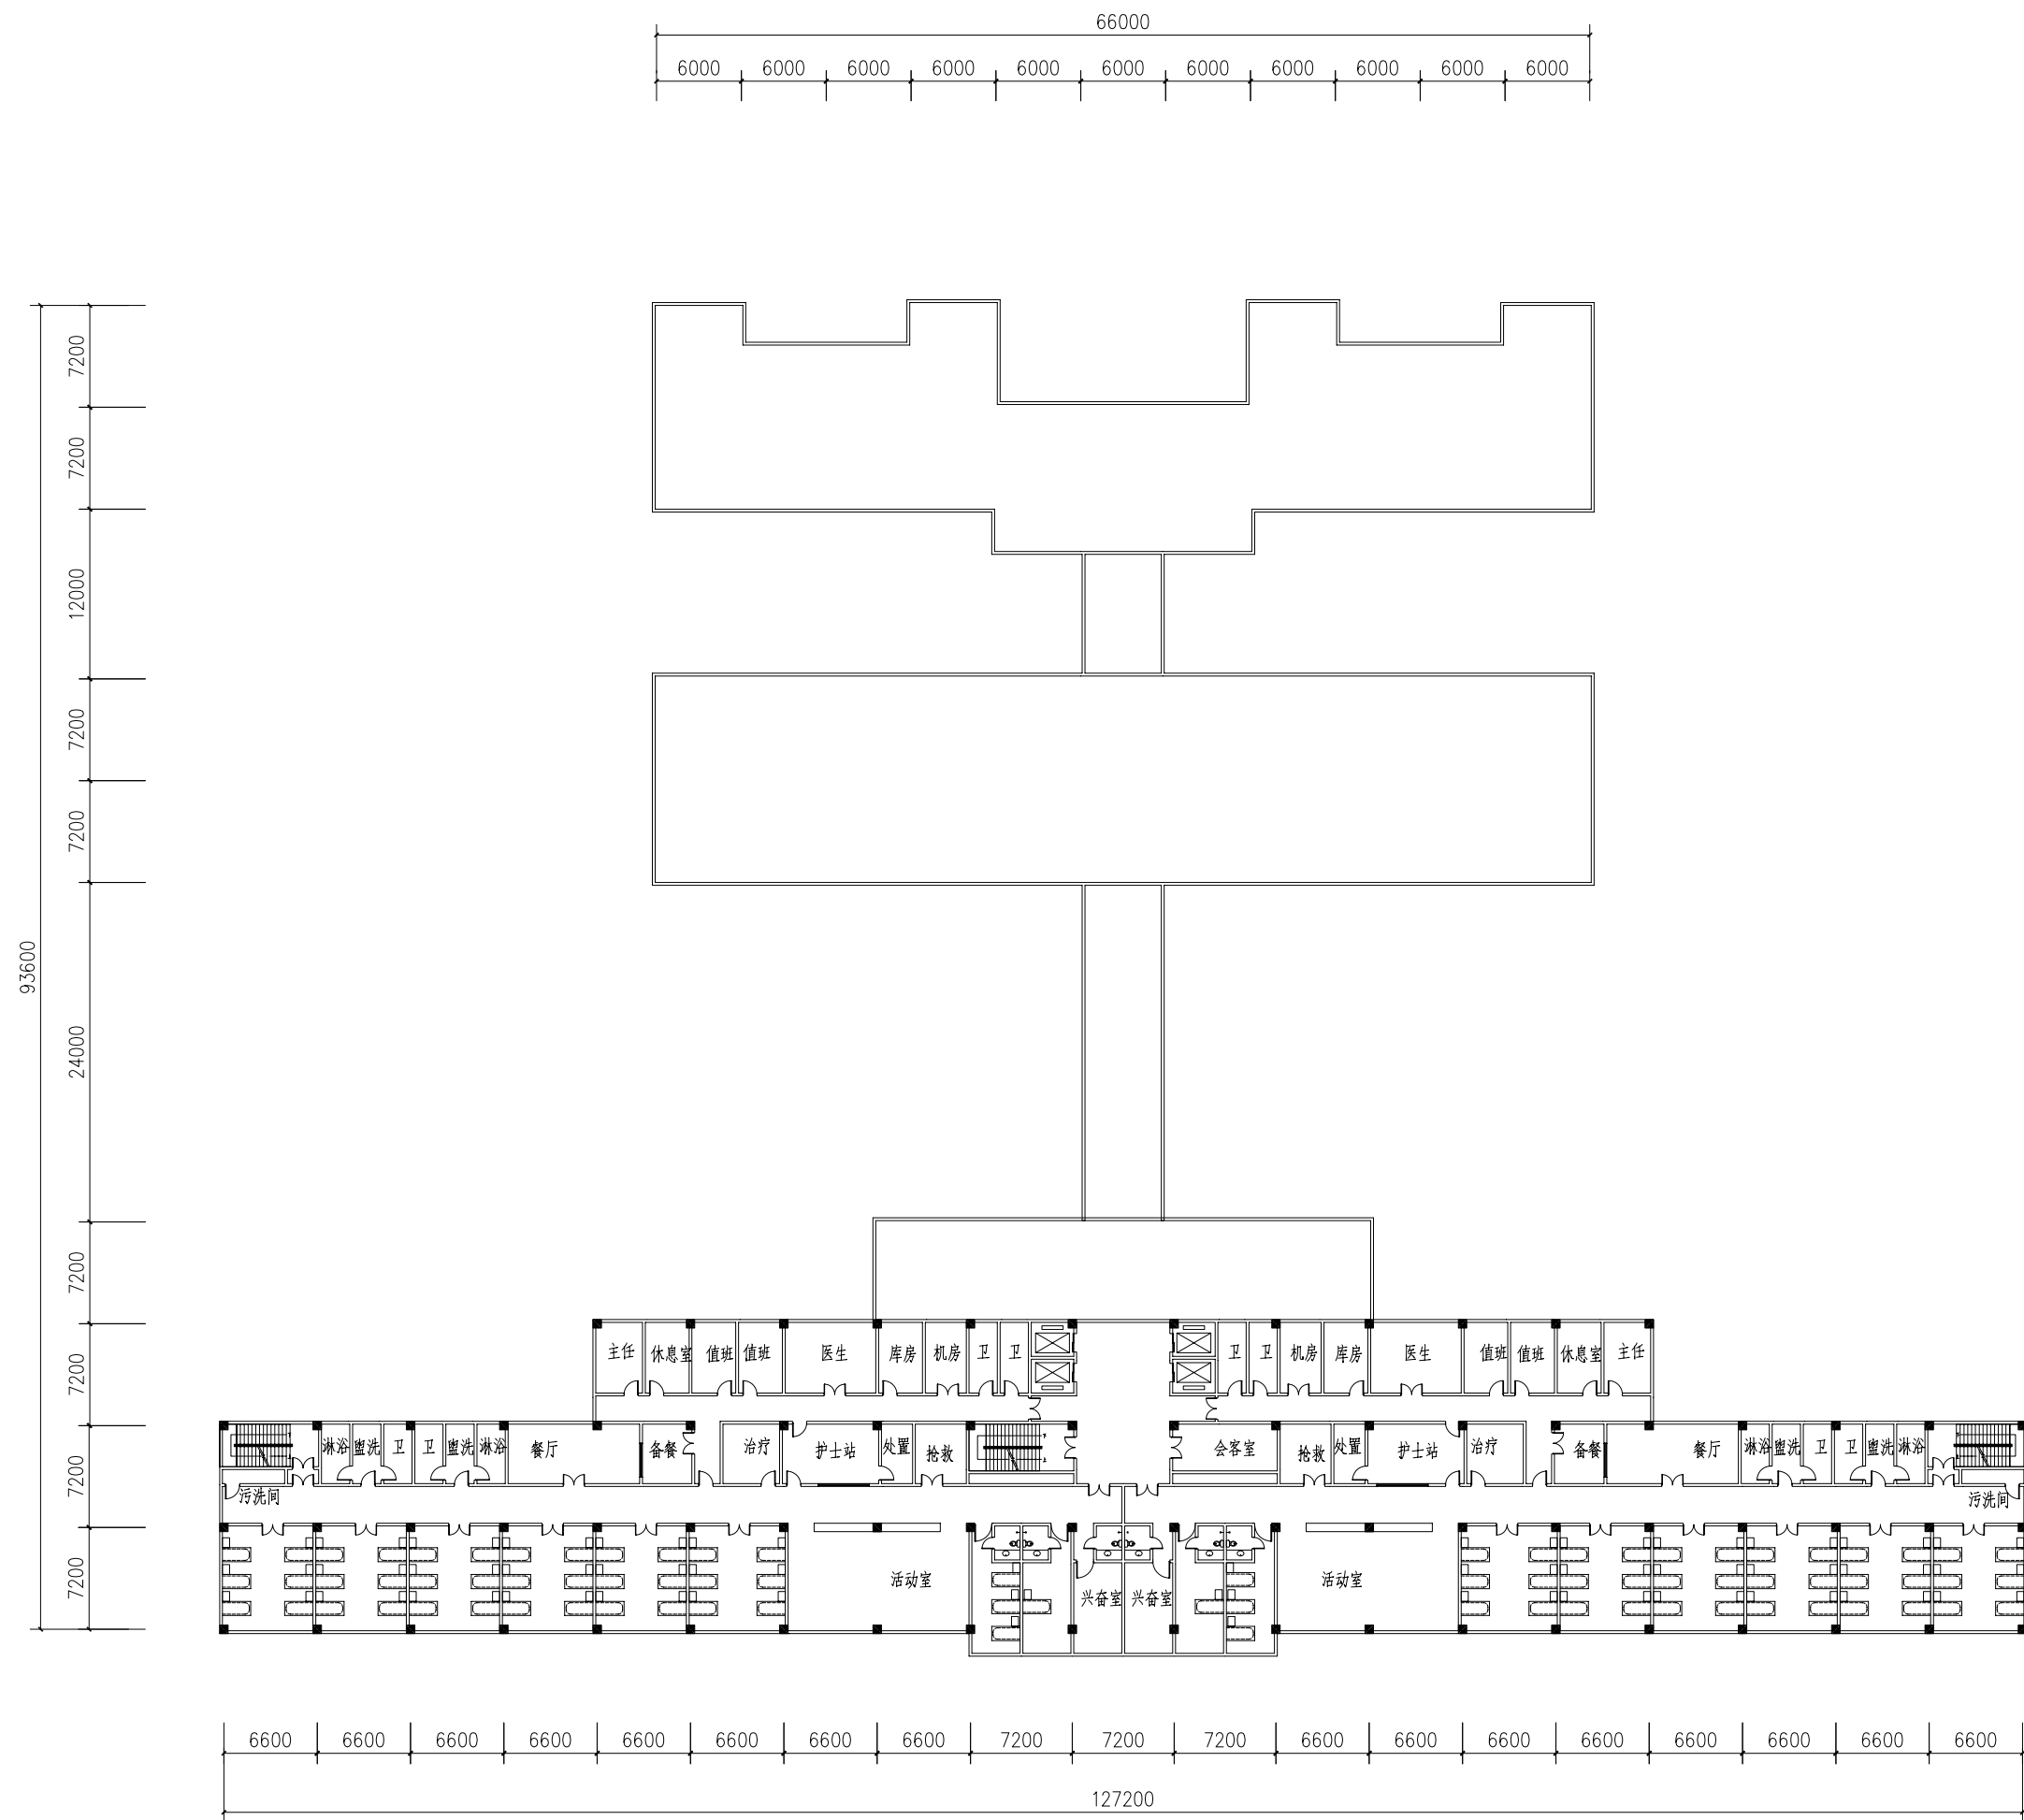


四-五层平面图1:500

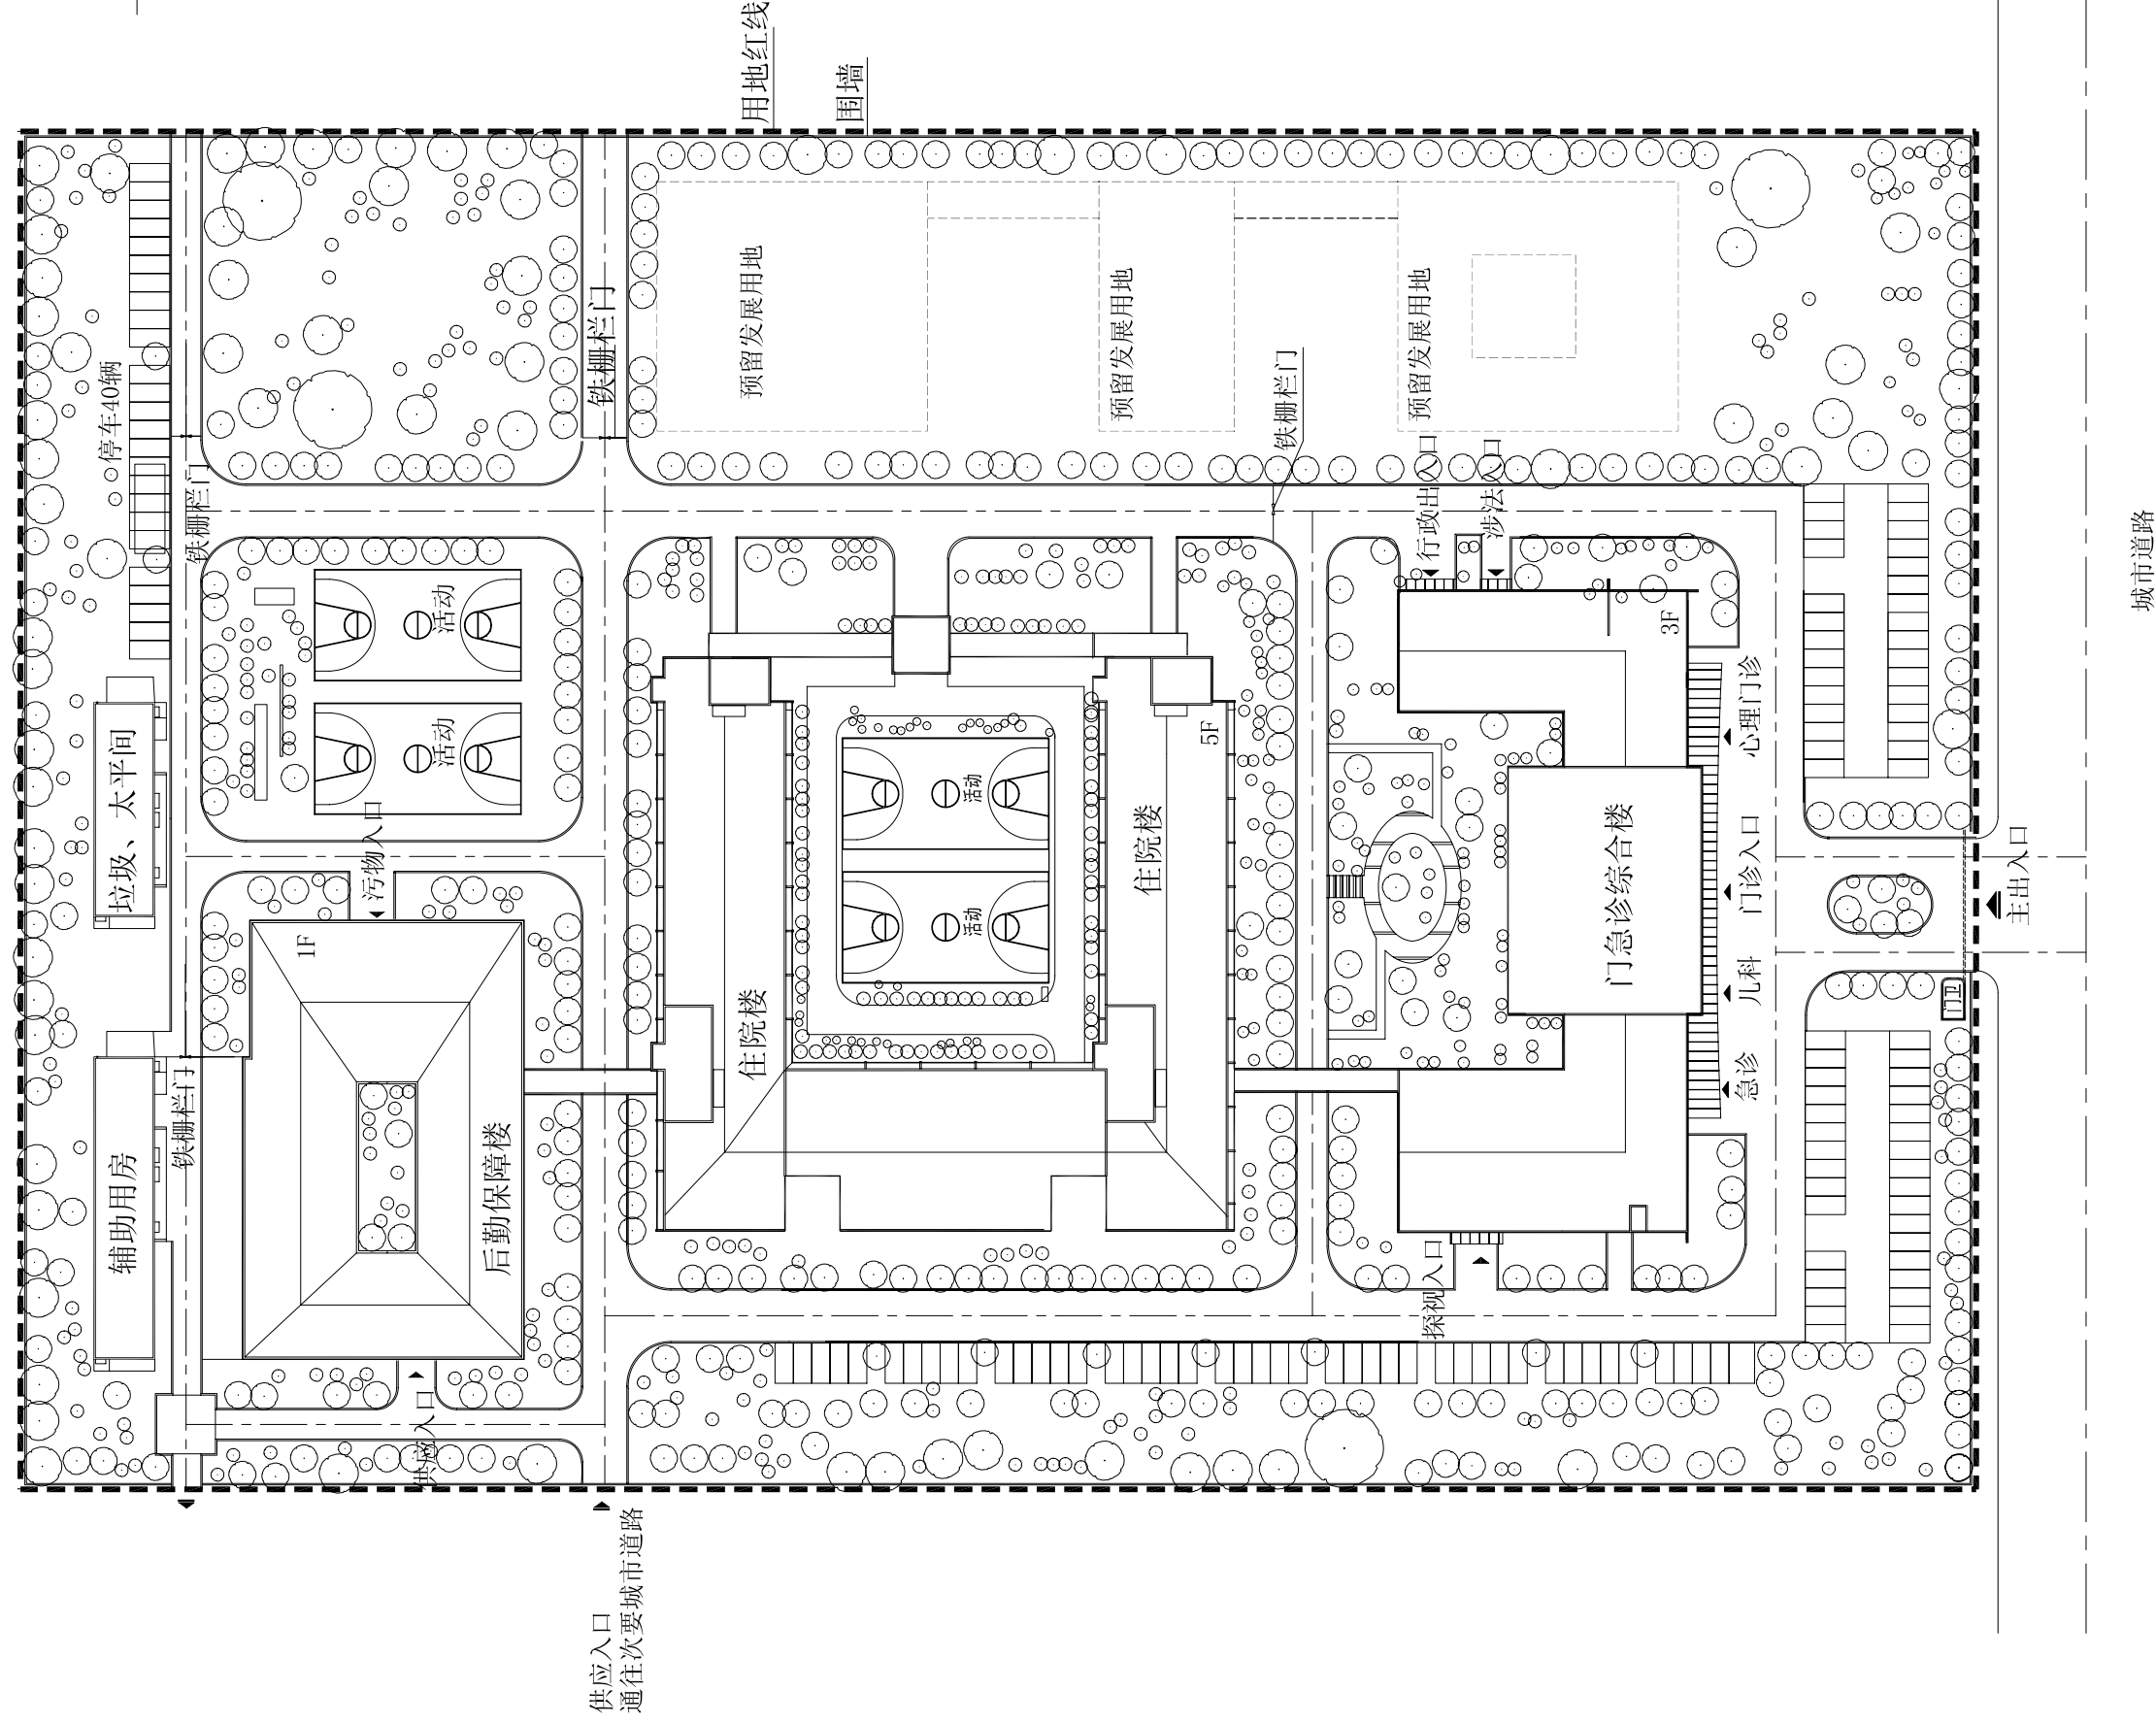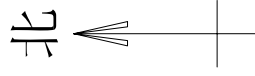


主要技术经济指标




用地面积	49302.5m ²
总建筑面积	30183m ²
床位数	500 张
床均面积	60.4m ² /床

总平面图 1:1000

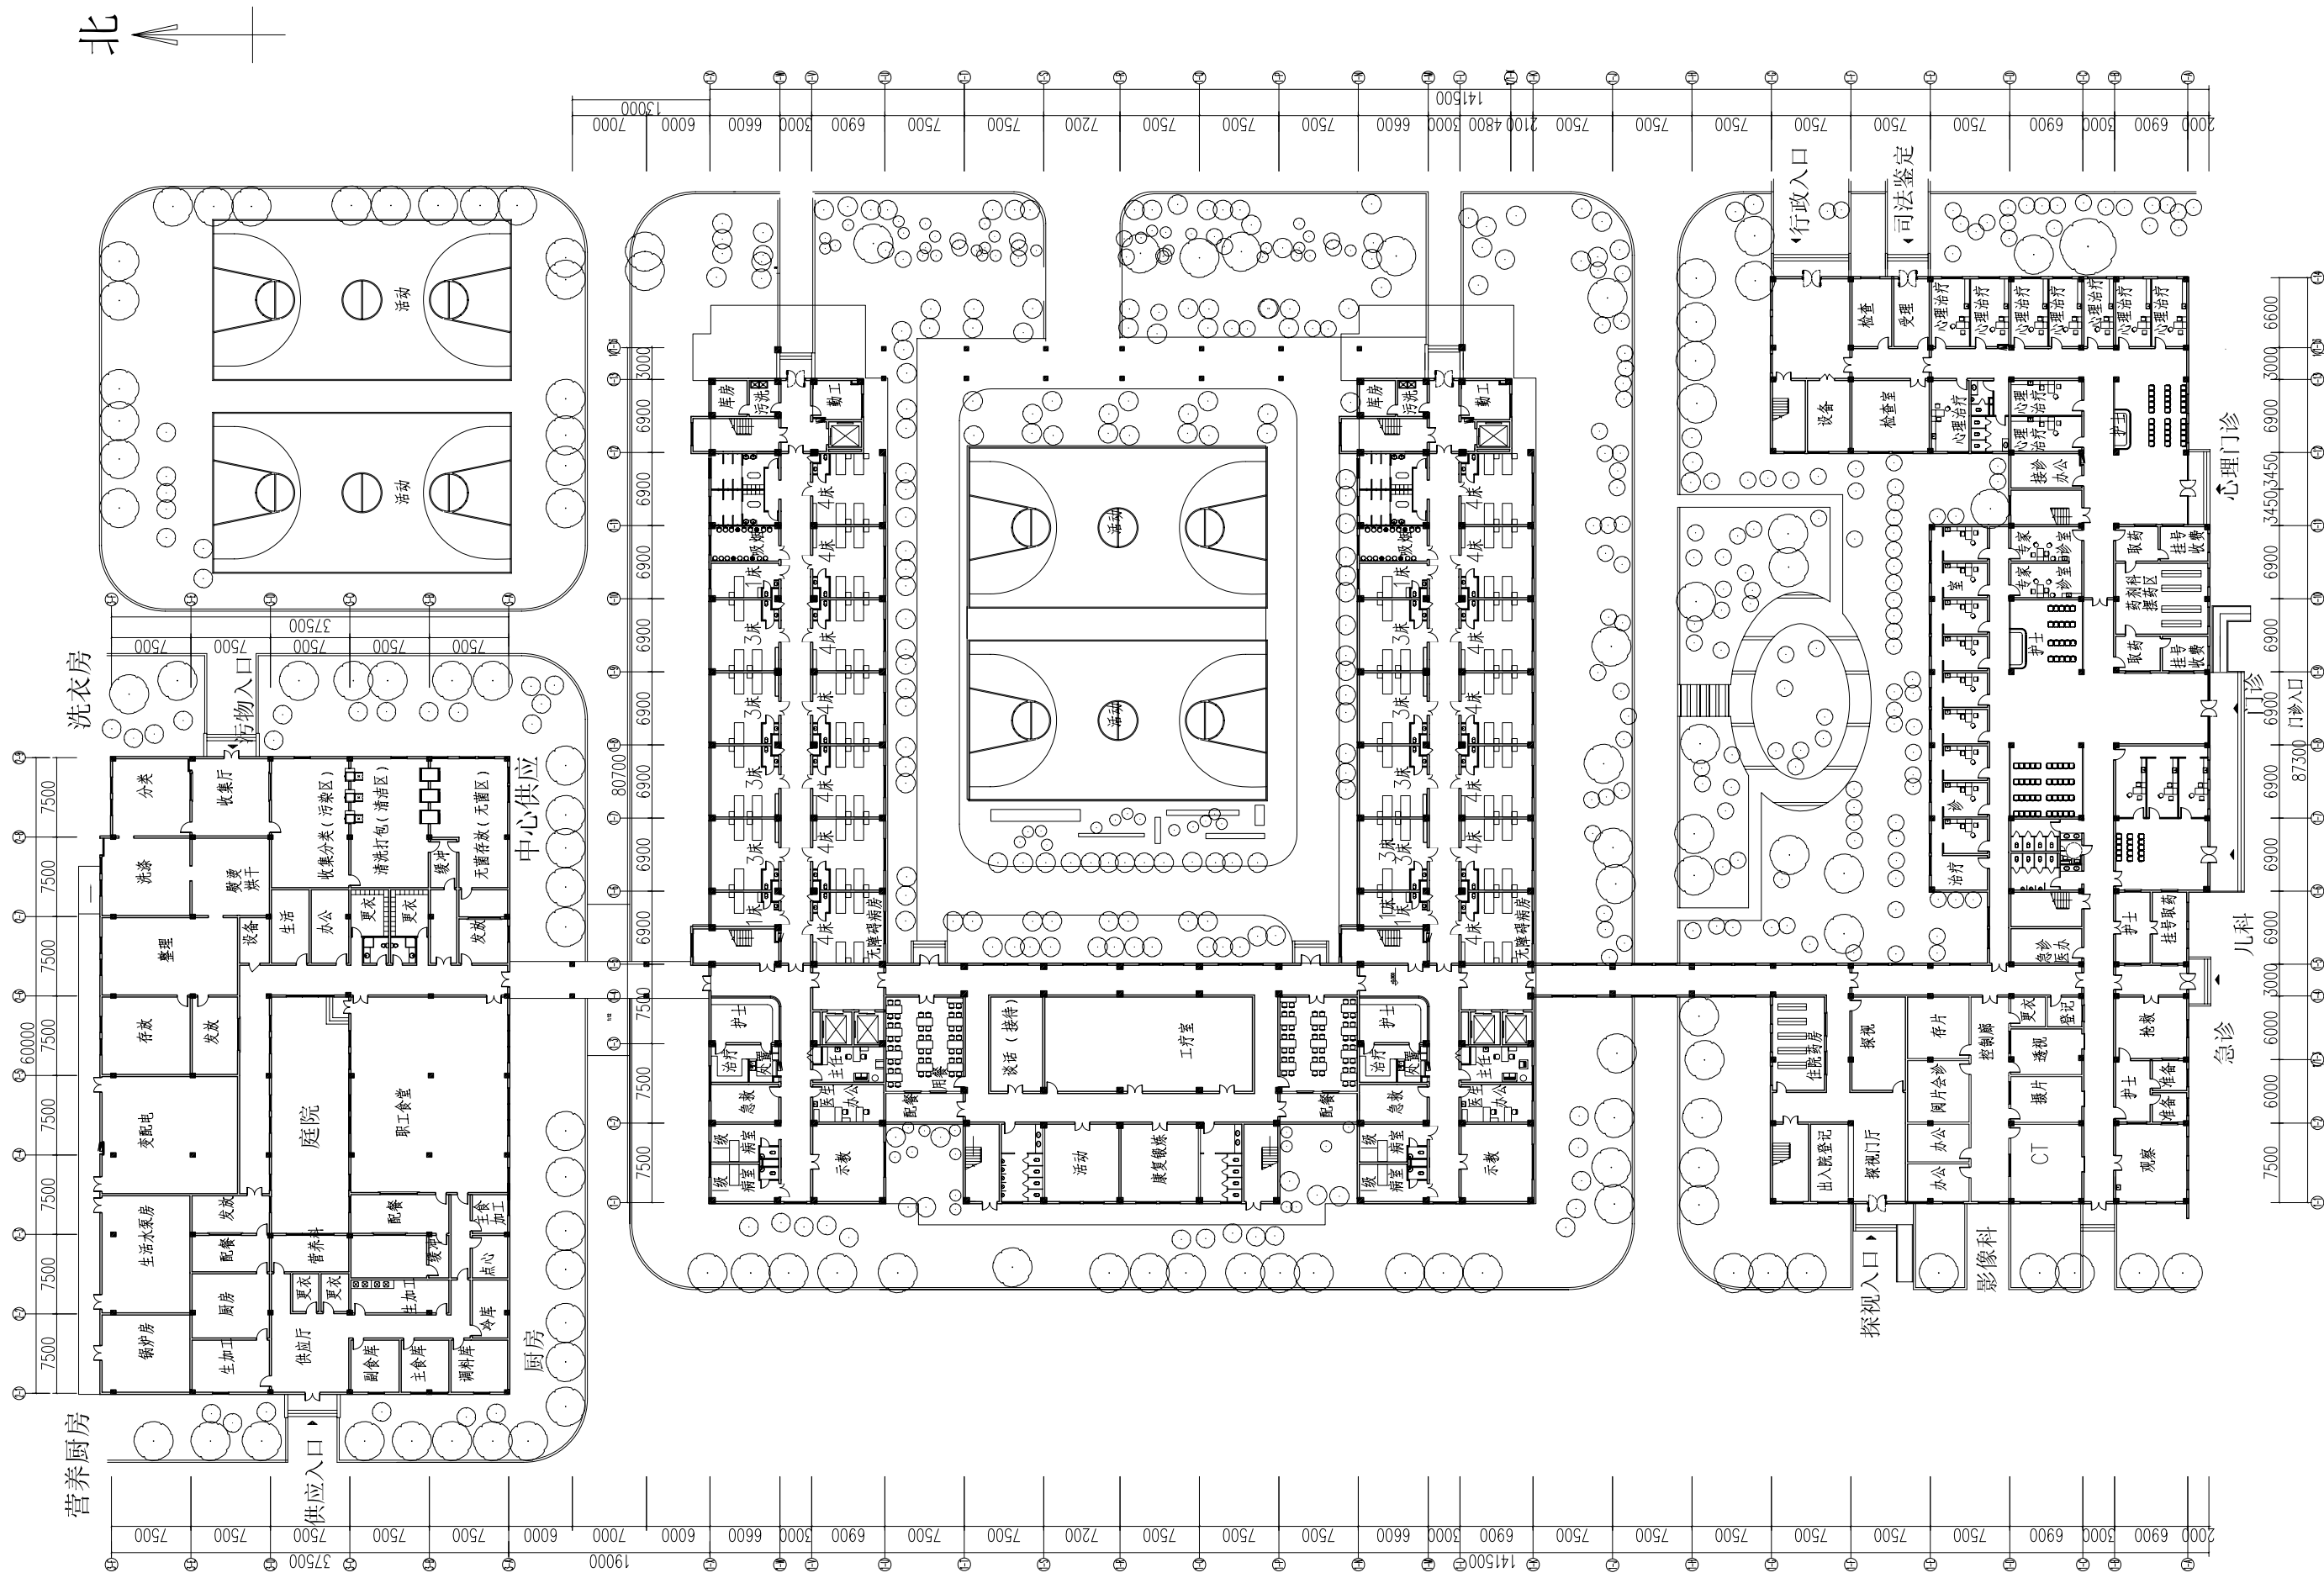


一层平面图 1:600

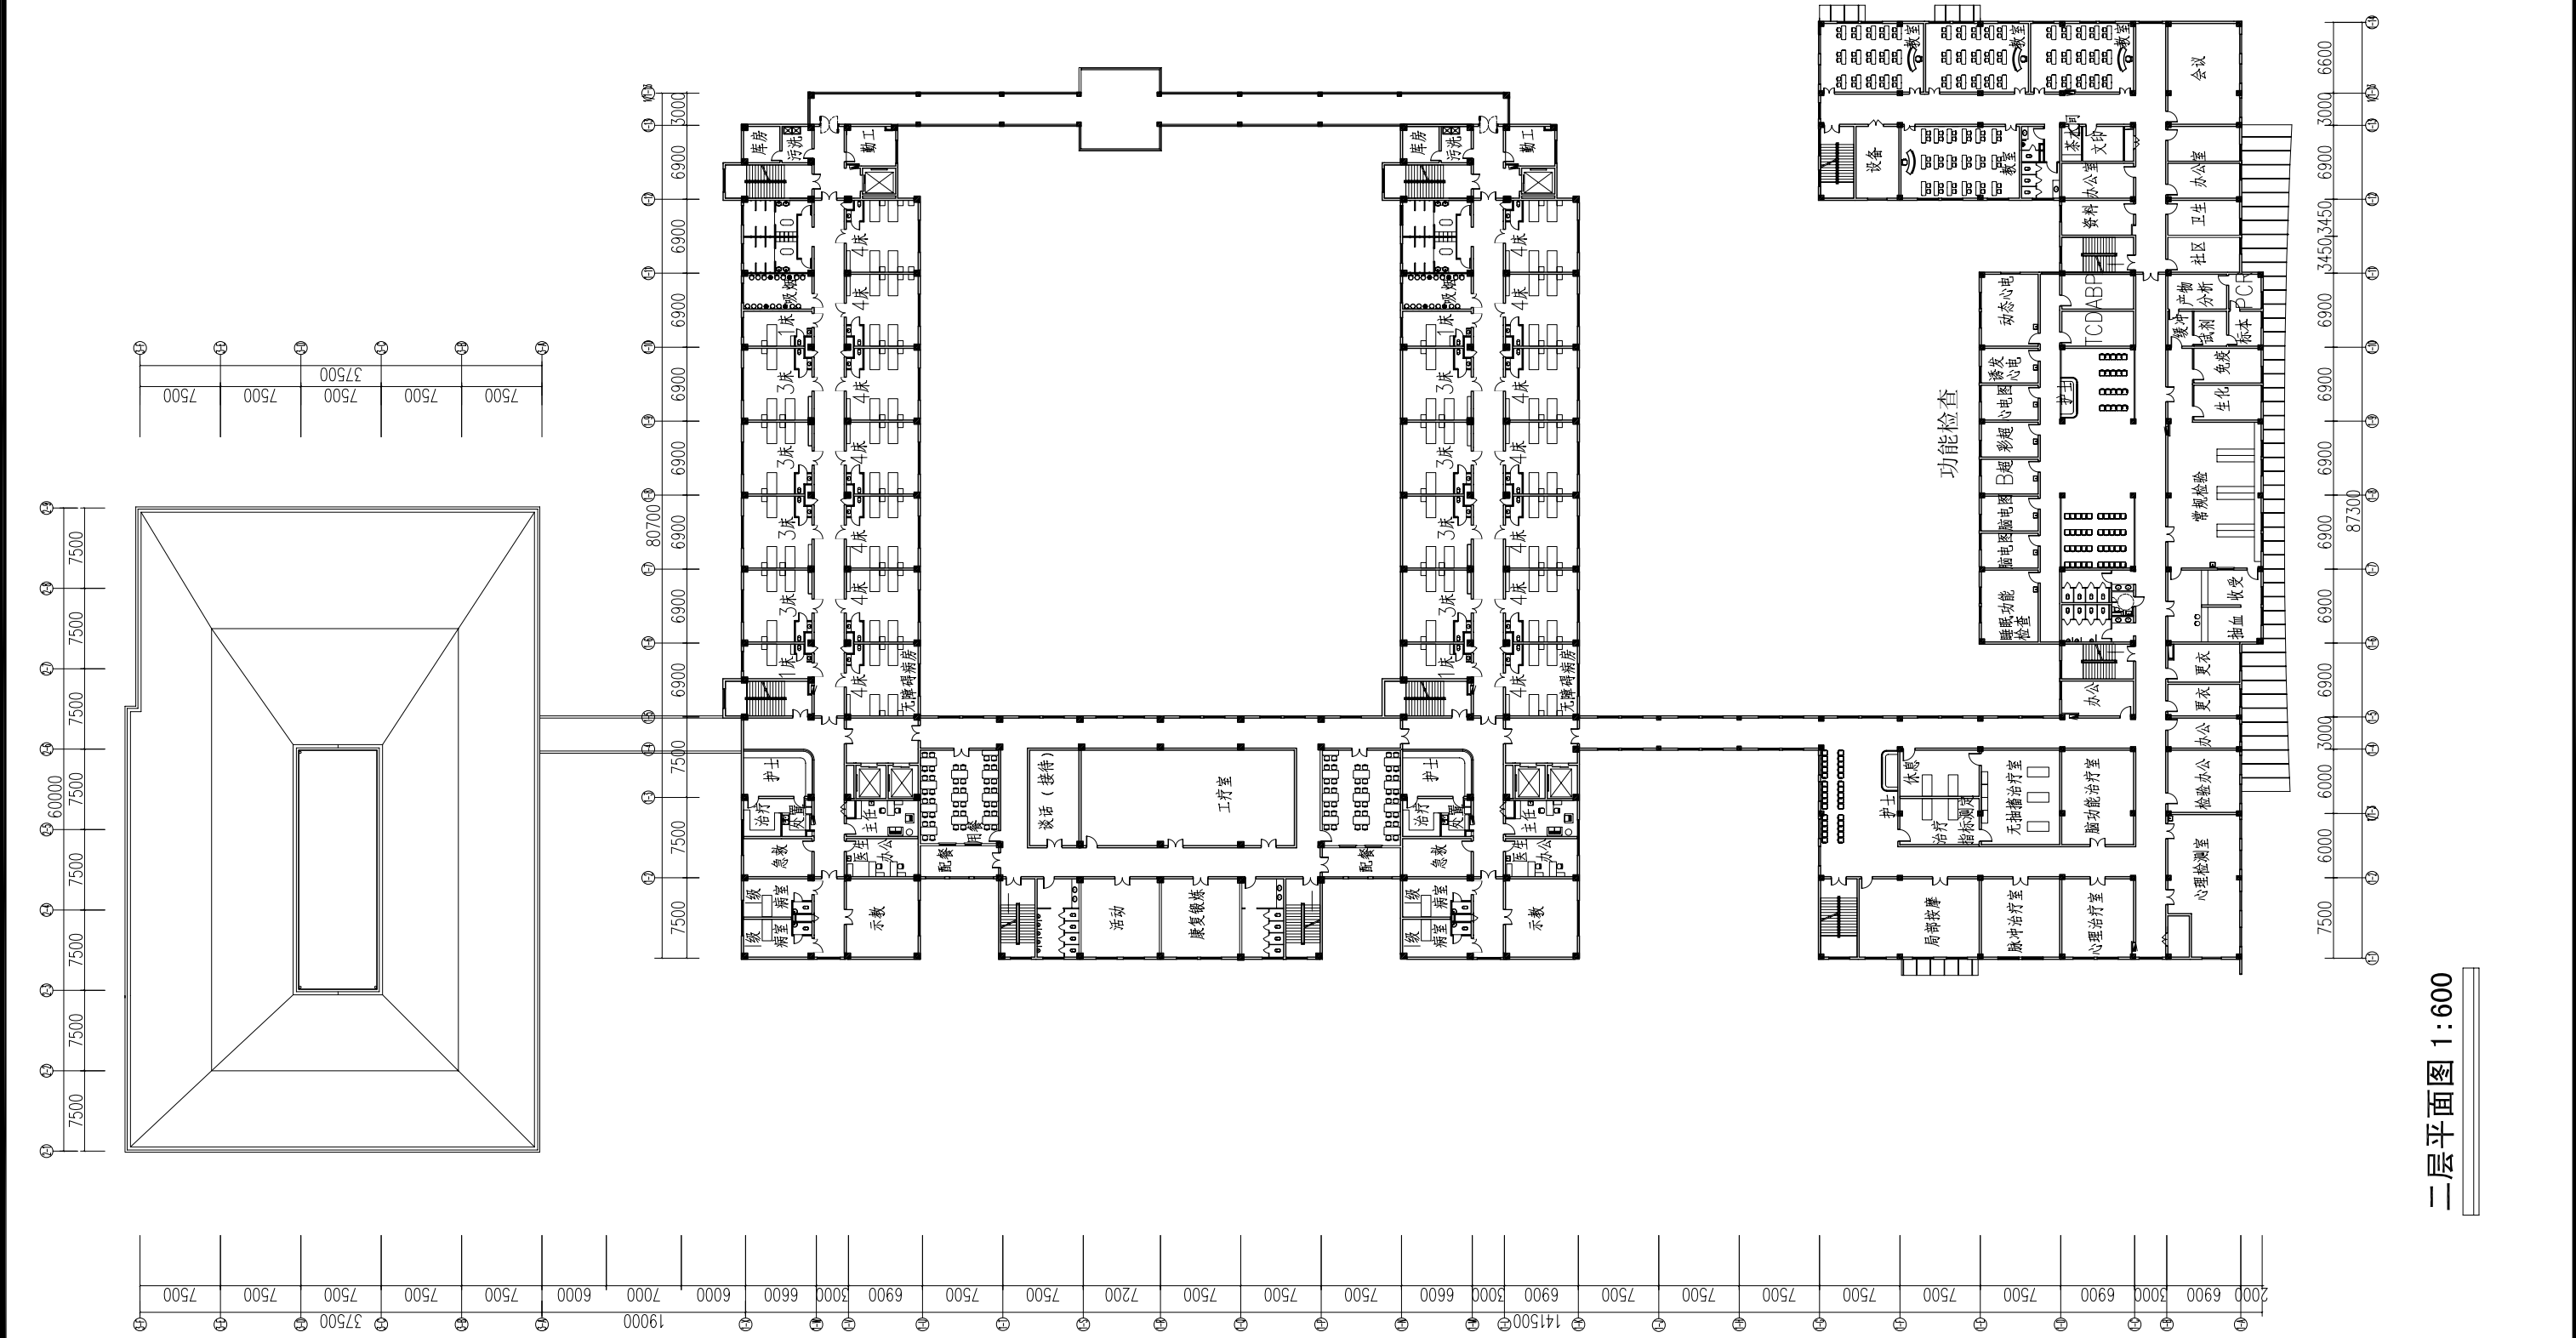


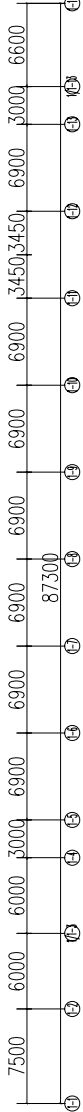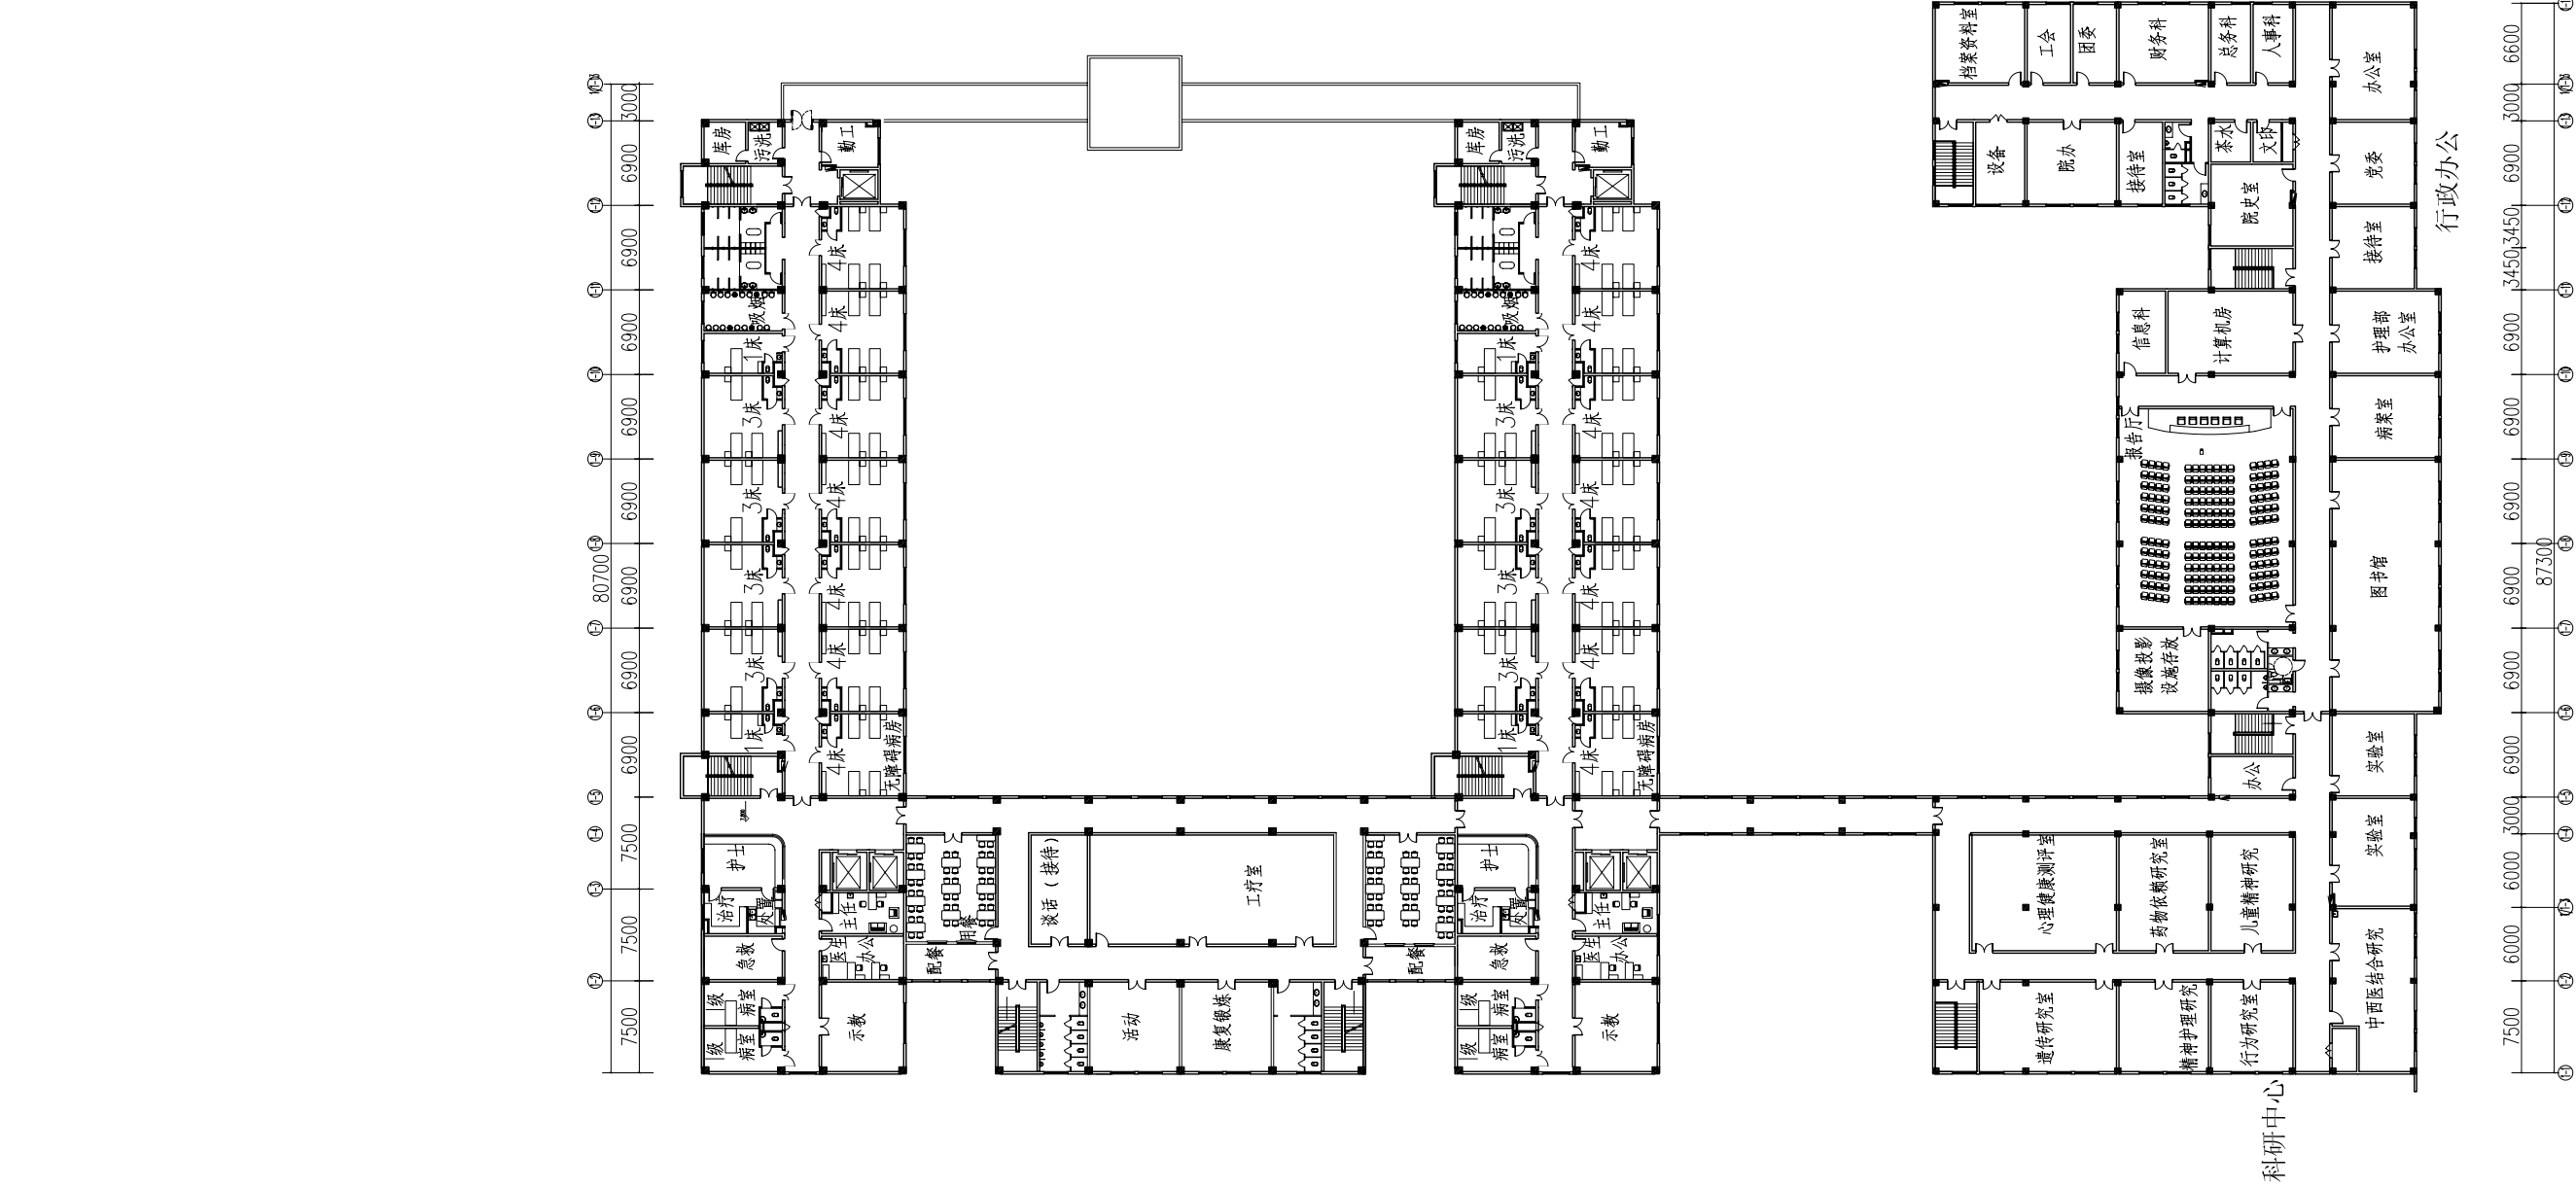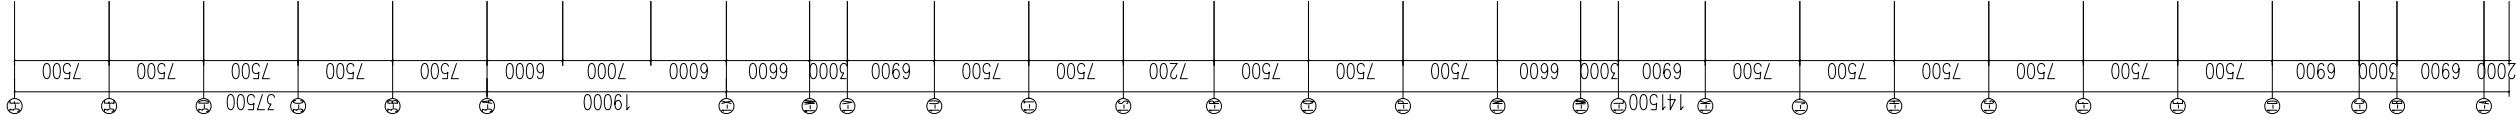

三层平面图 1:600

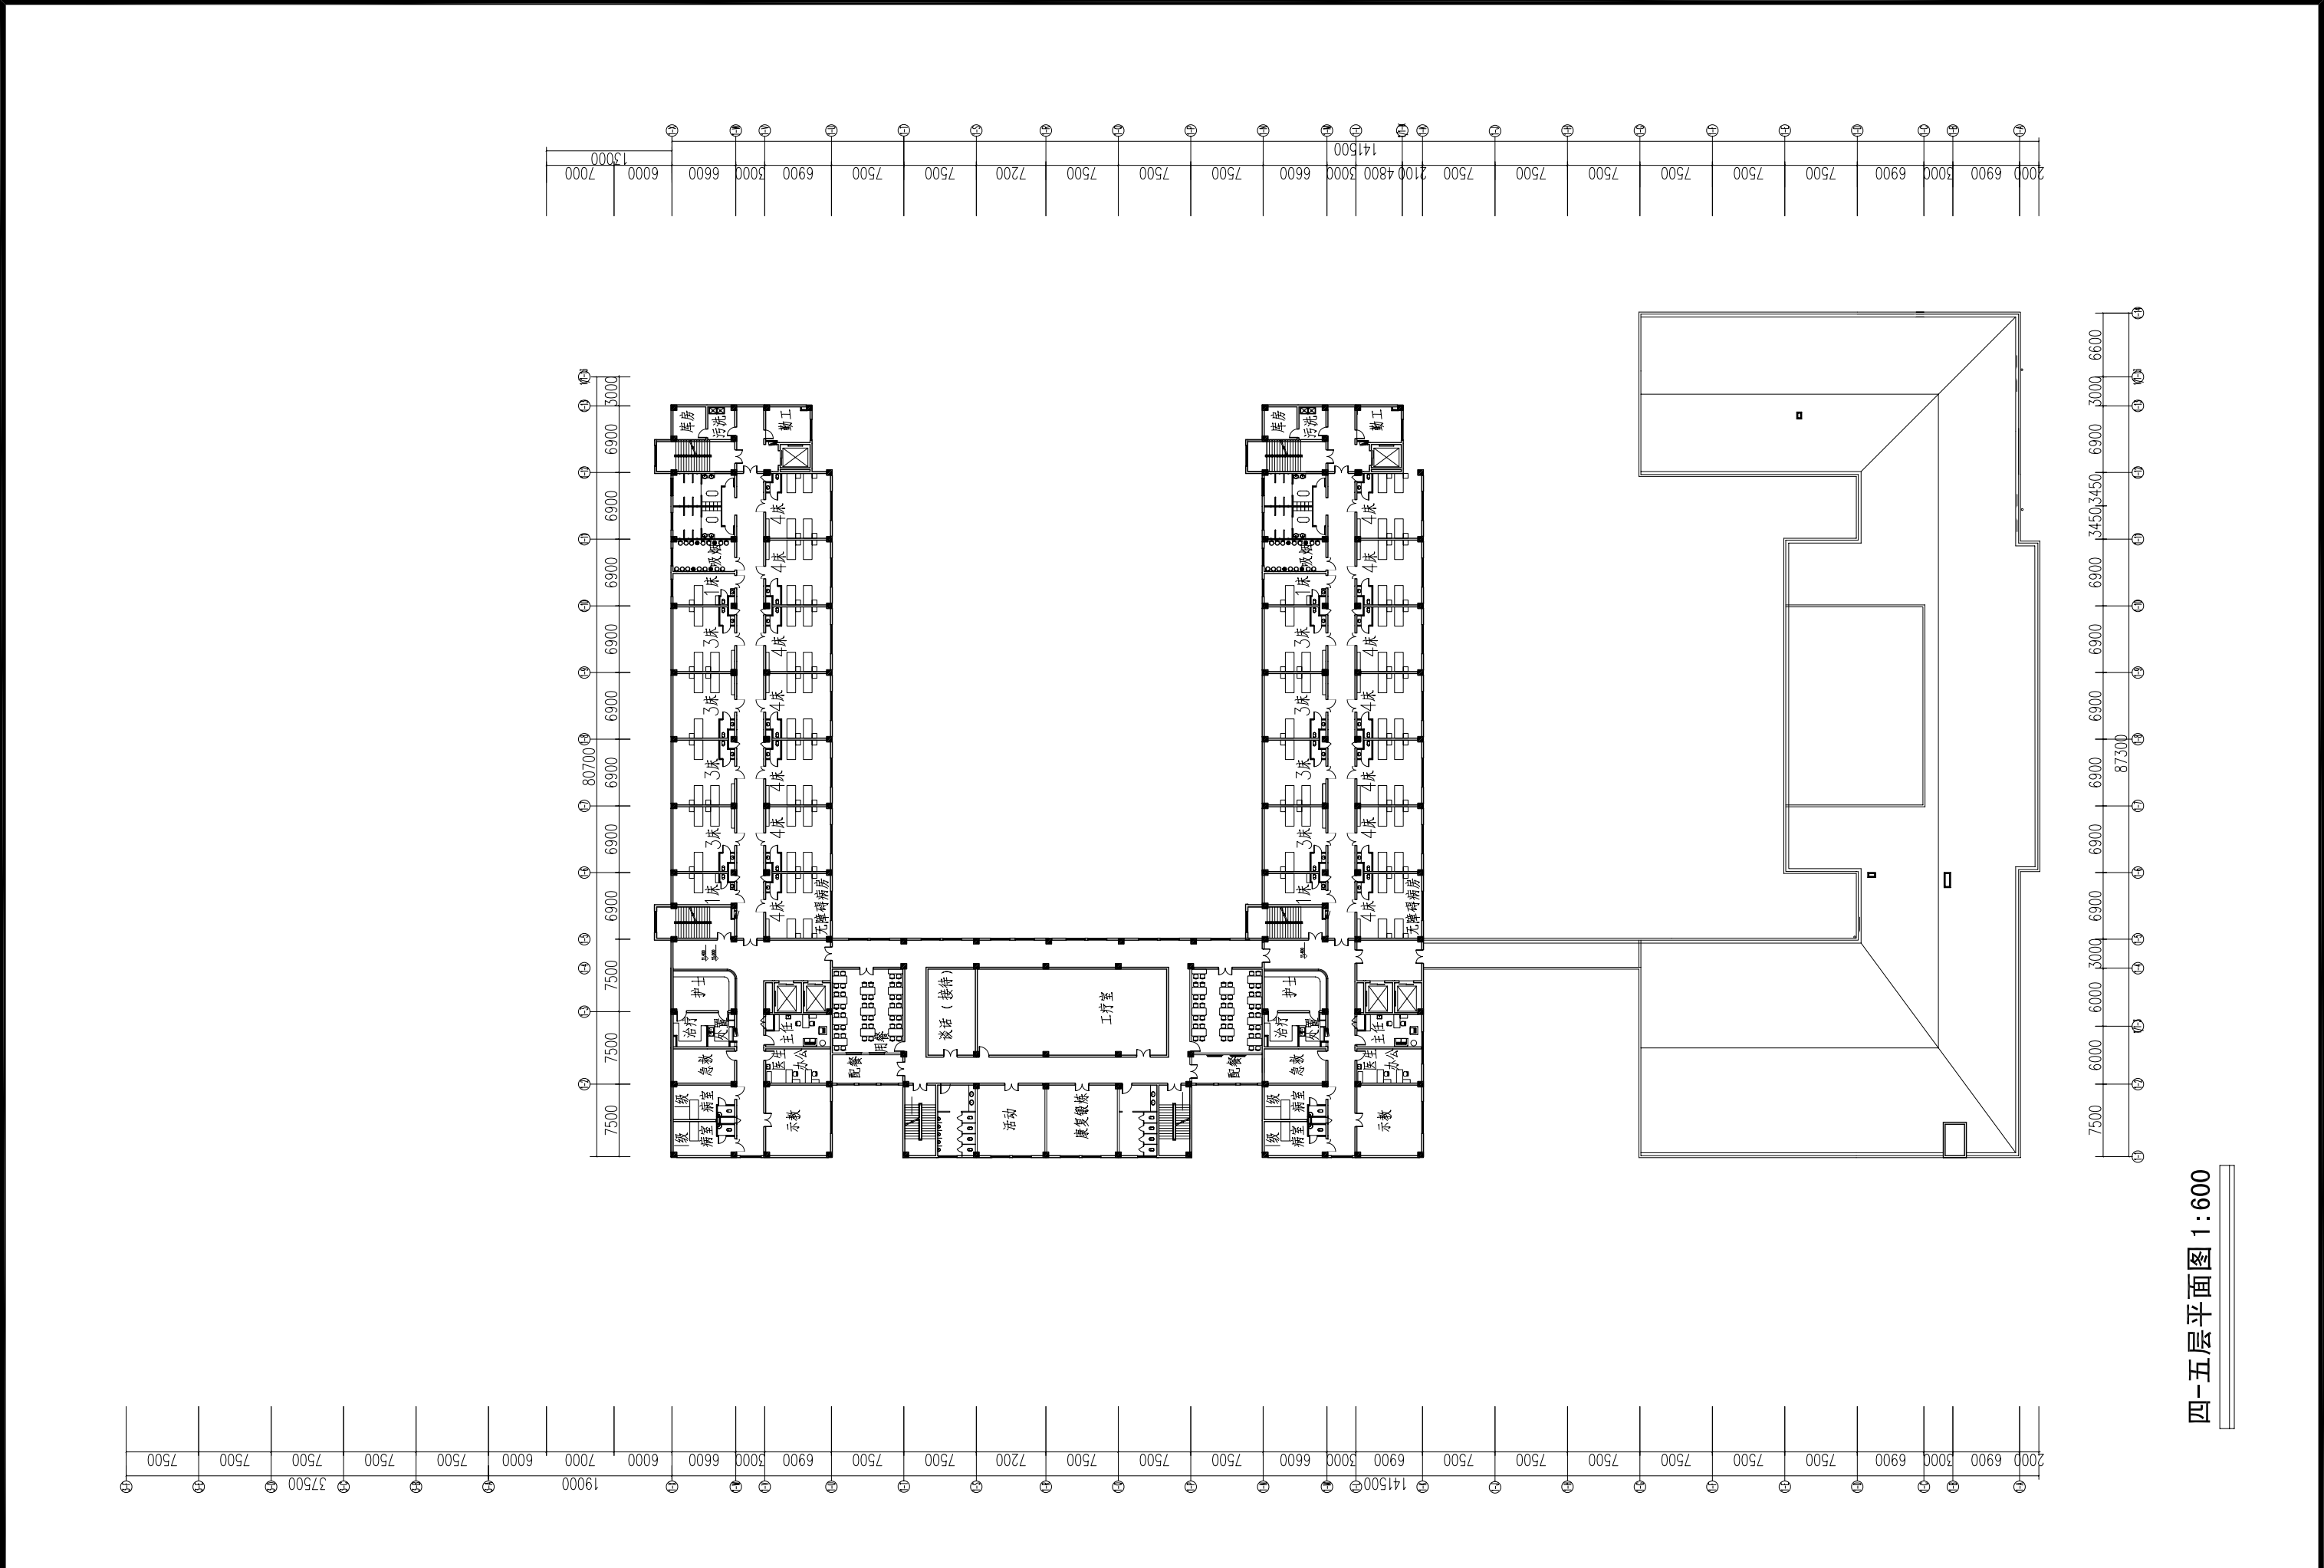


四-五层平面图 1:600

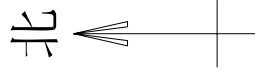

规划道路

主入口

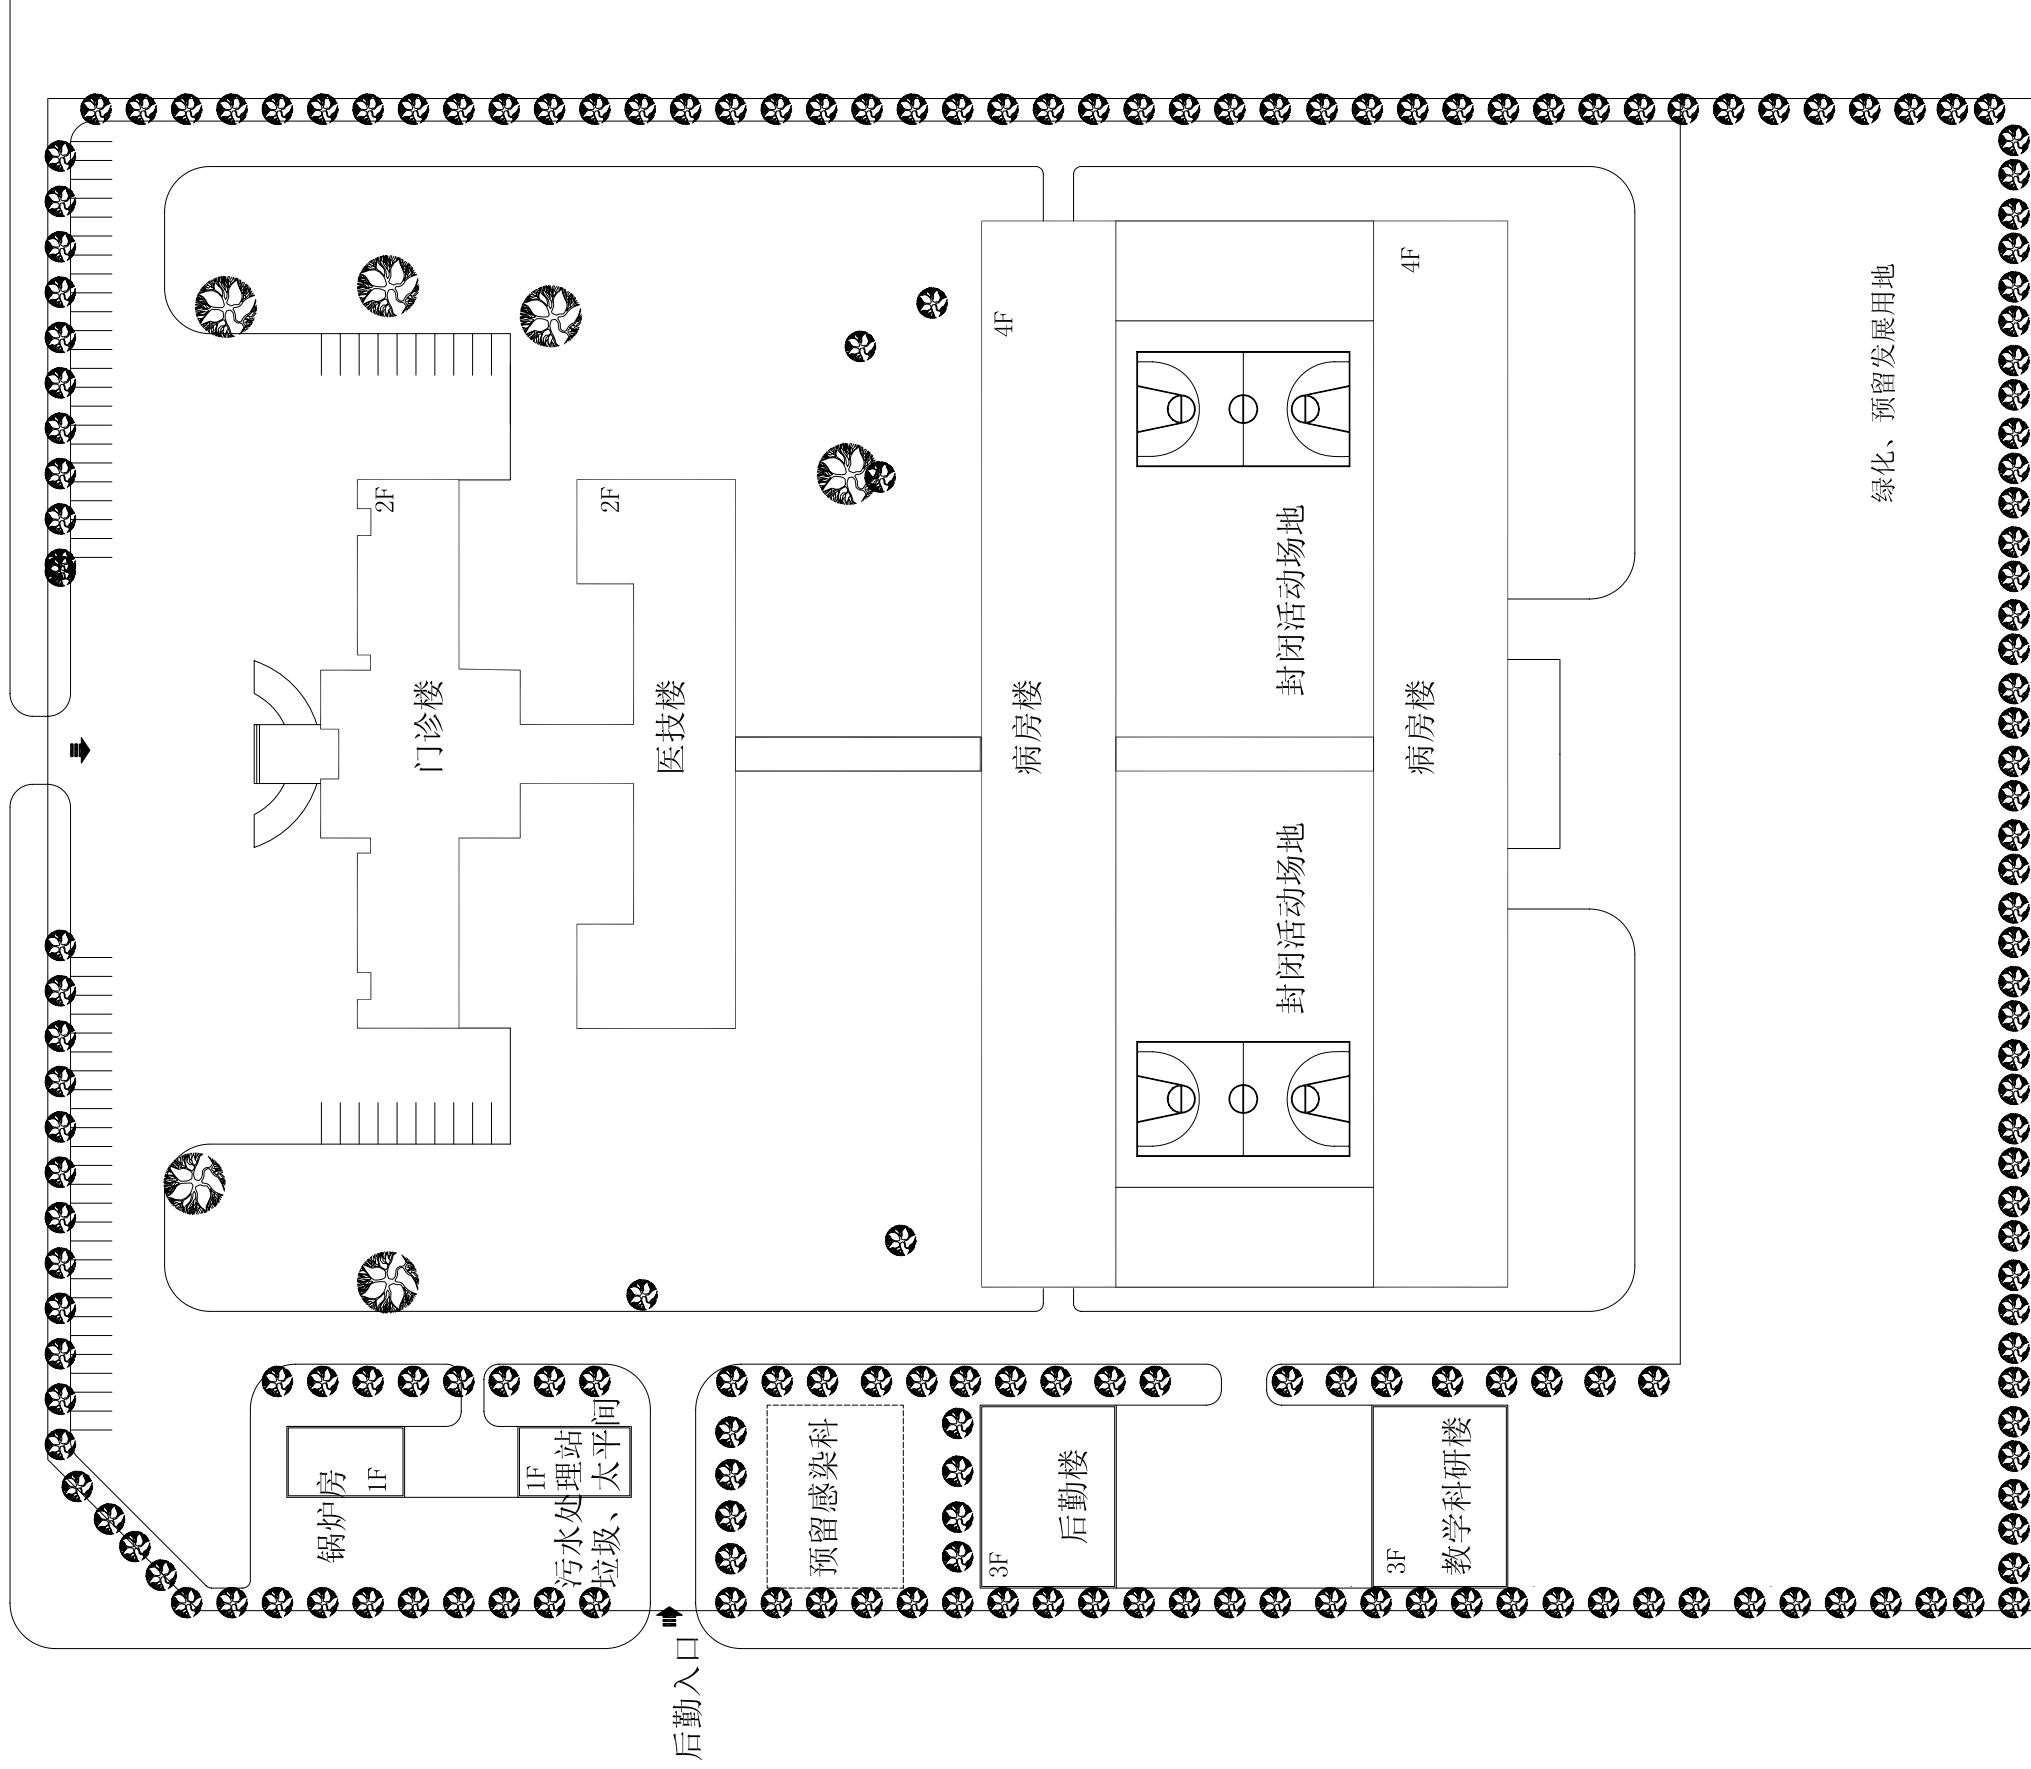


绿化、预留发展用地

主要技术经济指标

用地面积	51500m ²
总建筑面积	32109m ²
床位数	502 张
床均面积	63.9m ² /床

总平面图 1:1000



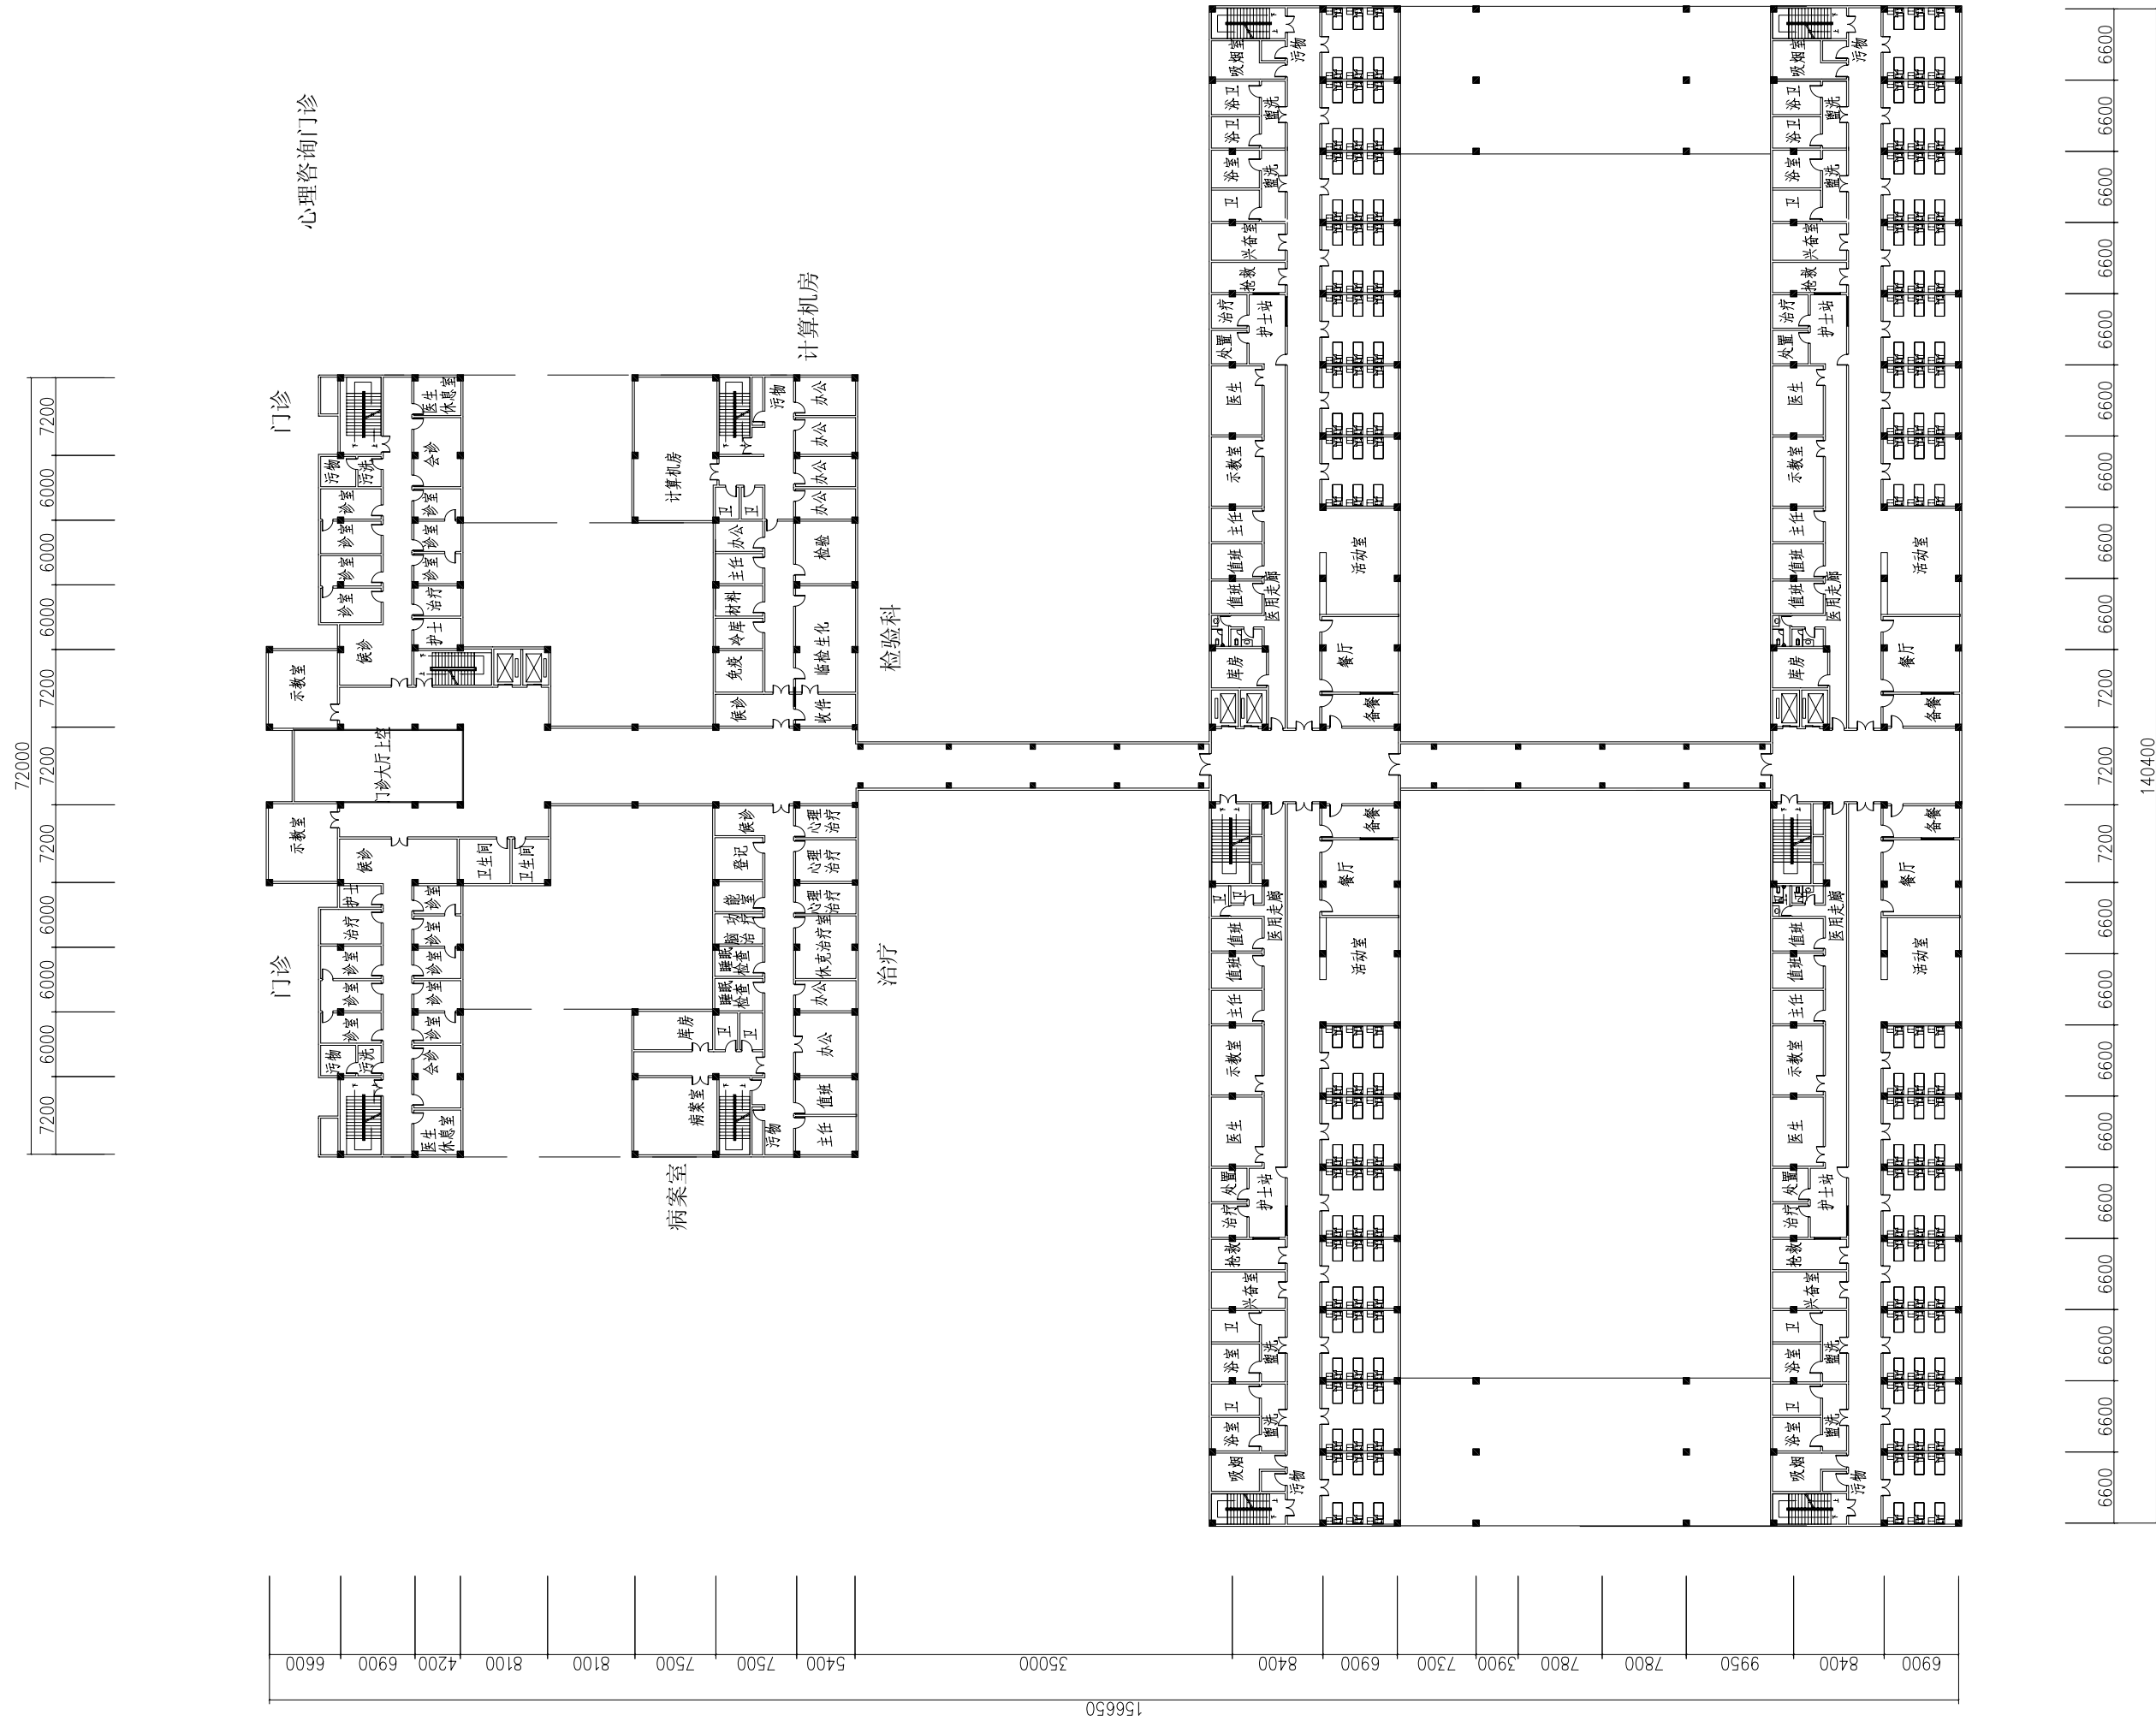

二层平面图 1:600

